


ARSITEKTUR
PERENCANAAN PEMBANGUNAN

MUSHOLA
DARUL SHOLIHIN

DAFTAR GAMBAR PERENCANAAN PEMBANGUNAN

DAFTAR ISI GAMBAR ARSITEKTUR

NO GAMBAR	JUDUL GAMBAR	HAL - GAMBAR
ARSITEKTUR		
01. DENAH, TAMPAK & POTONGAN		
ARS	RENCANA DENAH	1101
ARS	RENCANA DENAH ATAP	1102
ARS	TAMPAK DEPAN	1103
ARS	TAMPAK BELAKANG	1104
ARS	TAMPAK SAMPING KANAN	1105
ARS	TAMPAK SAMPING KIRI	1106
ARS	POTONGAN A-A	1107
ARS	POTONGAN B-B	1108
02. RENCANA POLA LANTAI		
ARS	RENCANA POLA LANTAI	1109
ARS	DETAIL LANTAI	1110
03. RENCANA DINDING		
ARS	RENCANA DINDING	1111
04. RENCANA KUSEN		
ARS	RENCANA KUSEN	1112
ARS	DETAIL KUSEN	1113
05. RENCANA PLAFOND		
ARS	RENCANA PLAFOND	1114
ARS	RENCANA RANGKA PLAFOND	1115
ARS	DETAIL PLAFOND	1116
06. DETAIL TOILET		
ARS	KEYPLAN TOILET	1117
ARS	DETAIL TOILET	1118
ARS	DETAIL TOILET	1119
ARS	DETAIL TOILET	1120
ARS	DETAIL TOILET	1121

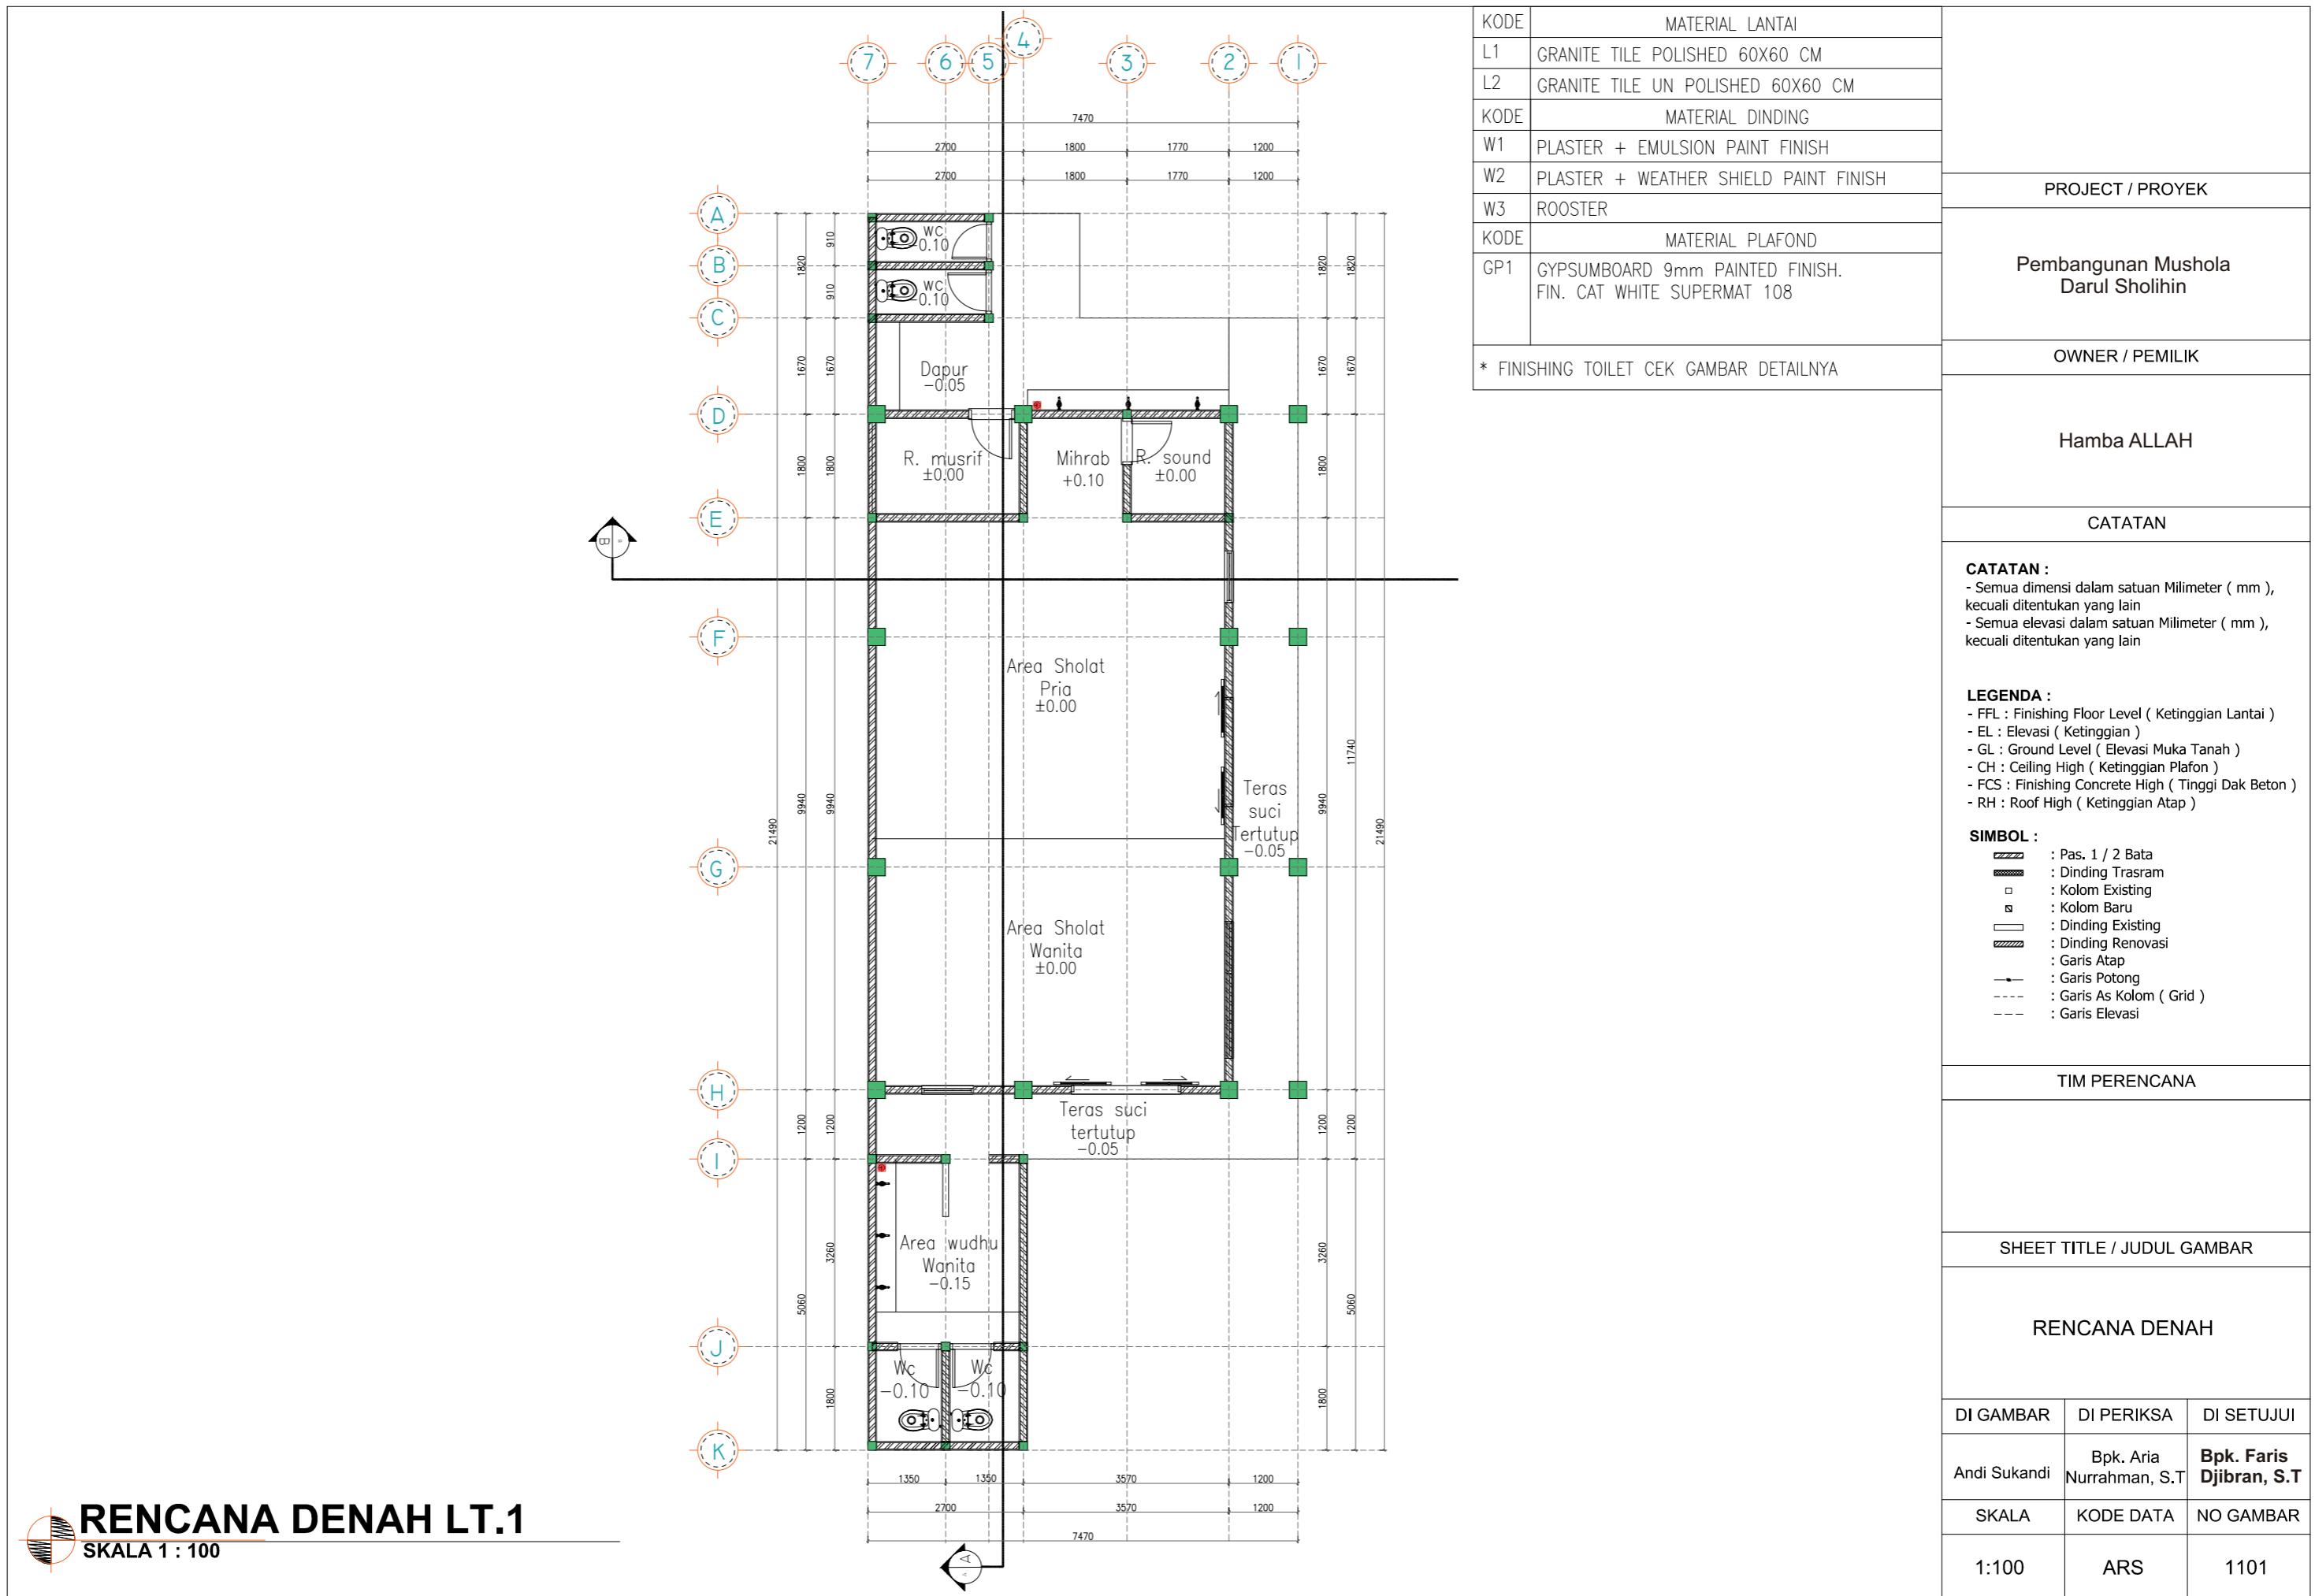

		PROJECT / PROYEK																					
		KODE	MATERIAL LANTAI																				
		L1	GRANITE TILE POLISHED 60X60 CM																				
		L2	GRANITE TILE UN POLISHED 60X60 CM																				
		KODE	MATERIAL DINDING																				
		W1	PLASTER + EMULSION PAINT FINISH																				
		W2	PLASTER + WEATHER SHIELD PAINT FINISH																				
		W3	ROOSTER																				
		KODE	MATERIAL PLAFOND																				
		GP1	GYPSUMBOARD 9mm PAINTED FINISH. FIN. CAT WHITE SUPERMAT 108																				
* FINISHING TOILET CEK GAMBAR DETAILNYA		OWNER / PEMILIK																					
		Hamba ALLAH																					
		CATATAN																					
		CATATAN : <ul style="list-style-type: none"> - Semua dimensi dalam satuan Milimeter (mm), kecuali ditentukan yang lain - Semua elevasi dalam satuan Milimeter (mm), kecuali ditentukan yang lain 																					
		LEGENDA : <ul style="list-style-type: none"> - FFL : Finishing Floor Level (Ketinggian Lantai) - EL : Elevasi (Ketinggian) - GL : Ground Level (Elevasi Muka Tanah) - CH : Ceiling High (Ketinggian Plafon) - FCS : Finishing Concrete High (Tinggi Dak Beton) - RH : Roof High (Ketinggian Atap) 																					
		SIMBOL : <table border="0"> <tr> <td></td><td>: Pas. 1 / 2 Bata</td></tr> <tr> <td></td><td>: Dinding Trasram</td></tr> <tr> <td></td><td>: Kolom Existing</td></tr> <tr> <td></td><td>: Kolom Baru</td></tr> <tr> <td></td><td>: Dinding Existing</td></tr> <tr> <td></td><td>: Dinding Renovasi</td></tr> <tr> <td></td><td>: Garis Atap</td></tr> <tr> <td></td><td>: Garis Potong</td></tr> <tr> <td></td><td>: Garis As Kolom (Grid)</td></tr> <tr> <td></td><td>: Garis Elevasi</td></tr> </table>			: Pas. 1 / 2 Bata		: Dinding Trasram		: Kolom Existing		: Kolom Baru		: Dinding Existing		: Dinding Renovasi		: Garis Atap		: Garis Potong		: Garis As Kolom (Grid)		: Garis Elevasi
	: Pas. 1 / 2 Bata																						
	: Dinding Trasram																						
	: Kolom Existing																						
	: Kolom Baru																						
	: Dinding Existing																						
	: Dinding Renovasi																						
	: Garis Atap																						
	: Garis Potong																						
	: Garis As Kolom (Grid)																						
	: Garis Elevasi																						
		TIM PERENCANA																					
		SHEET TITLE / JUDUL GAMBAR																					
		RENCANA DENAH ATAP																					
		DI GAMBAR	DI PERIKSA																				
		Andi Sukandi	Bpk. Aria Nurrahman, S.T																				
		SKALA	KODE DATA																				
		1:100	ARS																				
		NO GAMBAR																					
		1102																					

RENCANA DENAH ATAP

SKALA 1 : 100

KODE	MATERIAL LANTAI
L1	GRANITE TILE POLISHED 60X60 CM
L2	GRANITE TILE UN POLISHED 60X60 CM
KODE	MATERIAL DINDING
W1	PLASTER + EMULSION PAINT FINISH
W2	PLASTER + WEATHER SHIELD PAINT FINISH
W3	ROOSTER
KODE	MATERIAL PLAFOND
GP1	GYPSUMBOARD 9mm PAINTED FINISH. FIN. CAT WHITE SUPERMAT 108
* FINISHING TOILET CEK GAMBAR DETAILNYA	

PROJECT / PROYEK

Pembangunan Mushola
Darul Sholihin

OWNER / PEMILIK

Hamba ALLAH

CATATAN

CATATAN :

- Semua dimensi dalam satuan Milimeter (mm), kecuali ditentukan yang lain
- Semua elevasi dalam satuan Milimeter (mm), kecuali ditentukan yang lain

LEGENDA :

- FFL : Finishing Floor Level (Ketinggian Lantai)
- EL : Elevasi (Ketinggian)
- GL : Ground Level (Elevasi Muka Tanah)
- CH : Ceiling High (Ketinggian Plafon)
- FCS : Finishing Concrete High (Tinggi Dak Beton)
- RH : Roof High (Ketinggian Atap)

SIMBOL :


- | | |
|-----|---------------------------|
| — | : Pas. 1 / 2 Bata |
| — | : Dinding Trasram |
| — | : Kolom Existing |
| --- | : Kolom Baru |
| — | : Dinding Existing |
| — | : Dinding Renovasi |
| -- | : Garis Atap |
| -- | : Garis Potong |
| -- | : Garis As Kolom (Grid) |
| - | : Garis Elevasi |

TIM PERENCANA

SHEET TITLE / JUDUL GAMBAR

TAMPAK DEPAN

DI GAMBAR	DI PERIKSA	DI SETUJUI
Andi Sukandi	Bpk. Aria Nurrahman, S.T	Bpk. Faris Djibrain, S.T
SKALA	KODE DATA	NO GAMBAR
1:100	ARS	1103

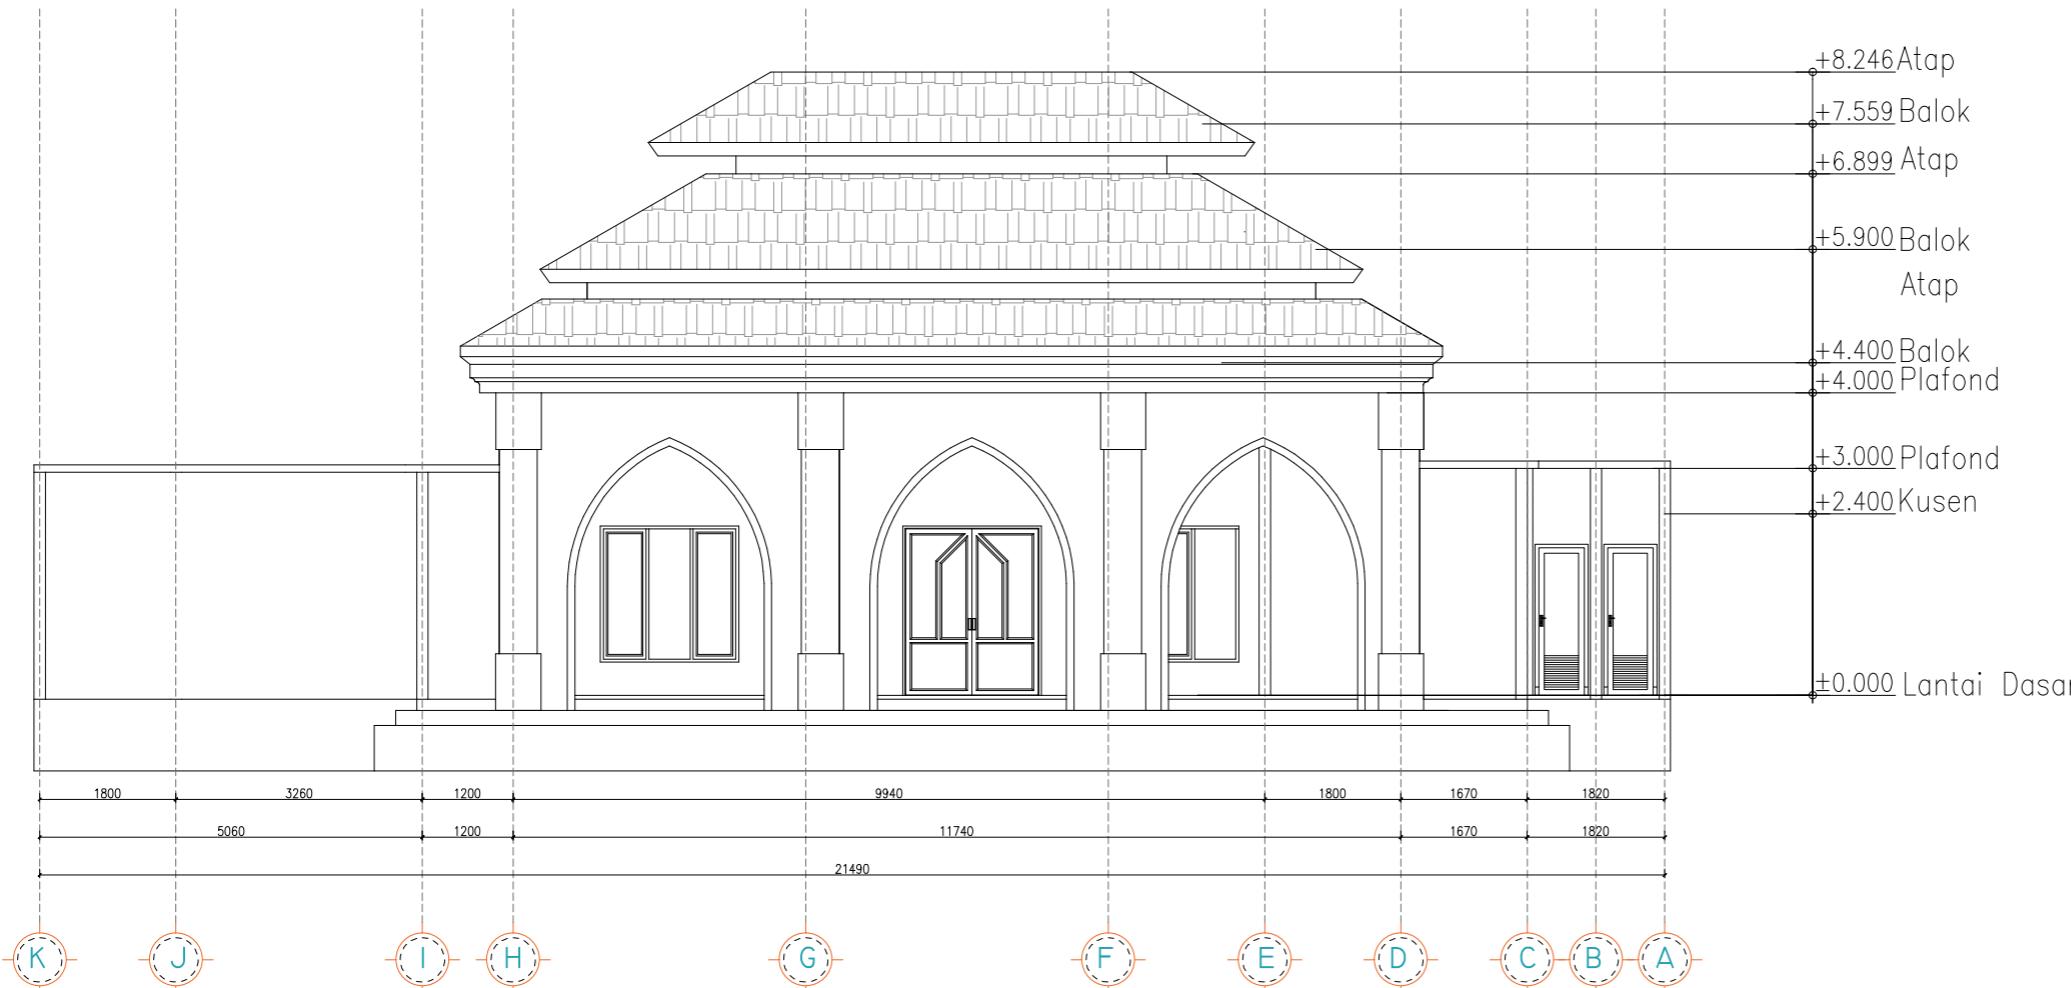

RENCANA TAMPAK DEPAN

SKALA 1 : 100

KODE	MATERIAL LANTAI	
L1	GRANITE TILE POLISHED 60X60 CM	
L2	GRANITE TILE UN POLISHED 60X60 CM	
KODE	MATERIAL DINDING	
W1	PLASTER + EMULSION PAINT FINISH	
W2	PLASTER + WEATHER SHIELD PAINT FINISH	
W3	ROOSTER	
KODE	MATERIAL PLAFOND	
GP1	GYPSUMBOARD 9mm PAINTED FINISH. FIN. CAT WHITE SUPERMAT 108	
* FINISHING TOILET CEK GAMBAR DETAILNYA		

PROJECT / PROYEK

Pembangunan Mushola
Darul Sholihin

OWNER / PEMILIK

Hamba ALLAH

CATATAN

CATATAN :
 - Semua dimensi dalam satuan Milimeter (mm),
 kecuali ditentukan yang lain
 - Semua elevasi dalam satuan Milimeter (mm),
 kecuali ditentukan yang lain

LEGENDA :
 - FFL : Finishing Floor Level (Ketinggian Lantai)
 - EL : Elevasi (Ketinggian)
 - GL : Ground Level (Elevasi Muka Tanah)
 - CH : Ceiling High (Ketinggian Plafon)
 - FCS : Finishing Concrete High (Tinggi Dak Beton)
 - RH : Roof High (Ketinggian Atap)


SIMBOL :
 : Pas. 1 / 2 Bata
 : Dinding Trasram
 : Kolom Existing
 : Kolom Baru
 : Dinding Existing
 : Dinding Renovasi
 : Garis Atap
 : Garis Potong
 : Garis As Kolom (Grid)
 : Garis Elevasi

TIM PERENCANA

SHEET TITLE / JUDUL GAMBAR

TAMPAK BELAKANG

DI GAMBAR	DI PERIKSA	DI SETUJUI
Andi Sukandi	Bpk. Aria Nurrahman, S.T	Bpk. Faris Djibrain, S.T
SKALA	KODE DATA	NO GAMBAR
1:100	ARS	1104

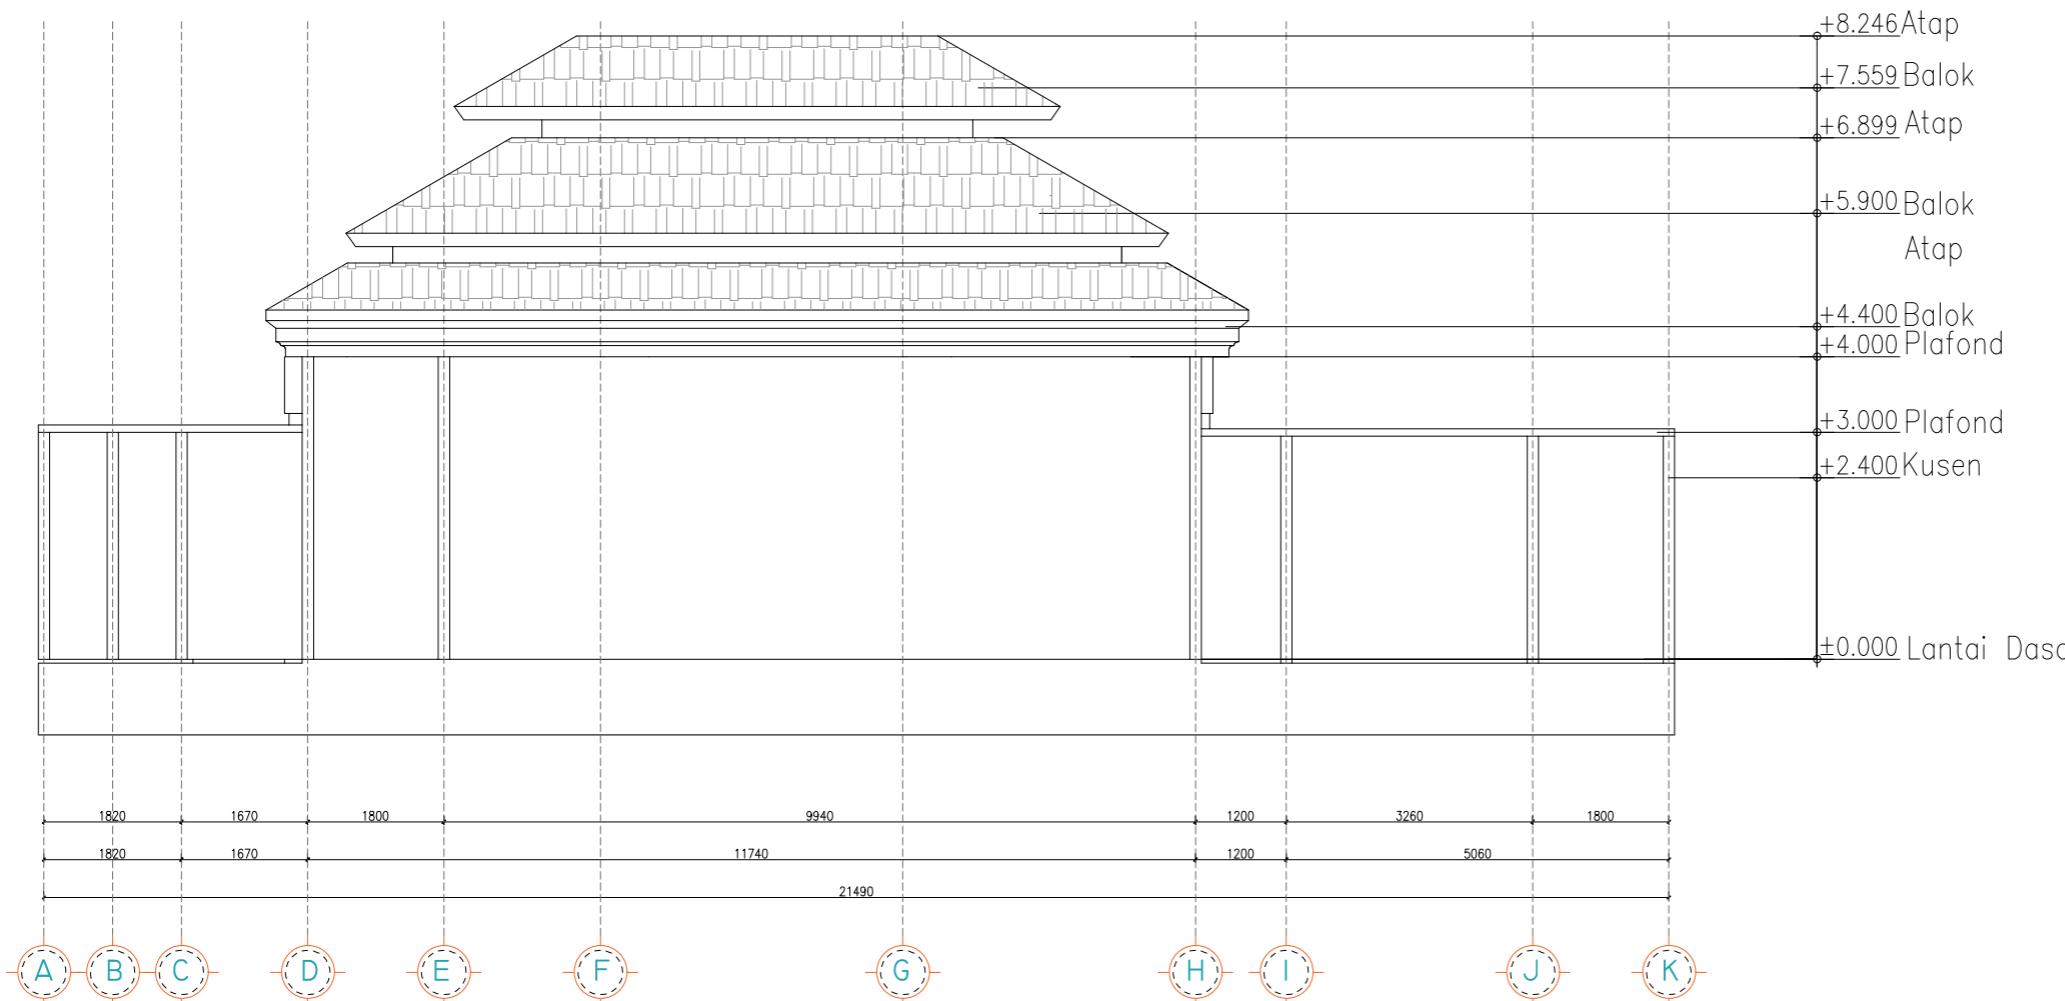

RENCANA TAMPAK BELAKANG

SKALA 1 : 100

1:100

KODE	MATERIAL LANTAI	
L1	GRANITE TILE POLISHED 60X60 CM	
L2	GRANITE TILE UN POLISHED 60X60 CM	
KODE	MATERIAL DINDING	
W1	PLASTER + EMULSION PAINT FINISH	PROJECT / PROYEK
W2	PLASTER + WEATHER SHIELD PAINT FINISH	
W3	ROOSTER	
KODE	MATERIAL PLAFOND	
GP1	GYPSUMBOARD 9mm PAINTED FINISH. FIN. CAT WHITE SUPERMAT 108	Pembangunan Mushola Darul Sholihin
* FINISHING TOILET CEK GAMBAR DETAILNYA		OWNER / PEMILIK

* FINISHING TOILET CEK GAMBAR DETAILNYA

PROJECT / PROYEK

Pembangunan Mushola Darul Sholihin

OWNER / PEMILIK

Hamba ALLAH

CATATAN

CATATAN :

- Semua dimensi dalam satuan Milimeter (mm), kecuali ditentukan yang lain
- Semua elevasi dalam satuan Milimeter (mm), kecuali ditentukan yang lain

LEGENDA :

- FFL : Finishing Floor Level (Ketinggian Lantai)
- EL : Elevasi (Ketinggian)
- GL : Ground Level (Elevasi Muka Tanah)
- CH : Ceiling High (Ketinggian Plafon)
- FCS : Finishing Concrete High (Tinggi Dak Beton)
- RH : Roof High (Ketinggian Atap)


SIMBOL :	:	Penjelasan
	:	Pas. 1 / 2 Bata
	:	Dinding Trasram
	:	Kolom Existing
	:	Kolom Baru
	:	Dinding Existing
	:	Dinding Renovasi
	:	Garis Atap
	:	Garis Potong
	:	Garis As Kolom (Grid)
	:	Garis Elevasi

TIM PERENCANA

SHEET TITLE / JUDUL GAMBAR

TAMPAK SAMPING KANAN

DI GAMBAR	DI PERIKSA	DI SETUJUI
Andi Sukandi	Bpk. Aria Nurrahman, S.T	Bpk. Faris Djibrani, S.T
SKALA	KODE DATA	NO GAMBAR
1:100	ARS	1105

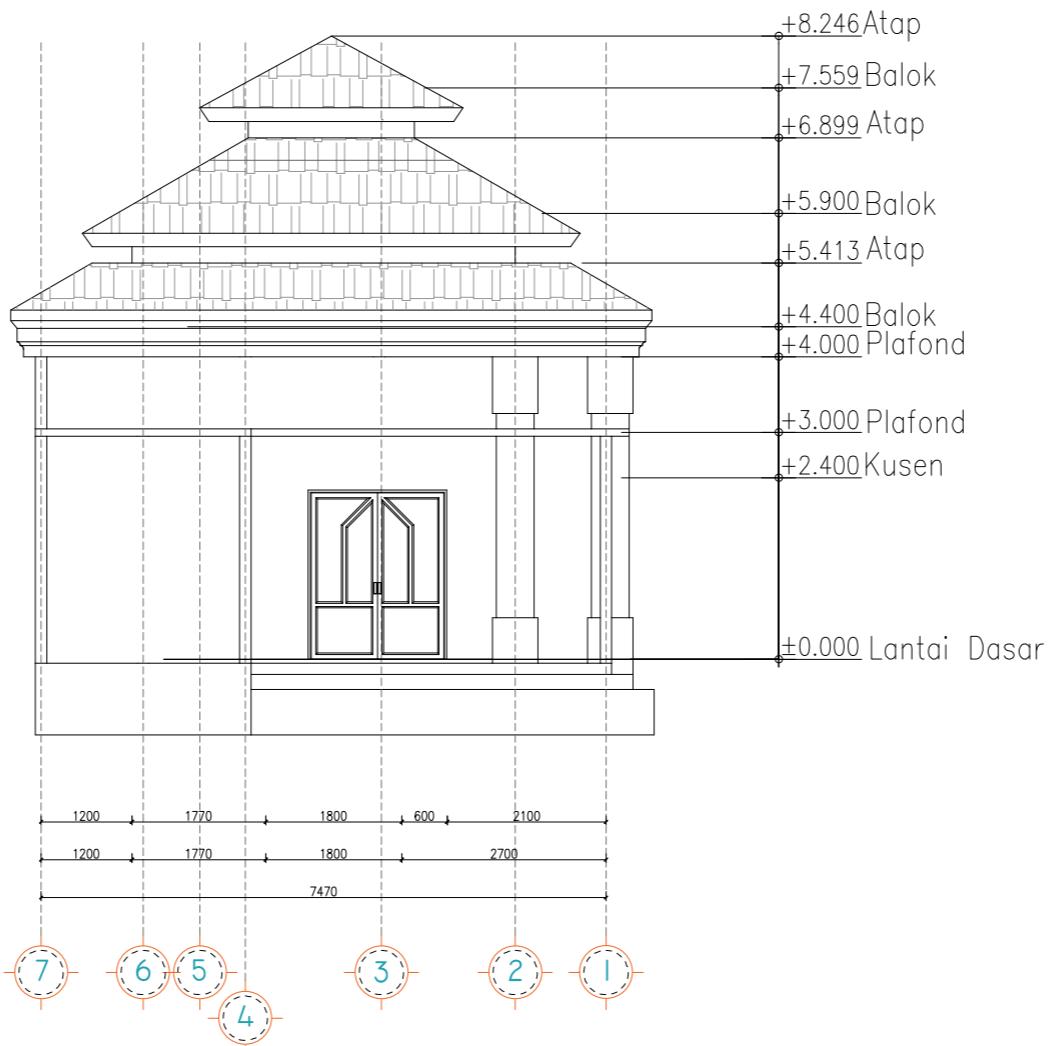

RENCANA TAMPAK SAMPING KANAN

SKALA 1 : 100

KODE	MATERIAL LANTAI	
L1	GRANITE TILE POLISHED 60X60 CM	
L2	GRANITE TILE UN POLISHED 60X60 CM	
KODE	MATERIAL DINDING	
W1	PLASTER + EMULSION PAINT FINISH	
W2	PLASTER + WEATHER SHIELD PAINT FINISH	
W3	ROOSTER	PROJECT / PROYEK
KODE	MATERIAL PLAFOND	Pembangunan Mushola Darul Sholihin
GP1	GYPSUMBOARD 9mm PAINTED FINISH. FIN. CAT WHITE SUPERMAT 108	
* FINISHING TOILET CEK GAMBAR DETAILNYA		OWNER / PEMILIK

Hamba ALLAH

CATATAN

CATATAN :
 - Semua dimensi dalam satuan Milimeter (mm),
 kecuali ditentukan yang lain
 - Semua elevasi dalam satuan Milimeter (mm),
 kecuali ditentukan yang lain

LEGENDA :
 - FFL : Finishing Floor Level (Ketinggian Lantai)
 - EL : Elevasi (Ketinggian)
 - GL : Ground Level (Elevasi Muka Tanah)
 - CH : Ceiling High (Ketinggian Plafon)
 - FCS : Finishing Concrete High (Tinggi Dak Beton)
 - RH : Roof High (Ketinggian Atap)


SIMBOL :
 : Pas. 1 / 2 Bata
 : Dinding Trasram
 : Kolom Existing
 : Kolom Baru
 : Dinding Existing
 : Dinding Renovasi
 : Garis Atap
 : Garis Potong
 : Garis As Kolom (Grid)
 : Garis Elevasi

TIM PERENCANA

SHEET TITLE / JUDUL GAMBAR

TAMPAK SAMPING KIRI

DI GAMBAR	DI PERIKSA	DI SETUJUI
Andi Sukandi	Bpk. Aria Nurrahman, S.T	Bpk. Faris Djibrain, S.T
SKALA	KODE DATA	NO GAMBAR
1:100	ARS	1106

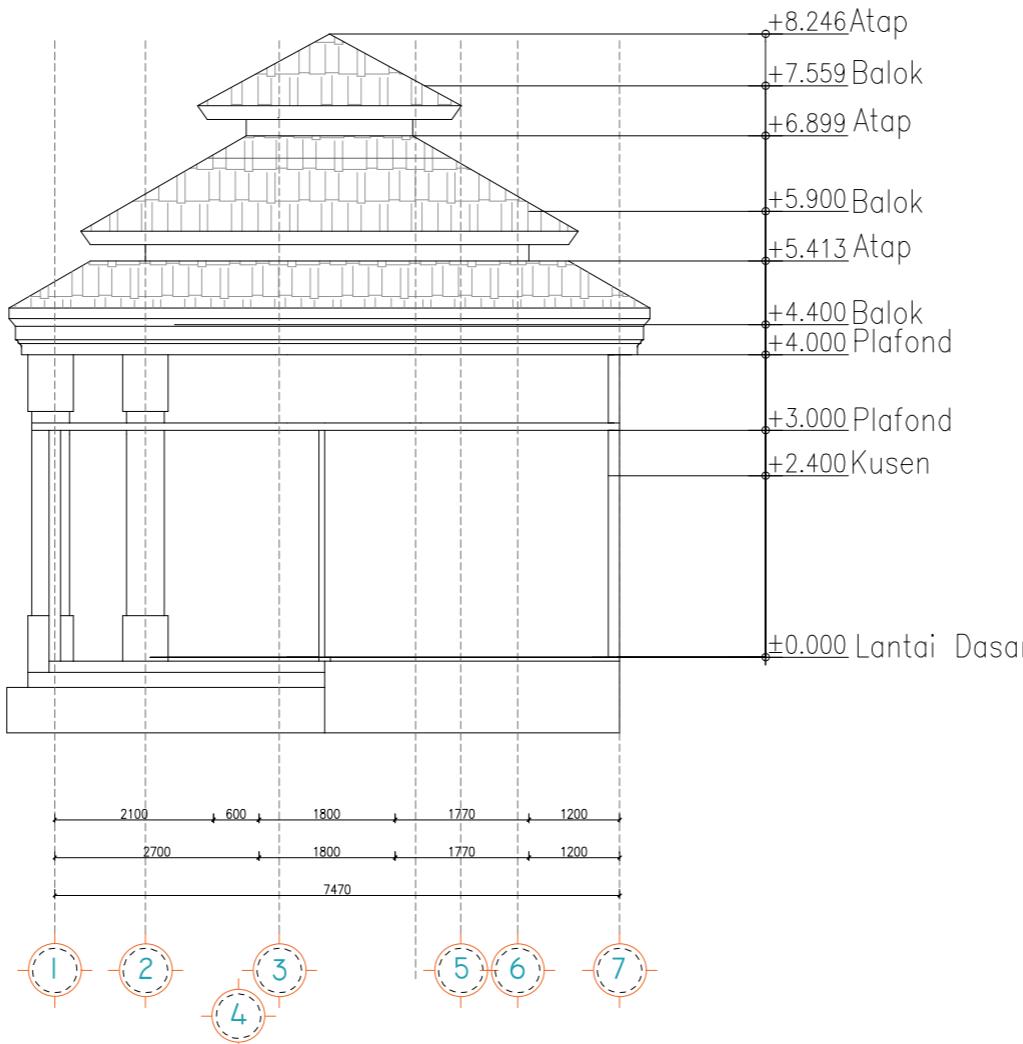

RENCANA TAMPAK SAMPING KIRI

SKALA 1 : 100

KODE	MATERIAL LANTAI
L1	GRANITE TILE POLISHED 60X60 CM
L2	GRANITE TILE UN POLISHED 60X60 CM
KODE	MATERIAL DINDING
W1	PLASTER + EMULSION PAINT FINISH
W2	PLASTER + WEATHER SHIELD PAINT FINISH
W3	ROOSTER
KODE	MATERIAL PLAFOND
GP1	GYPSUMBOARD 9mm PAINTED FINISH. FIN. CAT WHITE SUPERMAT 108

* FINISHING TOILET CEK GAMBAR DETAILNYA

PROJECT / PROYEK

Pembangunan Mushola
Darul Sholihin

OWNER / PEMILIK

Hamba ALLAH

CATATAN

CATATAN :
 - Semua dimensi dalam satuan Milimeter (mm),
 kecuali ditentukan yang lain
 - Semua elevasi dalam satuan Milimeter (mm),
 kecuali ditentukan yang lain

LEGENDA :
 - FFL : Finishing Floor Level (Ketinggian Lantai)
 - EL : Elevasi (Ketinggian)
 - GL : Ground Level (Elevasi Muka Tanah)
 - CH : Ceiling High (Ketinggian Plafon)
 - FCS : Finishing Concrete High (Tinggi Dak Beton)
 - RH : Roof High (Ketinggian Atap)


SIMBOL :

■■■■■	: Pas. 1 / 2 Bata
■■■■■	: Dinding Trasram
□	: Kolom Existing
■	: Kolom Baru
■■■■■	: Dinding Existing
■■■■■	: Dinding Renovasi
—●—	: Garis Atap
—●—	: Garis Potong
-----	: Garis As Kolom (Grid)
---	: Garis Elevasi

TIM PERENCANA

SHEET TITLE / JUDUL GAMBAR

POTONGAN A-A

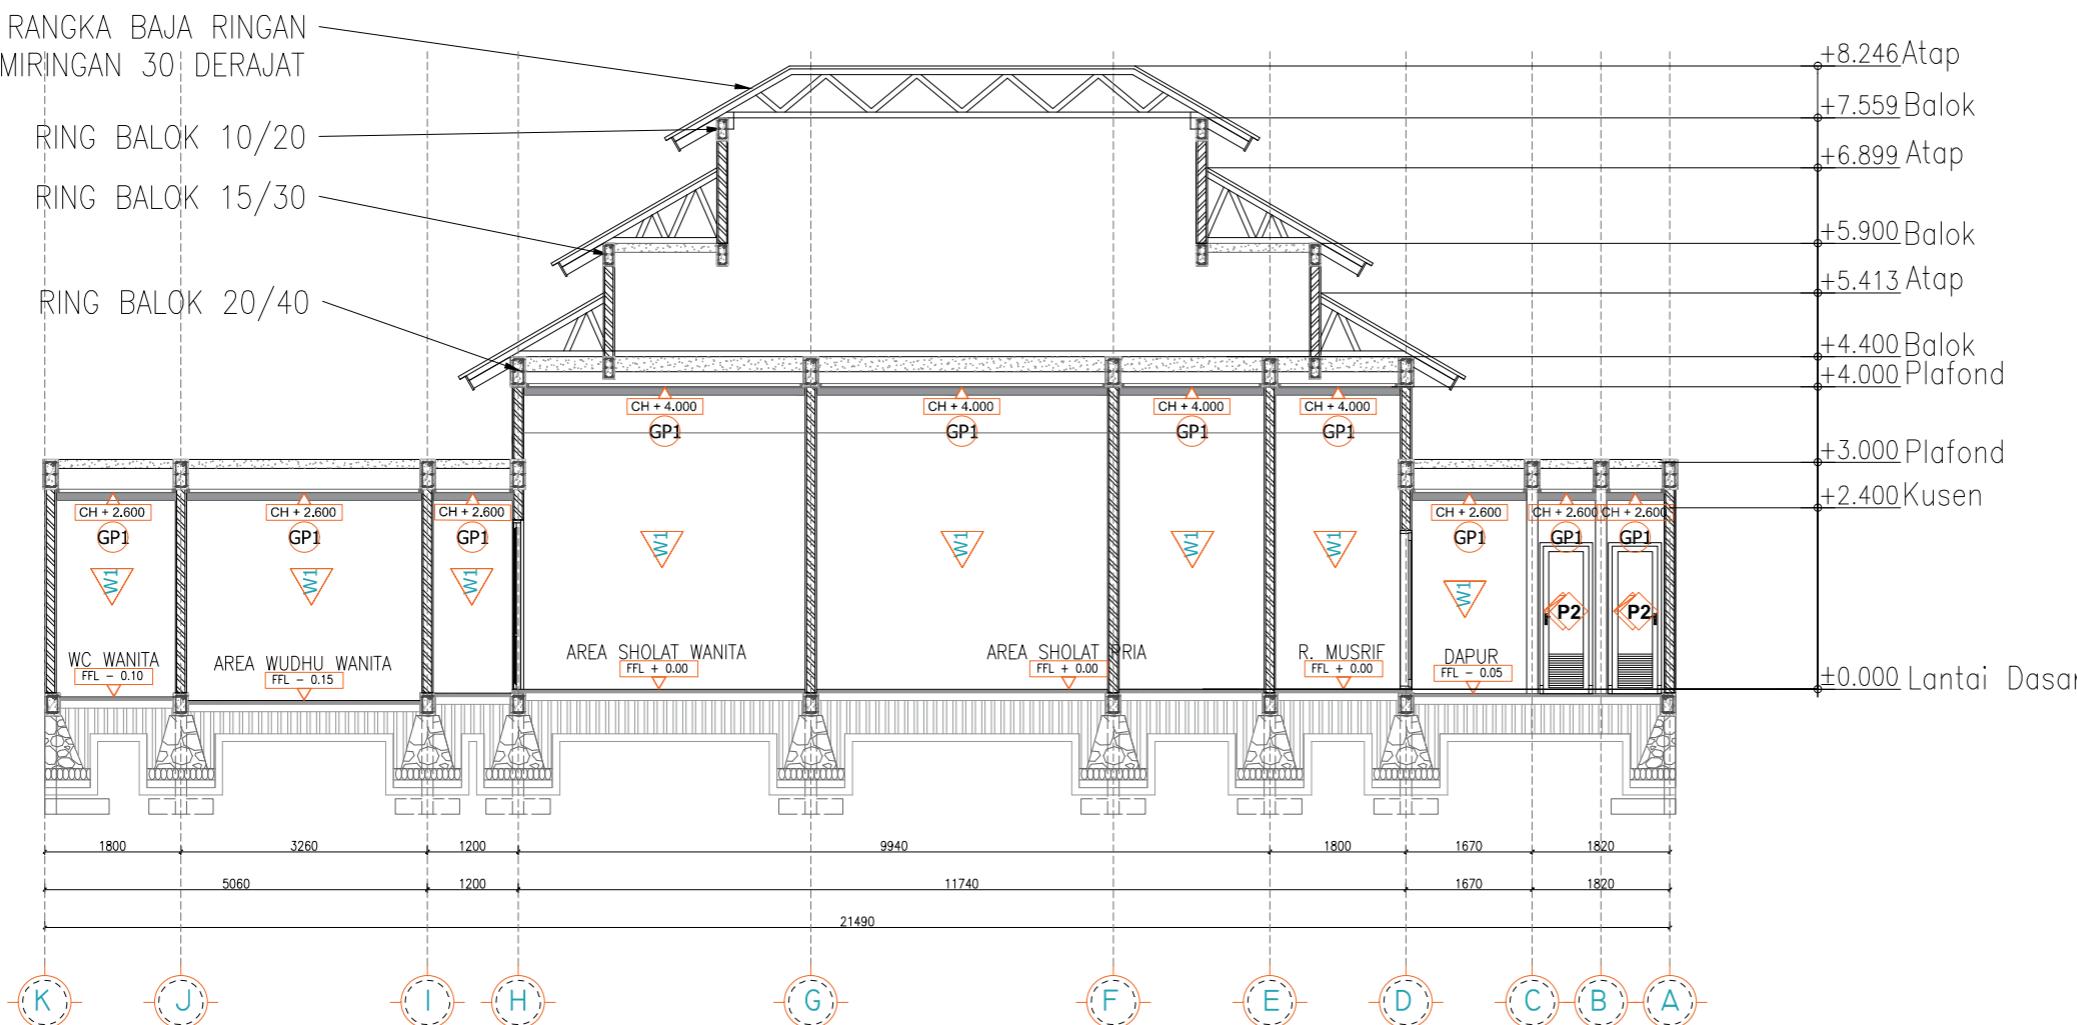

RENCANA POTONGAN A-A

SKALA 1 : 100

DI GAMBAR	DI PERIKSA	DI SETUJUI
Andi Sukandi	Bpk. Aria Nurrahman, S.T	Bpk. Faris Djibrain, S.T
SKALA	KODE DATA	NO GAMBAR
1:100	ARS	1107

KODE	MATERIAL LANTAI	PROJECT / PROYEK
L1	GRANITE TILE POLISHED 60X60 CM	
L2	GRANITE TILE UN POLISHED 60X60 CM	Pembangunan Mushola Darul Sholihin
KODE	MATERIAL DINDING	
W1	PLASTER + EMULSION PAINT FINISH	OWNER / PEMILIK
W2	PLASTER + WEATHER SHIELD PAINT FINISH	
W3	ROOSTER	Hamba ALLAH
KODE	MATERIAL PLAFOND	
GP1	GYPSUMBOARD 9mm PAINTED FINISH. FIN. CAT WHITE SUPERMAT 108	
* FINISHING TOILET CEK GAMBAR DETAILNYA		

PROJECT / PROYEK

Pembangunan Mushola
Darul Sholihin

OWNER / PEMILIK

Hamba ALLAH

CATATAN

CATATAN :
 - Semua dimensi dalam satuan Milimeter (mm),
 kecuali ditentukan yang lain
 - Semua elevasi dalam satuan Milimeter (mm),
 kecuali ditentukan yang lain

LEGENDA :
 - FFL : Finishing Floor Level (Ketinggian Lantai)
 - EL : Elevasi (Ketinggian)
 - GL : Ground Level (Elevasi Muka Tanah)
 - CH : Ceiling High (Ketinggian Plafond)
 - FCS : Finishing Concrete High (Tinggi Dak Beton)
 - RH : Roof High (Ketinggian Atap)


SIMBOL :
 : Pas. 1 / 2 Bata
 : Dinding Trasram
 : Kolom Existing
 : Kolom Baru
 : Dinding Existing
 : Dinding Renovasi
 : Garis Atap
 : Garis Potong
 : Garis As Kolom (Grid)
 : Garis Elevasi

TIM PERENCANA

SHEET TITLE / JUDUL GAMBAR


POTONGAN B-B

DI GAMBAR	DI PERIKSA	DI SETUJUI
Andi Sukandi	Bpk. Aria Nurrahman, S.T	Bpk. Faris Djibrain, S.T
SKALA	KODE DATA	NO GAMBAR
1:100	ARS	1108

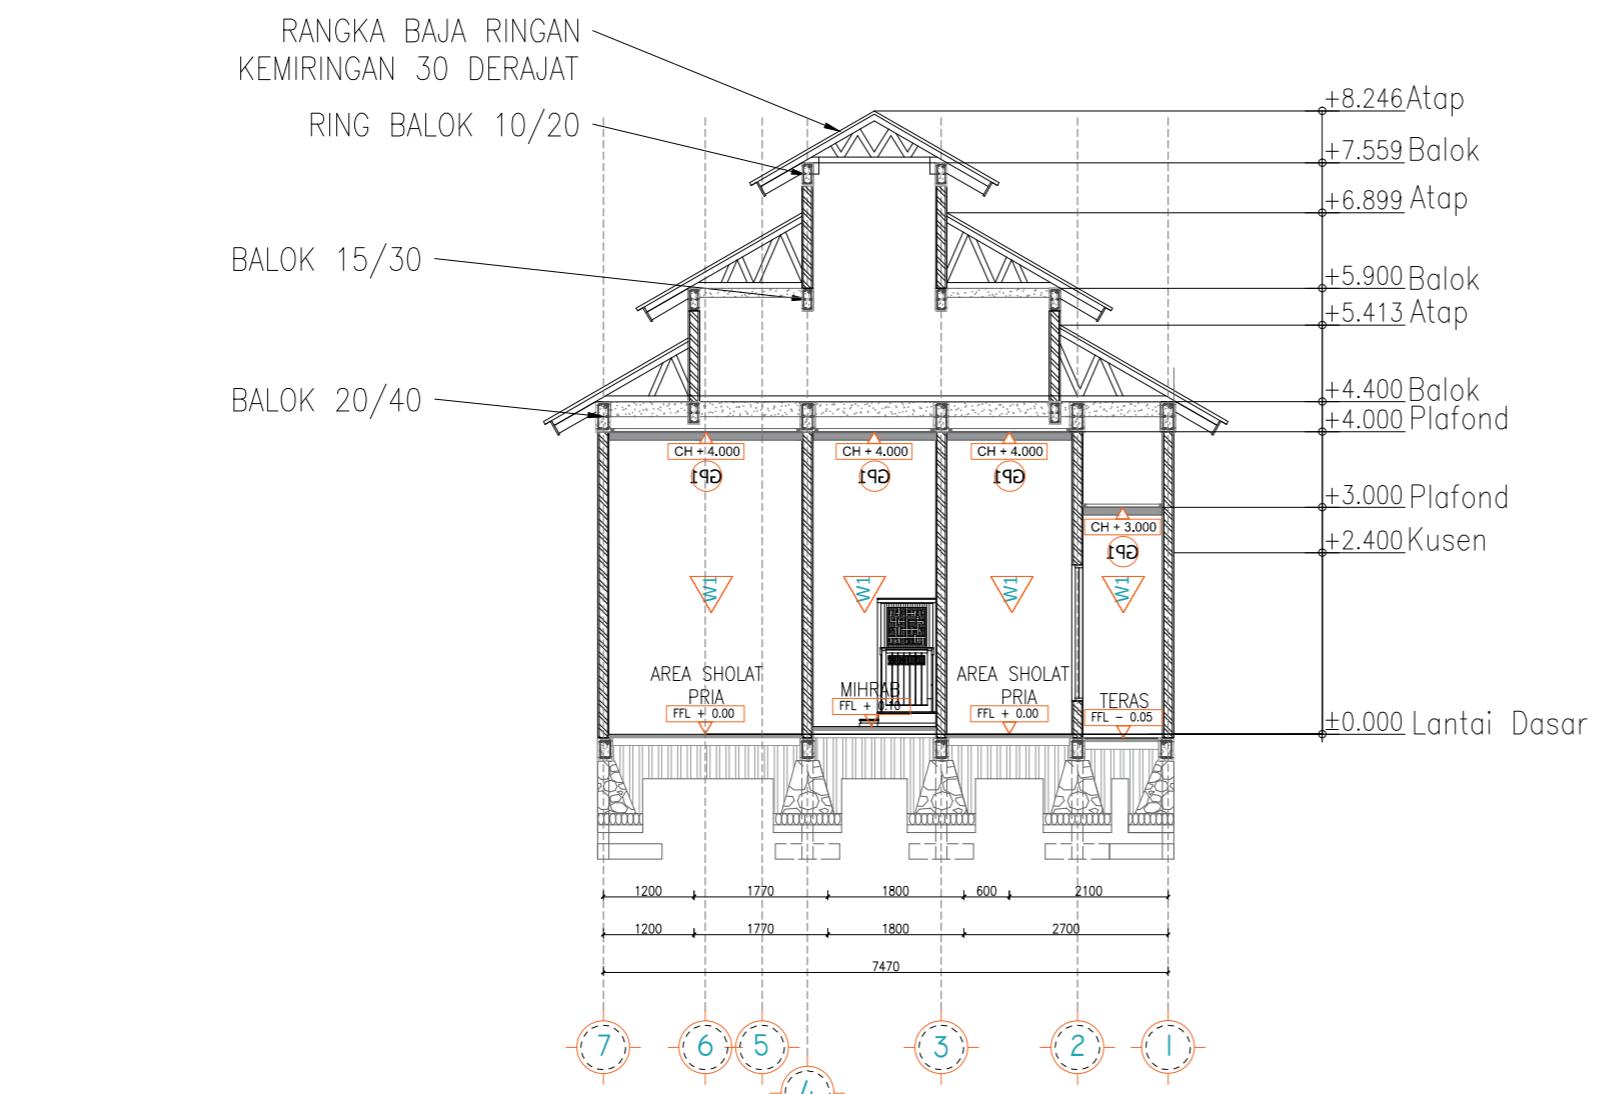

RENCANA POTONGAN B-B

SKALA 1 : 100

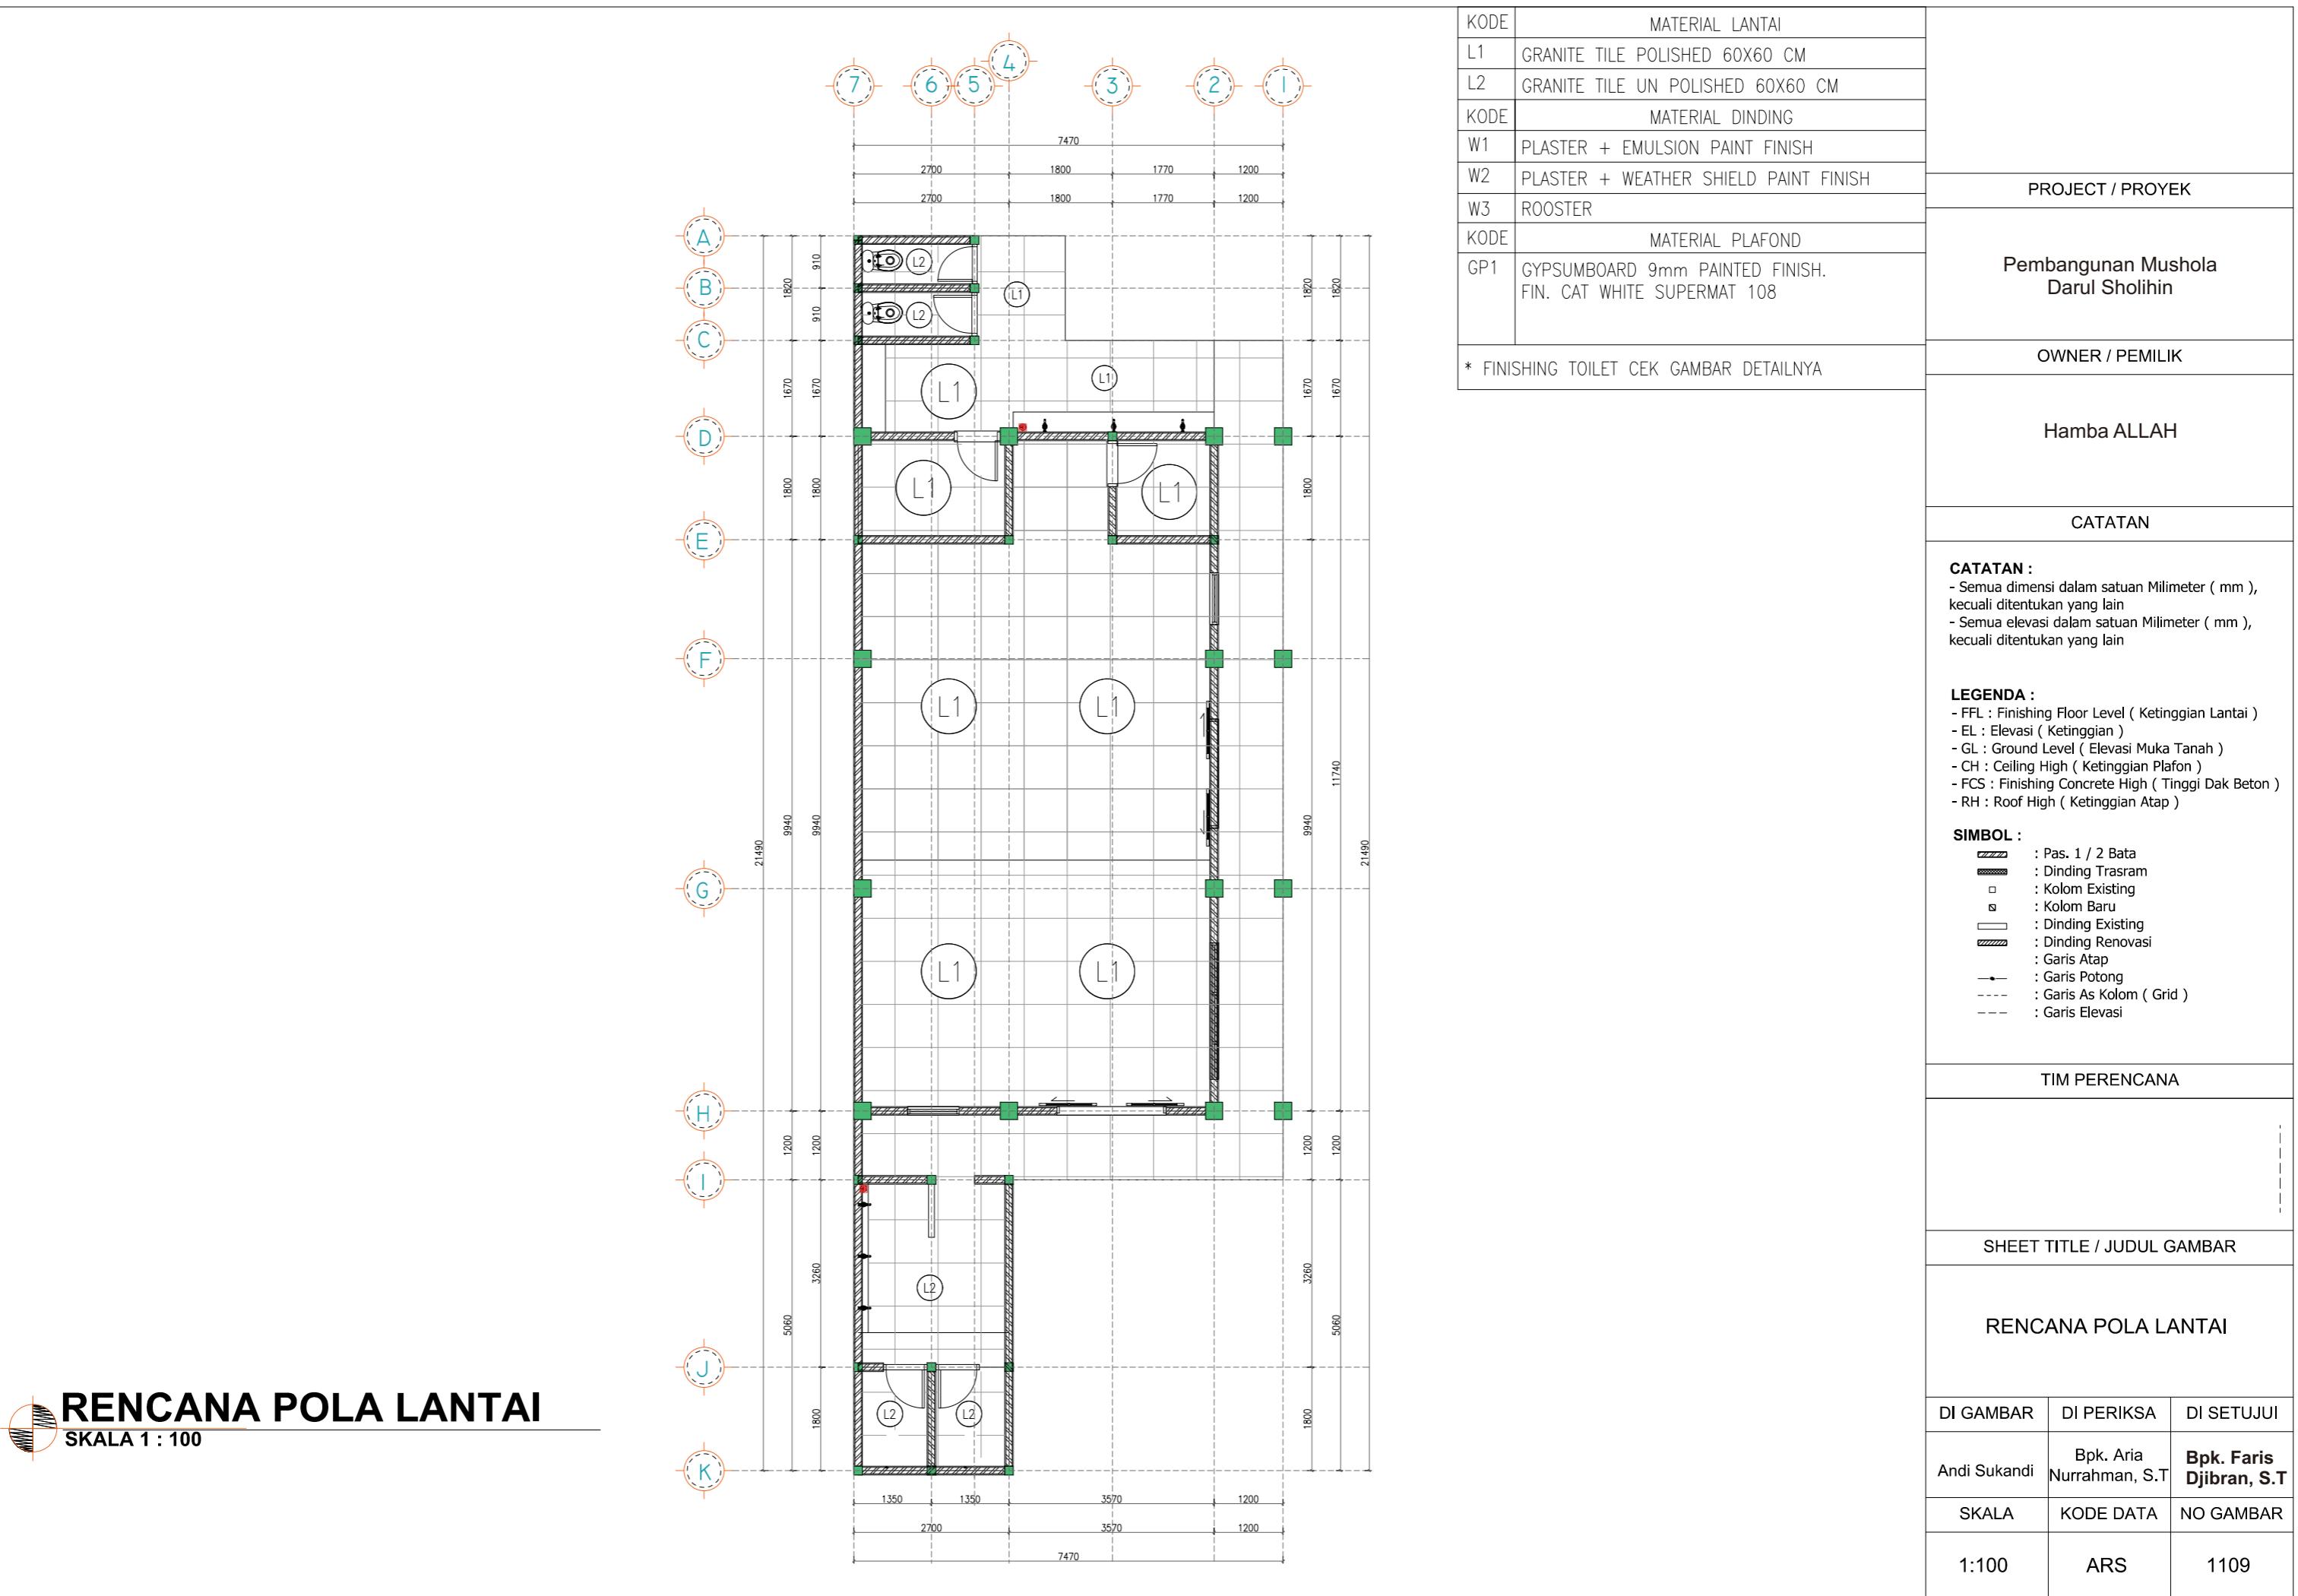

PROJECT / PROYEK

Pembangunan Mushola
Darul Sholihin

OWNER / PEMILIK

Hamba ALLAH

CATATAN

KODE	MATERIAL LANTAI
L1	GRANITE TILE POLISHED 60X60 CM
L2	GRANITE TILE UN POLISHED 60X60 CM
KODE	MATERIAL DINDING
W1	PLASTER + EMULSION PAINT FINISH
W2	PLASTER + WEATHER SHIELD PAINT FINISH
W3	ROOSTER
KODE	MATERIAL PLAFOND
GP1	GYPSUMBOARD 9mm PAINTED FINISH. FIN. CAT WHITE SUPERMAT 108


* FINISHING TOILET CEK GAMBAR DETAILNYA

TIM PERENCANA

SHEET TITLE / JUDUL GAMBAR


DETAIL LANTAI

DI GAMBAR	DI PERIKSA	DI SETUJUI
Andi Sukandi	Bpk. Aria Nurrahman, S.T	Bpk. Faris Djibrain, S.T
SKALA	KODE DATA	NO GAMBAR
1 : 25	ARS	1110

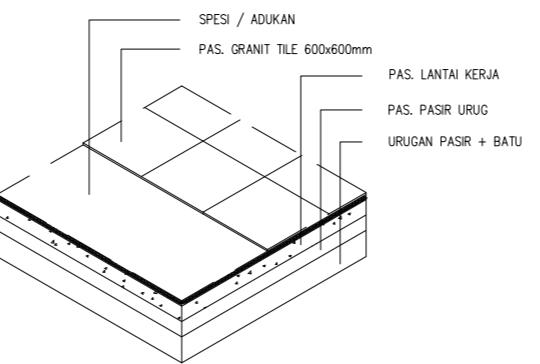

DET. ISOMETRI PAS. KERAMIK

SKALA 1 : 25

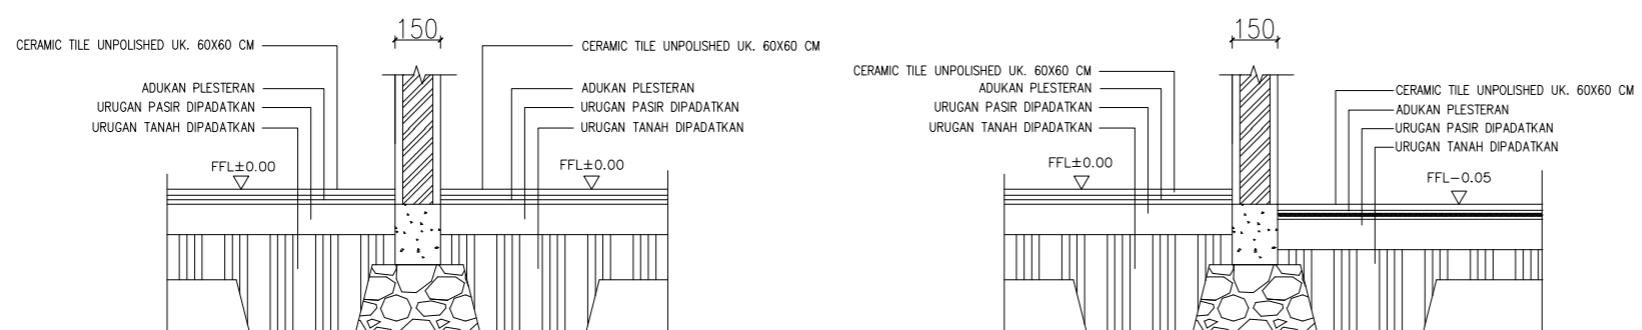


POT. A

SKALA 1 : 25

POT. B

SKALA 1 : 25

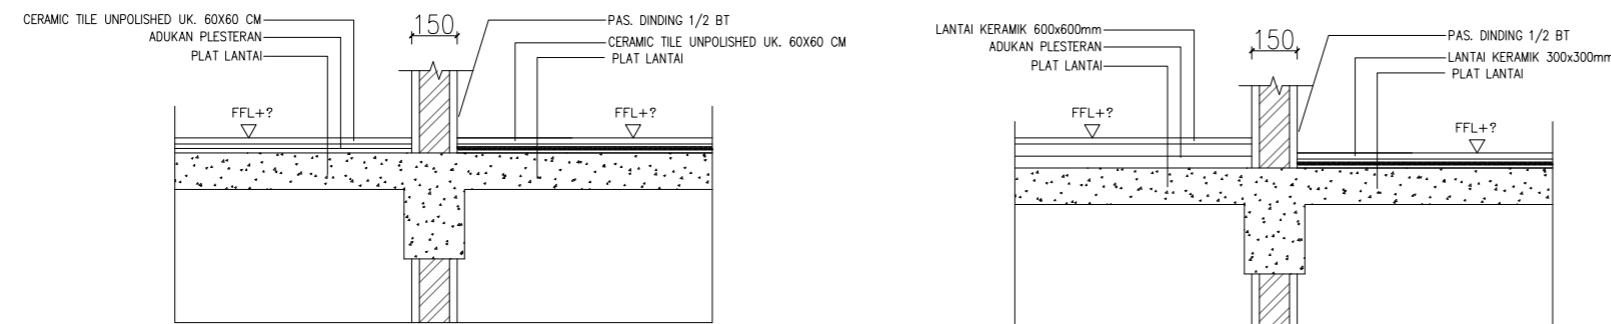

POT. E

SKALA 1 : 25


POT. D

SKALA 1 : 25



RENCANA DINDING

SKALA 1 : 100

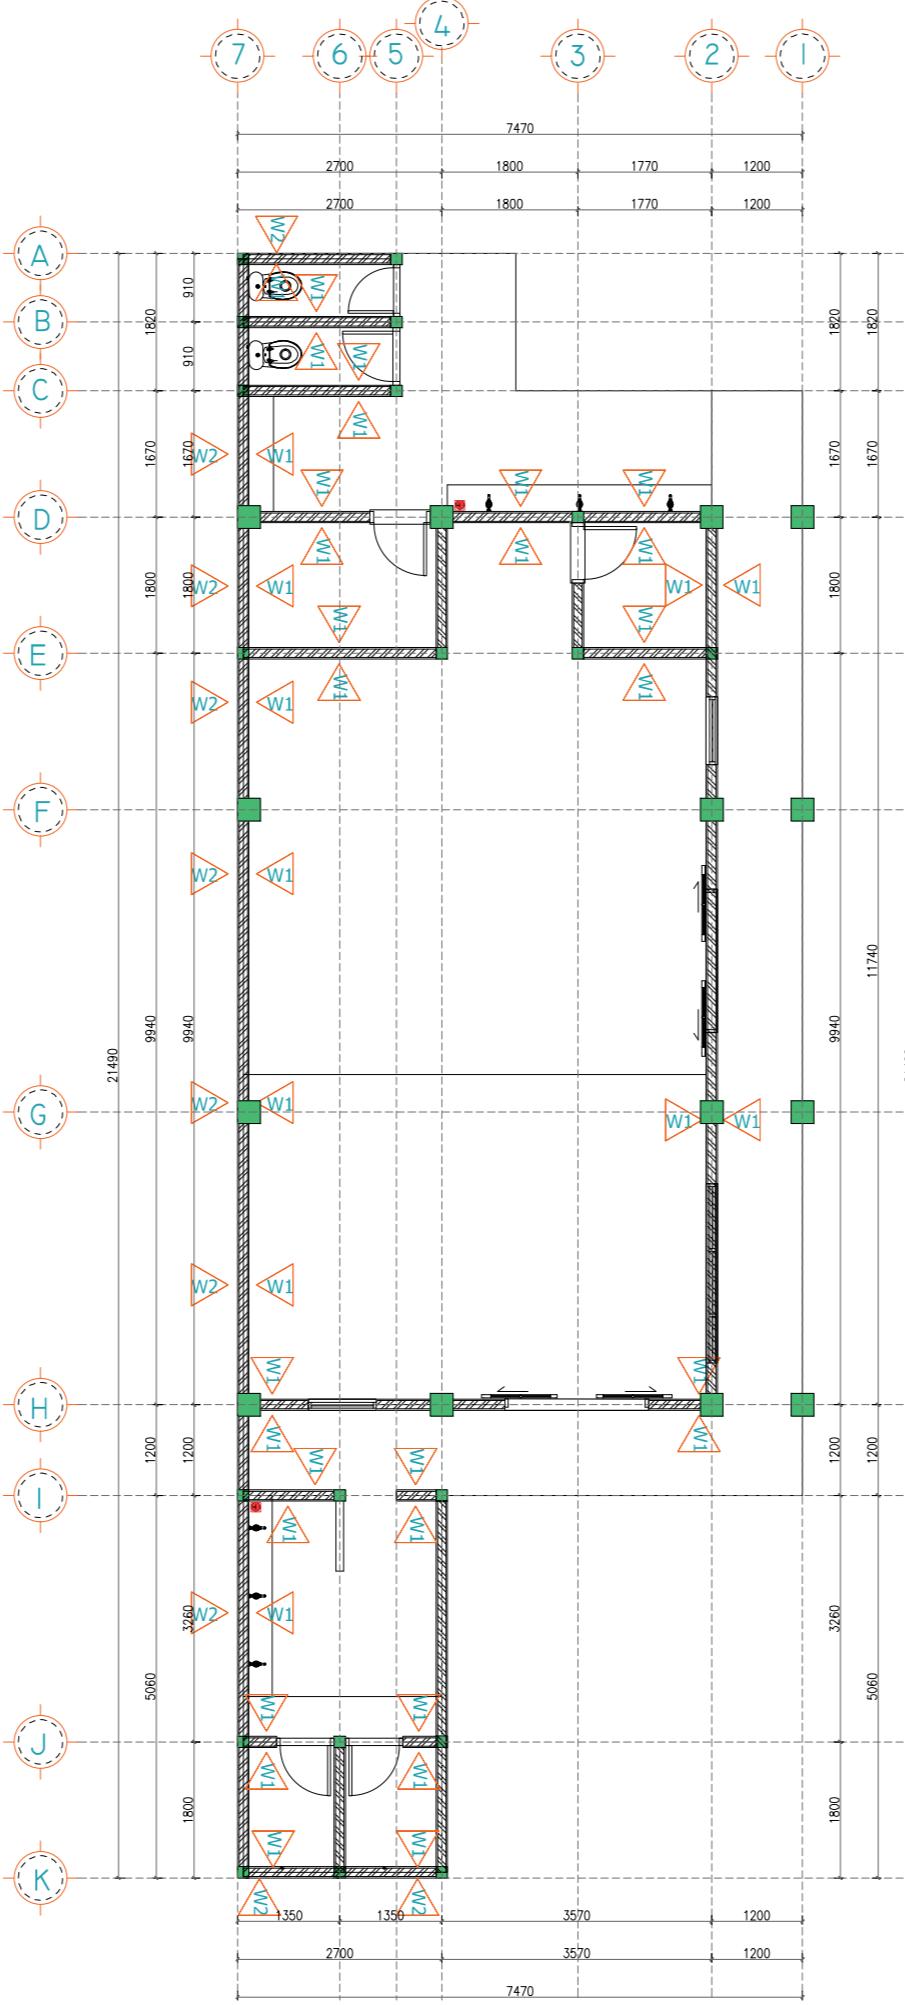

KODE	MATERIAL LANTAI	
L1	GRANITE TILE POLISHED 60X60 CM	
L2	GRANITE TILE UN POLISHED 60X60 CM	
KODE	MATERIAL DINDING	PROJECT / PROYEK
W1	PLASTER + EMULSION PAINT FINISH	
W2	PLASTER + WEATHER SHIELD PAINT FINISH	
W3	ROOSTER	Pembangunan Mushola Darul Sholihin
KODE	MATERIAL PLAFOND	
GP1	GYPSUMBOARD 9mm PAINTED FINISH. FIN. CAT WHITE SUPERMAT 108	
* FINISHING TOILET CEK GAMBAR DETAILNYA		OWNER / PEMILIK

* FINISHING TOILET CEK GAMBAR DETAILNYA

Pembangunan Mushola Darul Sholihin

OWNER / PEMILIK

Hamba ALLAH

CATATAN

CATATAN :

- Semua dimensi dalam satuan Milimeter (mm), kecuali ditentukan yang lain
- Semua elevasi dalam satuan Milimeter (mm), kecuali ditentukan yang lain

LEGENDA :

- FFL : Finishing Floor Level (Ketinggian Lantai)
- EL : Elevasi (Ketinggian)
- GL : Ground Level (Elevasi Muka Tanah)
- CH : Ceiling High (Ketinggian Plafon)
- FCS : Finishing Concrete High (Tinggi Dak Beton)
- RH : Roof High (Ketinggian Atap)


SIMBOL :	:
	: Pas. 1 / 2 Bata
	: Dinding Trasram
	: Kolom Existing
	: Kolom Baru
	: Dinding Existing
	: Dinding Renovasi
	: Garis Atap
	: Garis Potong
	: Garis As Kolom (Grid)
	: Garis Elevasi

TIM PERENCANA

SHEET TITLE / JUDUL GAMBAR

RENCANA DINDING





DI GAMBAR	DI PERIKSA	DI SETUJUI
Andi Sukandi	Bpk. Aria Nurrahman, S.T	Bpk. Faris Djibran, S.T
SKALA	KODE DATA	NO GAMBAR
1:100	ARS	1111

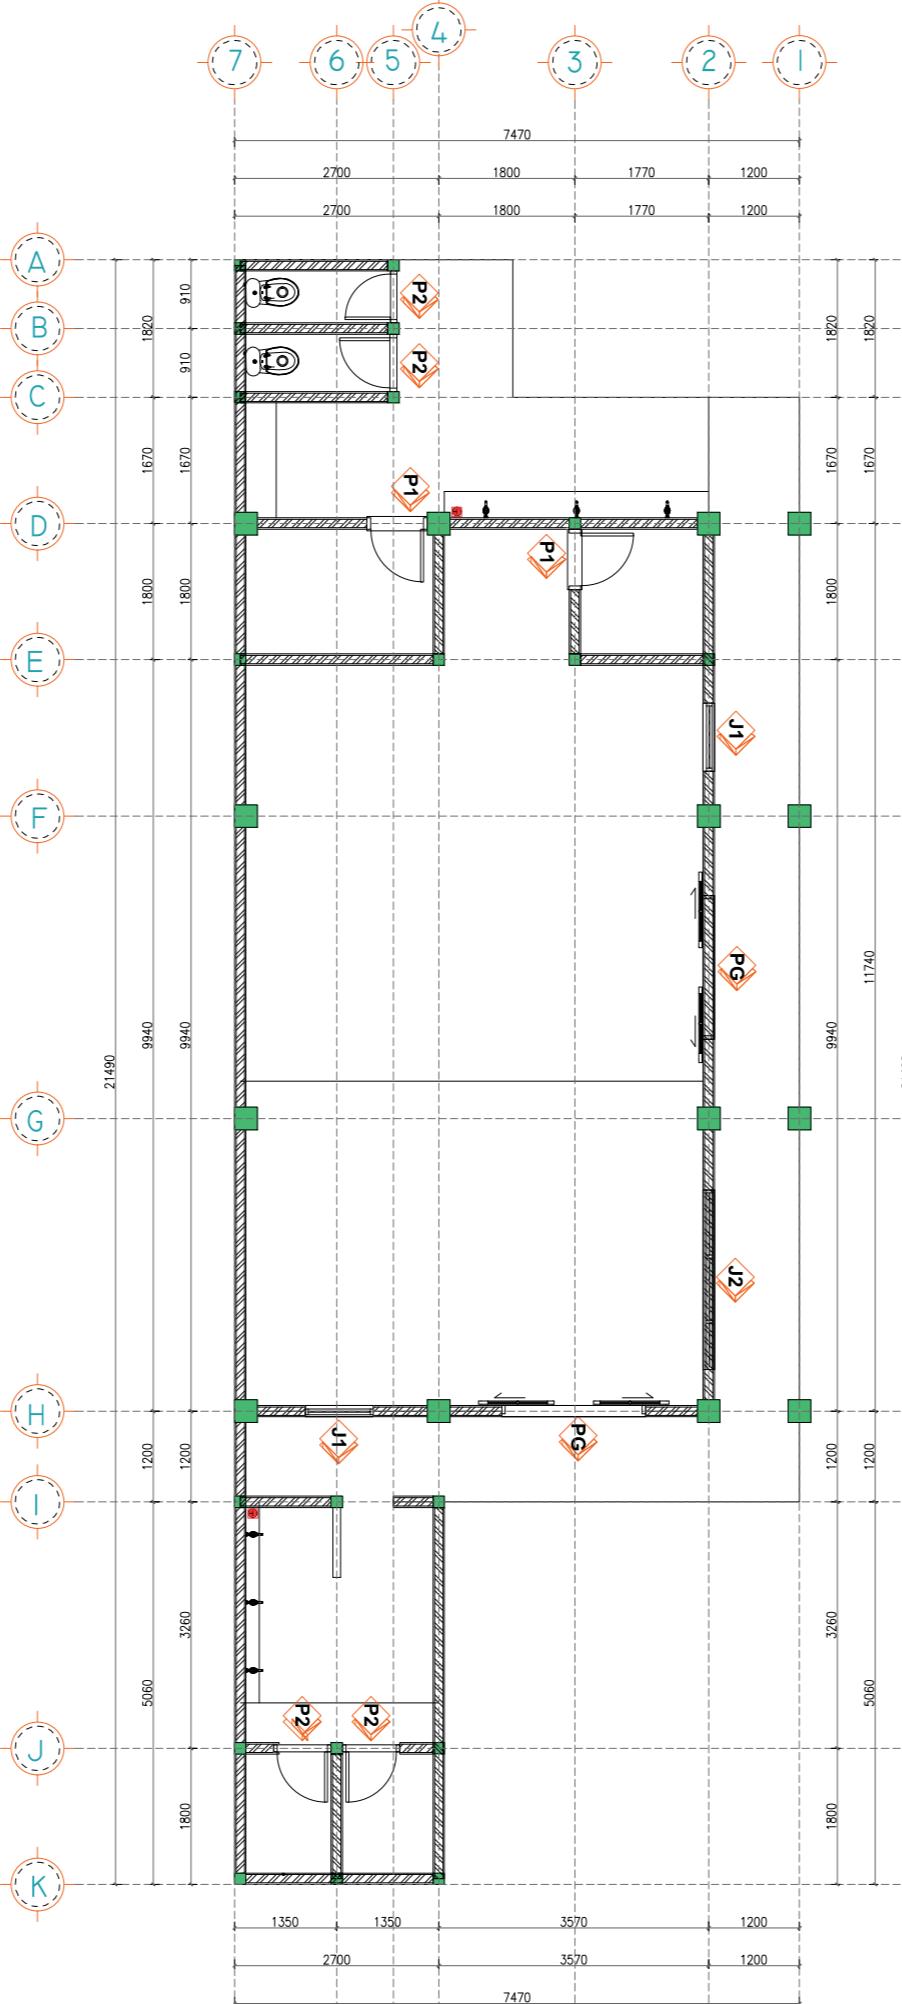

RENCANA KUSEN


SKALA 1 : 100

KODE	MATERIAL LANTAI	
L1	GRANITE TILE POLISHED 60X60 CM	
L2	GRANITE TILE UN POLISHED 60X60 CM	
KODE	MATERIAL DINDING	
W1	PLASTER + EMULSION PAINT FINISH	
W2	PLASTER + WEATHER SHIELD PAINT FINISH	
W3	ROOSTER	
KODE	MATERIAL PLAFOND	
GP1	GYPSUMBOARD 9mm PAINTED FINISH. FIN. CAT WHITE SUPERMAT 108	
PROJECT / PROYEK		Pembangunan Mushola Darul Sholihin
OWNER / PEMILIK		Hamba ALLAH
CATATAN		
CATATAN :		
- Semua dimensi dalam satuan Milimeter (mm), kecuali ditentukan yang lain		
- Semua elevasi dalam satuan Milimeter (mm), kecuali ditentukan yang lain		
LEGENDA :		
- FFL : Finishing Floor Level (Ketinggian Lantai)		
- EL : Elevasi (Ketinggian)		
- GL : Ground Level (Elevasi Muka Tanah)		
- CH : Ceiling High (Ketinggian Plafon)		
- FCS : Finishing Concrete High (Tinggi Dak Beton)		
- RH : Roof High (Ketinggian Atap)		
SIMBOL :		
: Pas. 1 / 2 Bata : Dinding Trasram : Kolom Existing : Kolom Baru : Dinding Existing : Dinding Renovasi : Garis Atap : Garis Potong : Garis As Kolom (Grid) : Garis Elevasi		
TIM PERENCANA		
SHEET TITLE / JUDUL GAMBAR		
RENCANA KUSEN		
DI GAMBAR	DI PERIKSA	DI SETUJUI
Andi Sukandi	Bpk. Aria Nurrahman, S.T	Bpk. Faris Djibrain, S.T
SKALA	KODE DATA	NO GAMBAR
1:100	ARS	1112

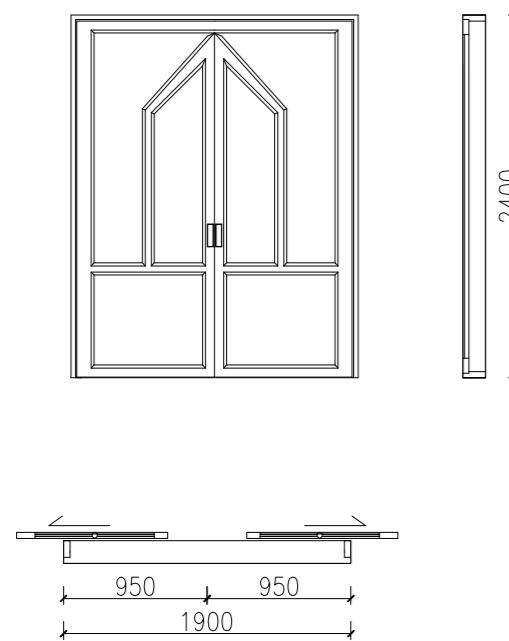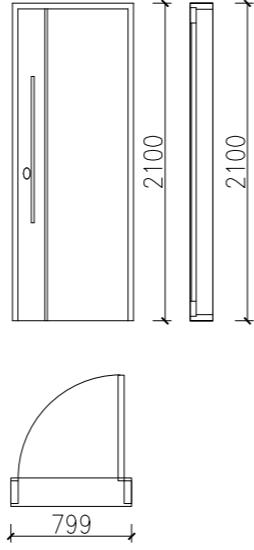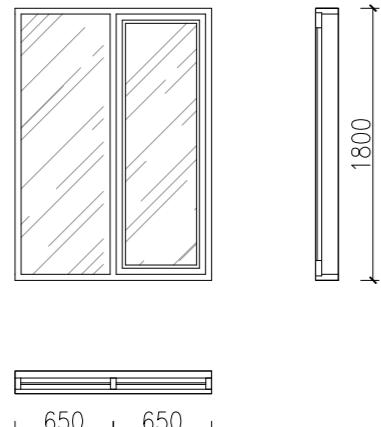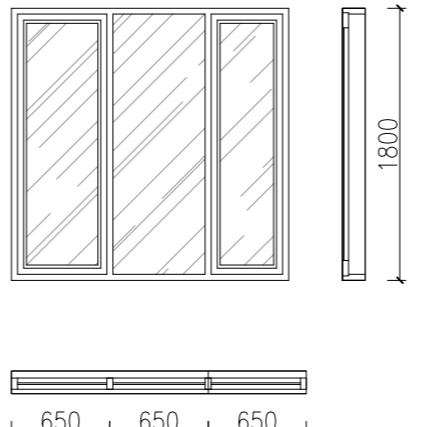
			PROJECT / PROYEK		
			Pembangunan Mushola Darul Sholihin		
			OWNER / PEMILIK		
			Hamba ALLAH		
			CATATAN		
 <p>JUMLAH KUSEN : 2 BUAH TYPE : PINTU GESER (PG) KUSEN : ALUMUNIUM 4"</p>			 <p>JUMLAH KUSEN : 2 BUAH TYPE : PINTU (P1) KUSEN : ALUMUNIUM 4"</p>		
 <p>JUMLAH KUSEN : 2 BUAH TYPE : JENDELA (J1) KUSEN : ALUMUNIUM 4"</p>			 <p>JUMLAH KUSEN : 13 BUAH TYPE : JENDELA (J2) KUSEN : ALUMUNIUM 4"</p>		
			TIM PERENCANA		
			SHEET TITLE / JUDUL GAMBAR		
			DETAIL KUSEN		
			DI GAMBAR	DI PERIKSA	DI SETUJUI
			Andi Sukandi	Bpk. Aria Nurrahman, S.T	Bpk. Faris Djibrain, S.T
			SKALA	KODE DATA	NO GAMBAR
			1:50	ARS	1113

RENCANA PLAFOND

SKALA 1 : 100

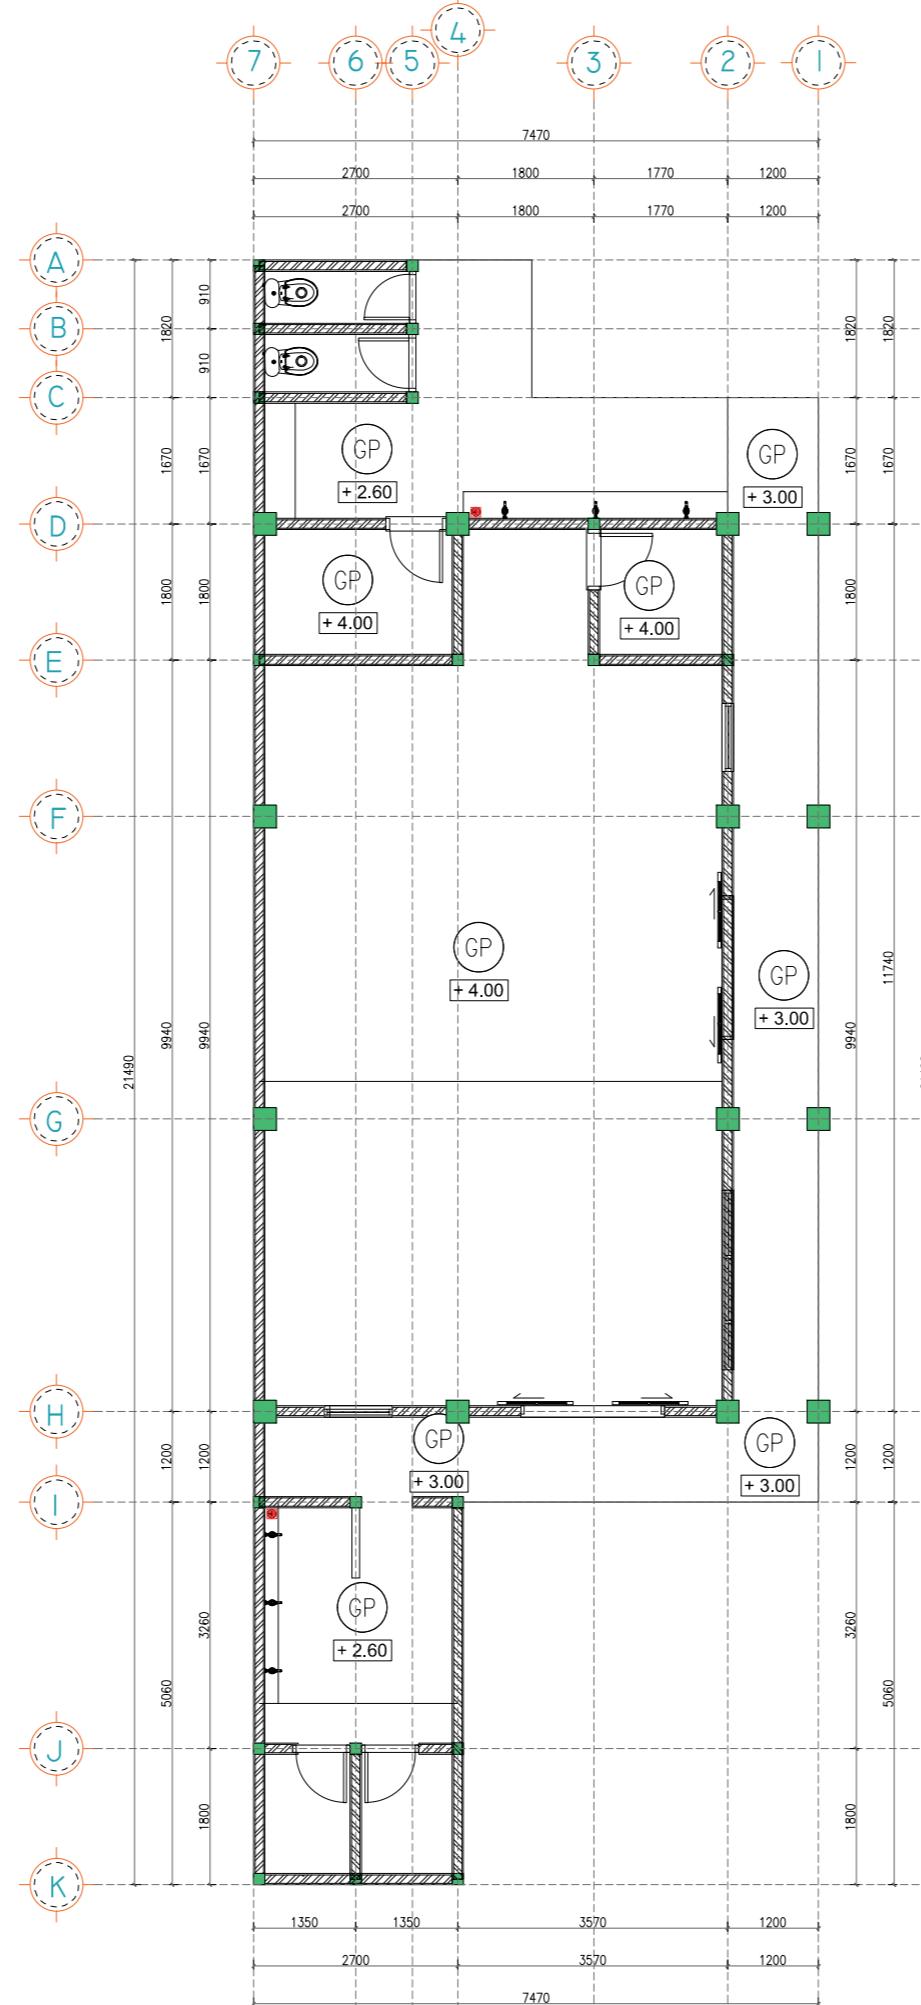

KODE	MATERIAL LANTAI																					
L1	GRANITE TILE POLISHED 60X60 CM																					
L2	GRANITE TILE UN POLISHED 60X60 CM																					
KODE	MATERIAL DINDING																					
W1	PLASTER + EMULSION PAINT FINISH																					
W2	PLASTER + WEATHER SHIELD PAINT FINISH																					
W3	ROOSTER																					
KODE	MATERIAL PLAFOND																					
GP1	GYPSUMBOARD 9mm PAINTED FINISH. FIN. CAT WHITE SUPERMAT 108																					
* FINISHING TOILET CEK GAMBAR DETAILNYA																						
PROJECT / PROYEK		Pembangunan Mushola Darul Sholihin																				
OWNER / PEMILIK		Hamba ALLAH																				
CATATAN																						
CATATAN :																						
<ul style="list-style-type: none"> - Semua dimensi dalam satuan Milimeter (mm), kecuali ditentukan yang lain - Semua elevasi dalam satuan Milimeter (mm), kecuali ditentukan yang lain 																						
LEGENDA :																						
<ul style="list-style-type: none"> - FFL : Finishing Floor Level (Ketinggian Lantai) - EL : Elevasi (Ketinggian) - GL : Ground Level (Elevasi Muka Tanah) - CH : Ceiling High (Ketinggian Plafon) - FCS : Finishing Concrete High (Tinggi Dak Beton) - RH : Roof High (Ketinggian Atap) 																						
SIMBOL :																						
<table> <tbody> <tr> <td>■</td><td>: Pas. 1 / 2 Bata</td></tr> <tr> <td>■■■</td><td>: Dinding Trasram</td></tr> <tr> <td>□</td><td>: Kolom Existing</td></tr> <tr> <td>▣</td><td>: Kolom Baru</td></tr> <tr> <td>■■</td><td>: Dinding Existing</td></tr> <tr> <td>■■■■</td><td>: Dinding Renovasi</td></tr> <tr> <td>○</td><td>: Garis Atap</td></tr> <tr> <td>—●—</td><td>: Garis Potong</td></tr> <tr> <td>——●—</td><td>: Garis As Kolom (Grid)</td></tr> <tr> <td>---●---</td><td>: Garis Elevasi</td></tr> </tbody> </table>			■	: Pas. 1 / 2 Bata	■■■	: Dinding Trasram	□	: Kolom Existing	▣	: Kolom Baru	■■	: Dinding Existing	■■■■	: Dinding Renovasi	○	: Garis Atap	—●—	: Garis Potong	——●—	: Garis As Kolom (Grid)	---●---	: Garis Elevasi
■	: Pas. 1 / 2 Bata																					
■■■	: Dinding Trasram																					
□	: Kolom Existing																					
▣	: Kolom Baru																					
■■	: Dinding Existing																					
■■■■	: Dinding Renovasi																					
○	: Garis Atap																					
—●—	: Garis Potong																					
——●—	: Garis As Kolom (Grid)																					
---●---	: Garis Elevasi																					
TIM PERENCANA																						
SHEET TITLE / JUDUL GAMBAR																						
RENCANA PLAFOND																						
DI GAMBAR	DI PERIKSA	DI SETUJUI																				
Andi Sukandi	Bpk. Aria Nurrahman, S.T	Bpk. Faris Djibrain, S.T																				
SKALA	KODE DATA	NO GAMBAR																				
1:100	ARS	1114																				

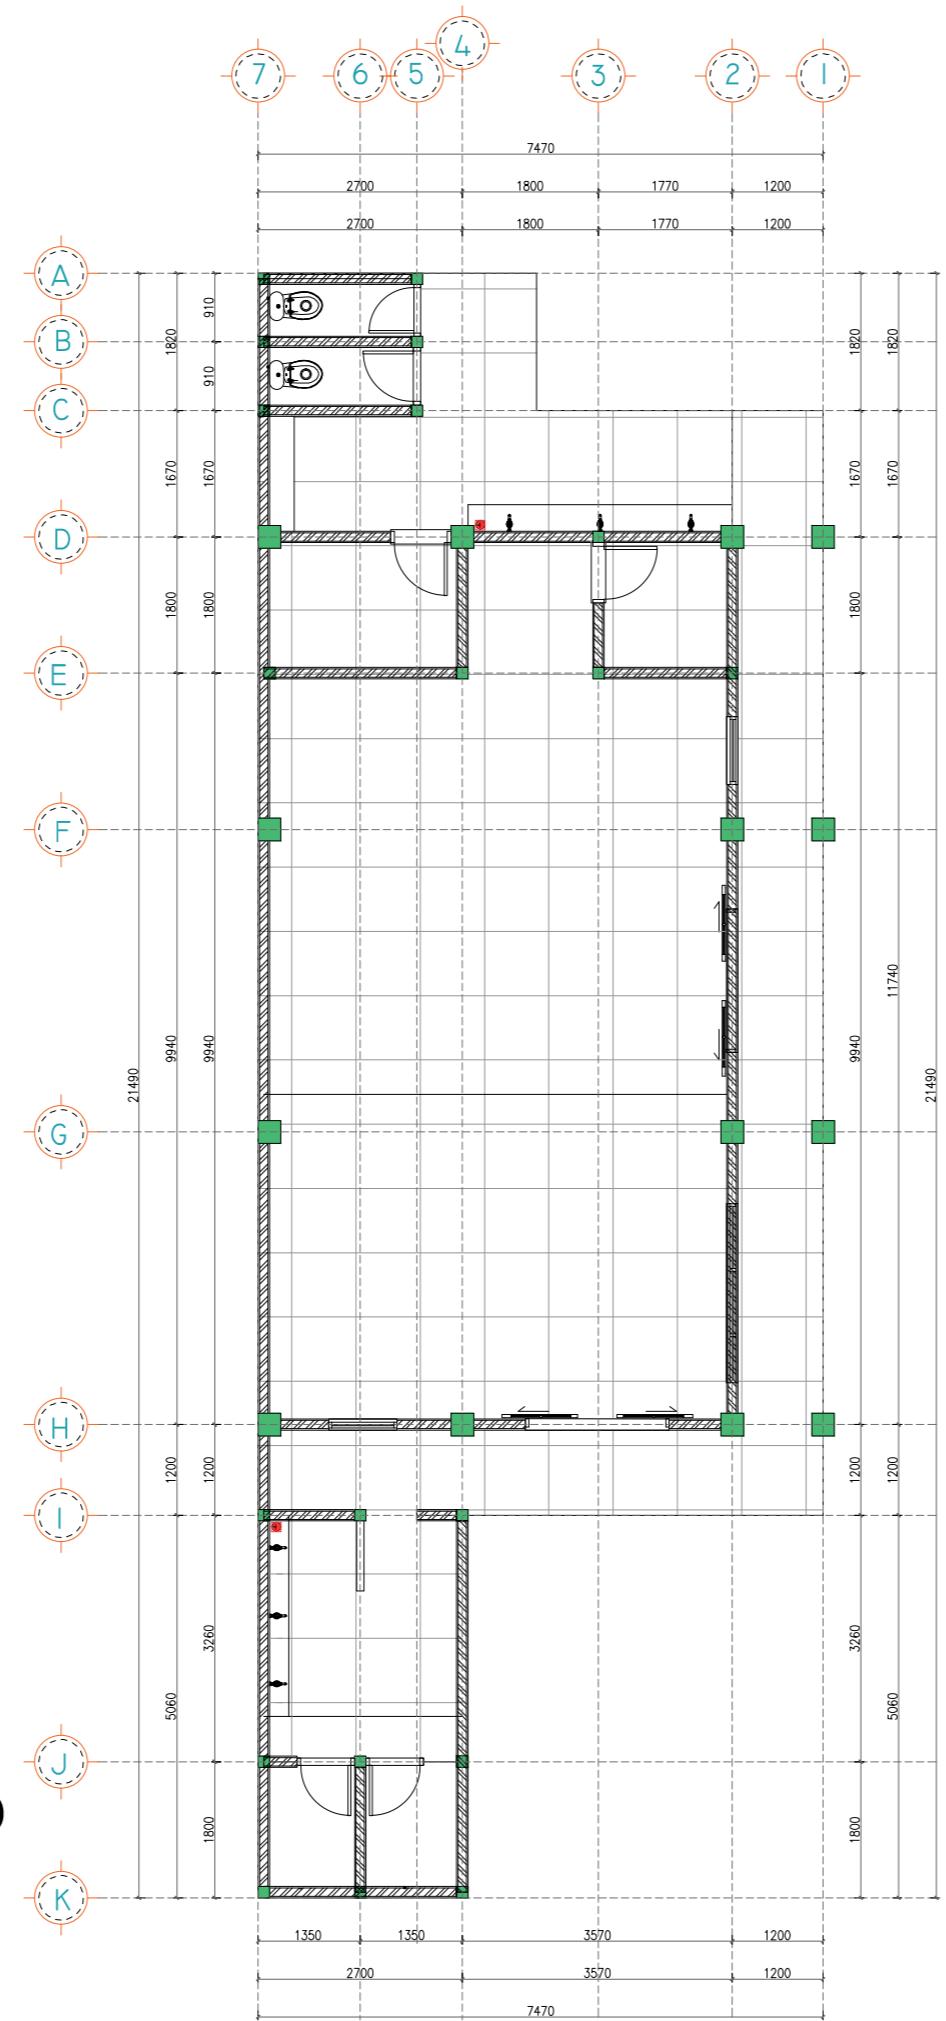

KODE	MATERIAL LANTAI																					
L1	GRANITE TILE POLISHED 60X60 CM																					
L2	GRANITE TILE UN POLISHED 60X60 CM																					
KODE	MATERIAL DINDING																					
W1	PLASTER + EMULSION PAINT FINISH																					
W2	PLASTER + WEATHER SHIELD PAINT FINISH																					
W3	ROOSTER																					
KODE	MATERIAL PLAFOND																					
GP1	GYPSUMBOARD 9mm PAINTED FINISH. FIN. CAT WHITE SUPERMAT 108																					
PROJECT / PROYEK		Pembangunan Mushola Darul Sholihin																				
OWNER / PEMILIK		Hamba ALLAH																				
CATATAN		CATATAN : <ul style="list-style-type: none"> - Semua dimensi dalam satuan Milimeter (mm), kecuali ditentukan yang lain - Semua elevasi dalam satuan Milimeter (mm), kecuali ditentukan yang lain 																				
LEGENDA :		<ul style="list-style-type: none"> - FFL : Finishing Floor Level (Ketinggian Lantai) - EL : Elevasi (Ketinggian) - GL : Ground Level (Elevasi Muka Tanah) - CH : Ceiling High (Ketinggian Plafon) - FCS : Finishing Concrete High (Tinggi Dak Beton) - RH : Roof High (Ketinggian Atap) 																				
SIMBOL :		<table> <tbody> <tr> <td>■</td><td>: Pas. 1 / 2 Bata</td></tr> <tr> <td>■</td><td>: Dinding Trasram</td></tr> <tr> <td>□</td><td>: Kolom Existing</td></tr> <tr> <td>▣</td><td>: Kolom Baru</td></tr> <tr> <td>■</td><td>: Dinding Existing</td></tr> <tr> <td>■</td><td>: Dinding Renovasi</td></tr> <tr> <td>—</td><td>: Garis Atap</td></tr> <tr> <td>—</td><td>: Garis Potong</td></tr> <tr> <td>---</td><td>: Garis As Kolom (Grid)</td></tr> <tr> <td>---</td><td>: Garis Elevasi</td></tr> </tbody> </table>	■	: Pas. 1 / 2 Bata	■	: Dinding Trasram	□	: Kolom Existing	▣	: Kolom Baru	■	: Dinding Existing	■	: Dinding Renovasi	—	: Garis Atap	—	: Garis Potong	---	: Garis As Kolom (Grid)	---	: Garis Elevasi
■	: Pas. 1 / 2 Bata																					
■	: Dinding Trasram																					
□	: Kolom Existing																					
▣	: Kolom Baru																					
■	: Dinding Existing																					
■	: Dinding Renovasi																					
—	: Garis Atap																					
—	: Garis Potong																					
---	: Garis As Kolom (Grid)																					
---	: Garis Elevasi																					
TIM PERENCANA																						
SHEET TITLE / JUDUL GAMBAR																						
RENCANA RANGKA PLAFOND																						
DI GAMBAR	DI PERIKSA	DI SETUJUI																				
Andi Sukandi	Bpk. Aria Nurrahman, S.T	Bpk. Faris Djibrain, S.T																				
SKALA	KODE DATA	NO GAMBAR																				
1:100	ARS	1115																				

PROJECT / PROYEK

Pembangunan Mushola
Darul Sholihin

OWNER / PEMILIK

Hamba ALLAH
WILLI PRAJAKAS

CATATAN


KODE	MATERIAL LANTAI
L1	GRANITE TILE POLISHED 60X60 CM
L2	GRANITE TILE UN POLISHED 60X60 CM
KODE	MATERIAL DINDING
W1	PLASTER + EMULSION PAINT FINISH
W2	PLASTER + WEATHER SHIELD PAINT FINISH
W3	ROOSTER
KODE	MATERIAL PLAFOND
GP1	GYPSUMBOARD 9mm PAINTED FINISH. FIN. CAT WHITE SUPERMAT 108

* FINISHING TOILET CEK GAMBAR DETAILNYA

TIM PERENCANA

SHEET TITLE / JUDUL GAMBAR


DETAIL PLAFOND

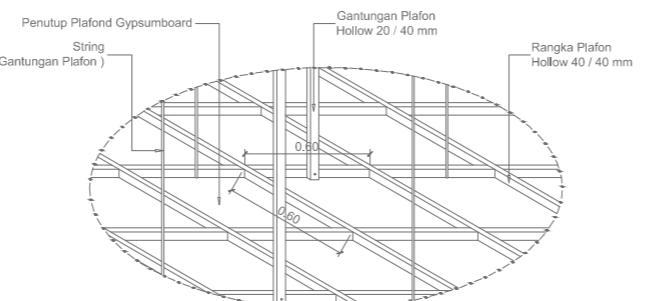



 **DETAIL PLAFOND**
SKALA 1 : 25

DI GAMBAR	DI PERIKSA	DI SETUJUI
Andi Sukandi	Bpk. Aria Nurrahman, S.T	Bpk. Faris Djibrain, S.T
SKALA	KODE DATA	NO GAMBAR
1 : 25	ARS	1116


RANGKA HOLLOW MODUL 60 X 60

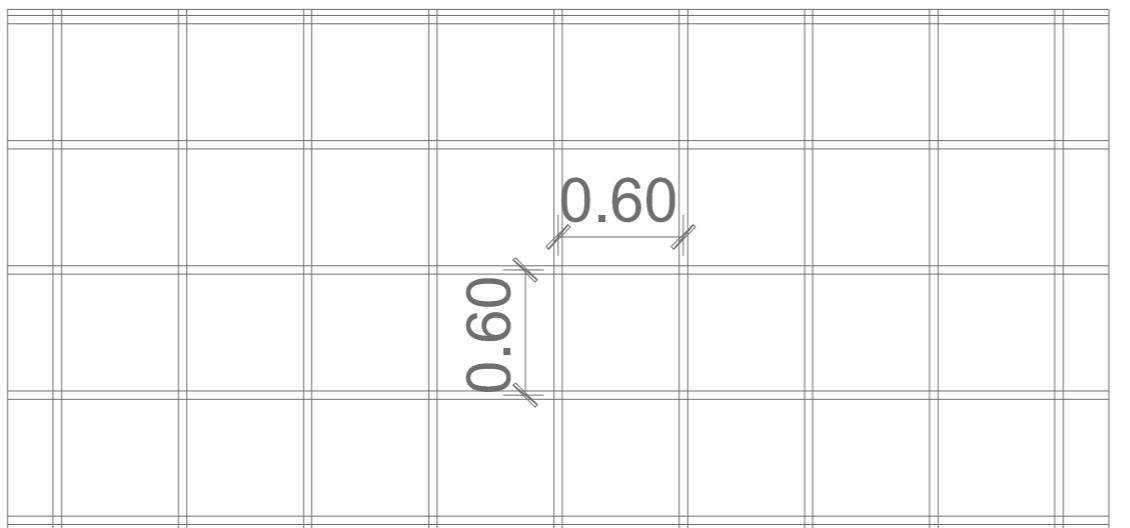

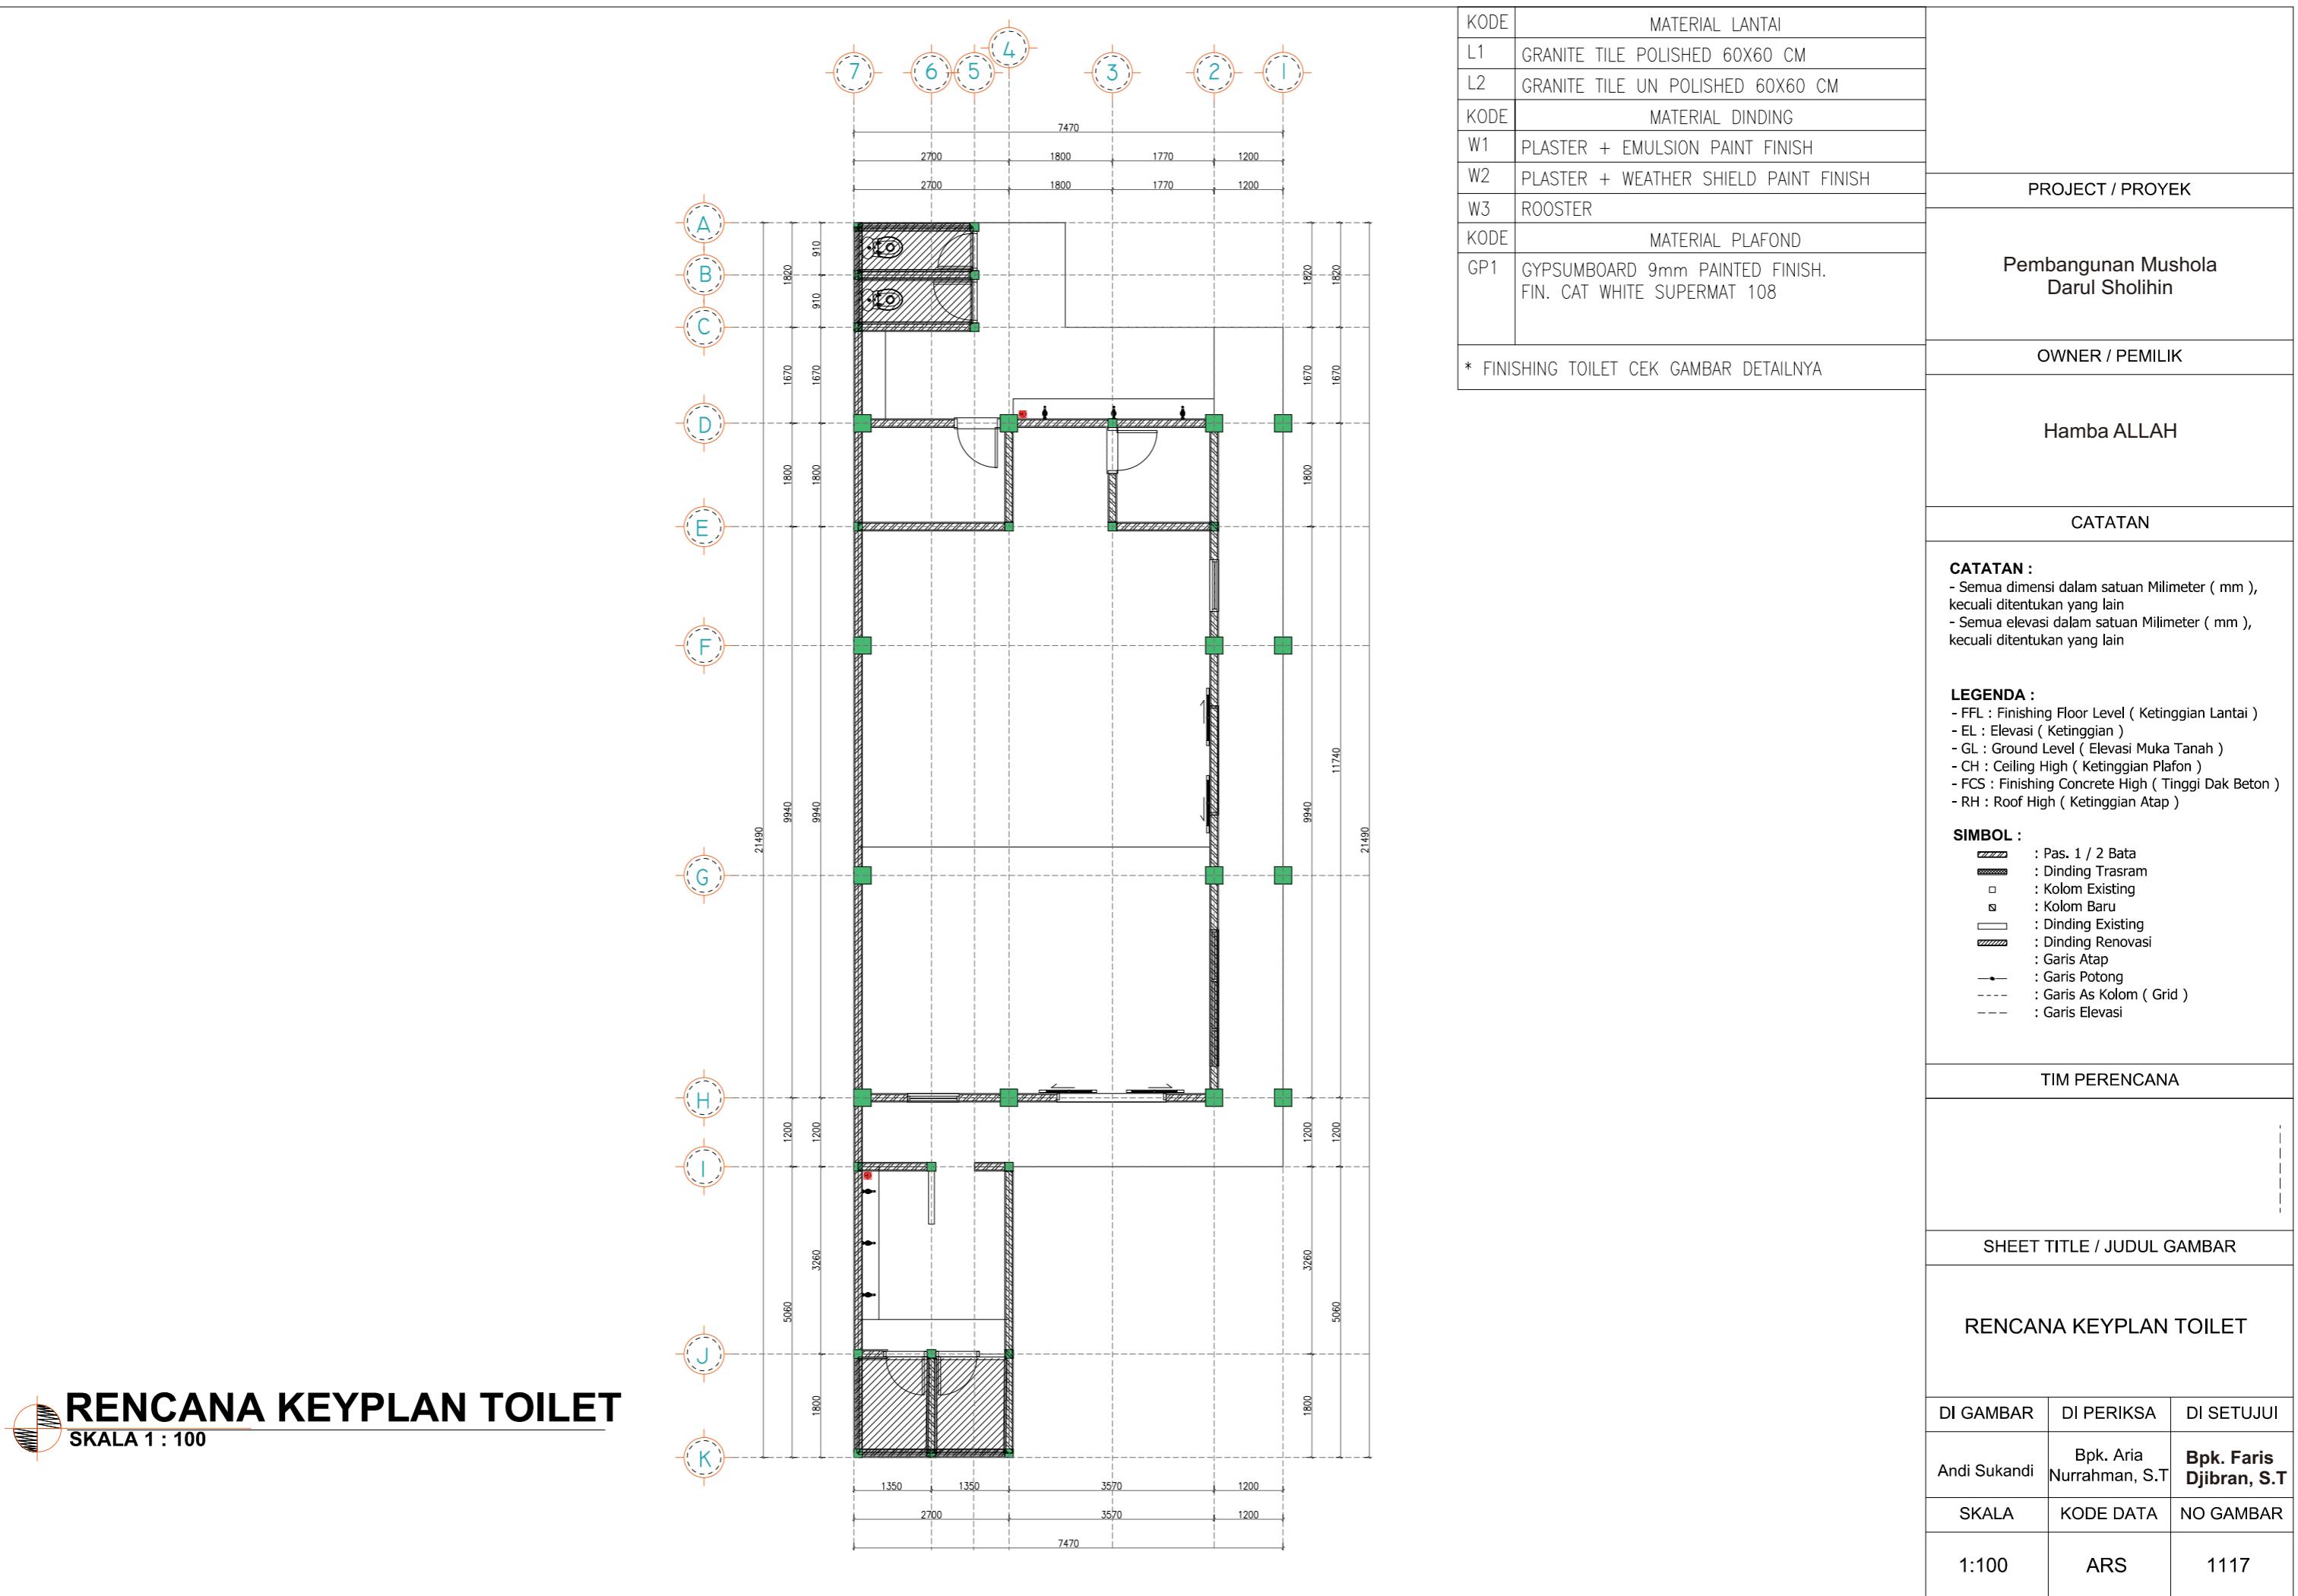


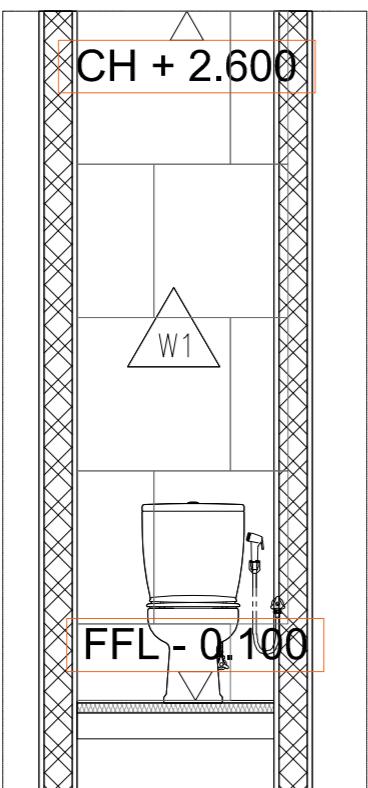

POTONGAN A-A
SKALA 1 : 30

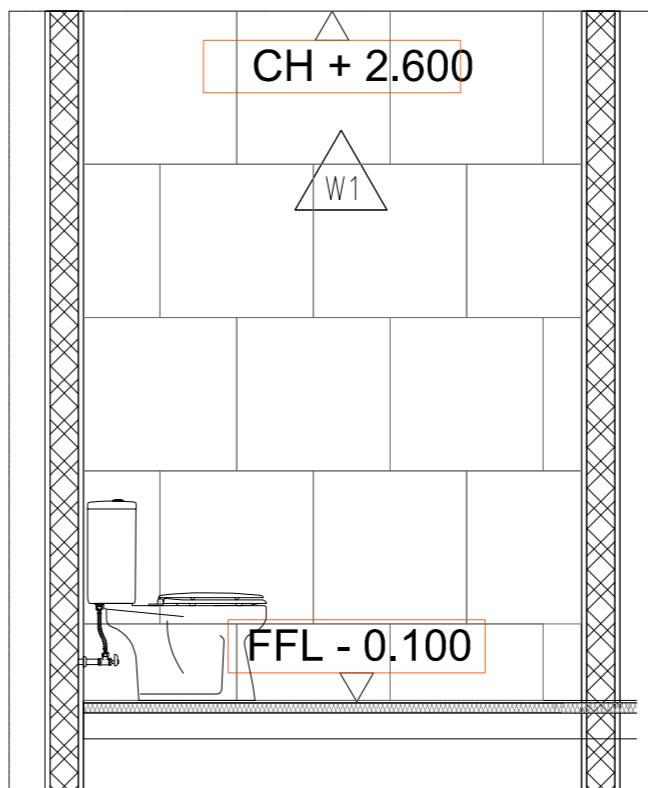

POTONGAN B-B
SKALA 1 : 30

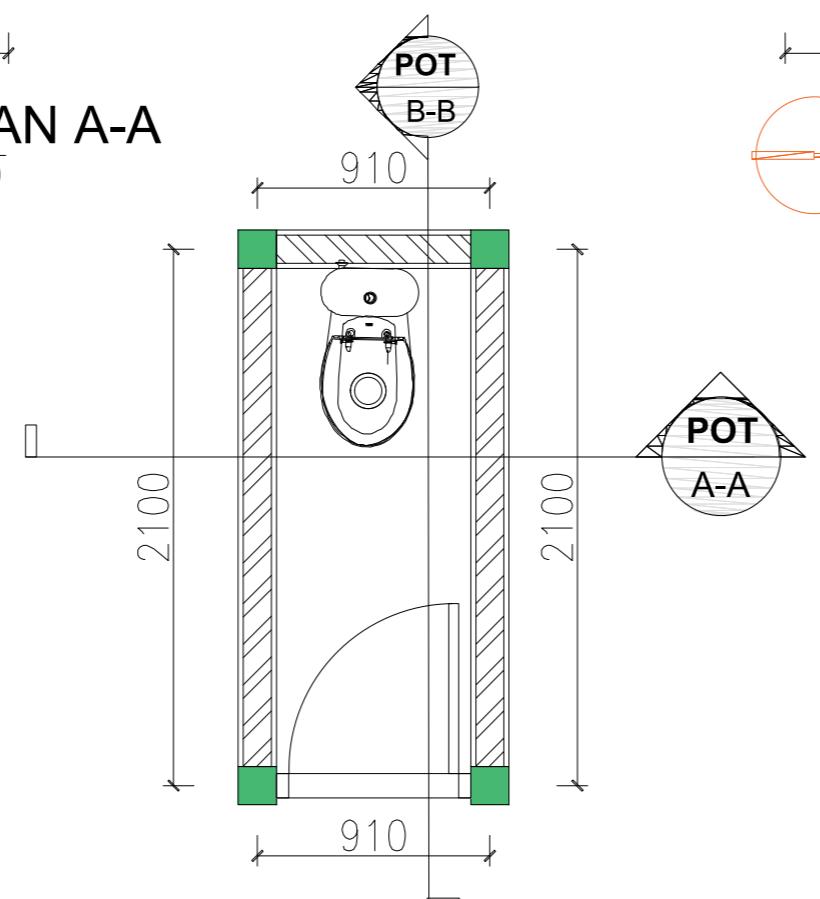

WC/KM 1
SKALA 1 : 30

PROJECT / PROYEK

Pembangunan Mushola
Darul Sholihin

OWNER / PEMILIK

Wl Hamba ALLAH KAS

CATATAN

KODE	MATERIAL LANTAI
L1	GRANITE TILE POLISHED 60X60 CM
L2	GRANITE TILE UN POLISHED 60X60 CM
KODE	MATERIAL DINDING
W1	PLASTER + EMULSION PAINT FINISH
W2	PLASTER + WEATHER SHIELD PAINT FINISH
W3	ROOSTER
KODE	MATERIAL PLAFOND
GP1	GYPSUMBOARD 9mm PAINTED FINISH. FIN. CAT WHITE SUPERMAT 108


* FINISHING TOILET CEK GAMBAR DETAILNYA

TIM PERENCANA


SHEET TITLE / JUDUL GAMBAR

DETAIL TOILET


DI GAMBAR	DI PERIKSA	DI SETUJUI
Andi Sukandi	Bpk. Aria Nurrahman, S.T	Bpk. Faris Djibran, S.T
SKALA	KODE DATA	NO GAMBAR
1:30	ARS	1118

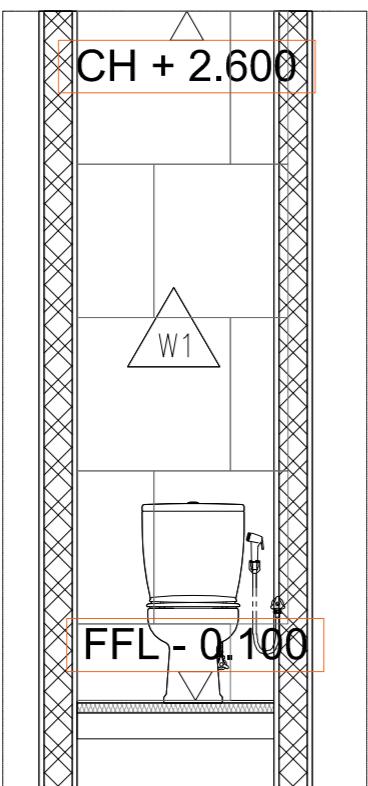

POTONGAN A-A
SKALA 1 : 30

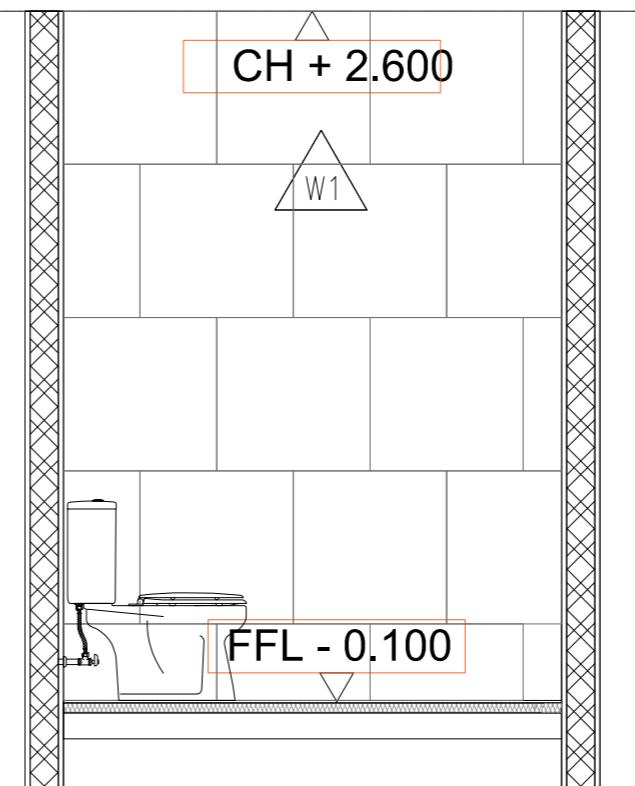

POTONGAN B-B
SKALA 1 : 30

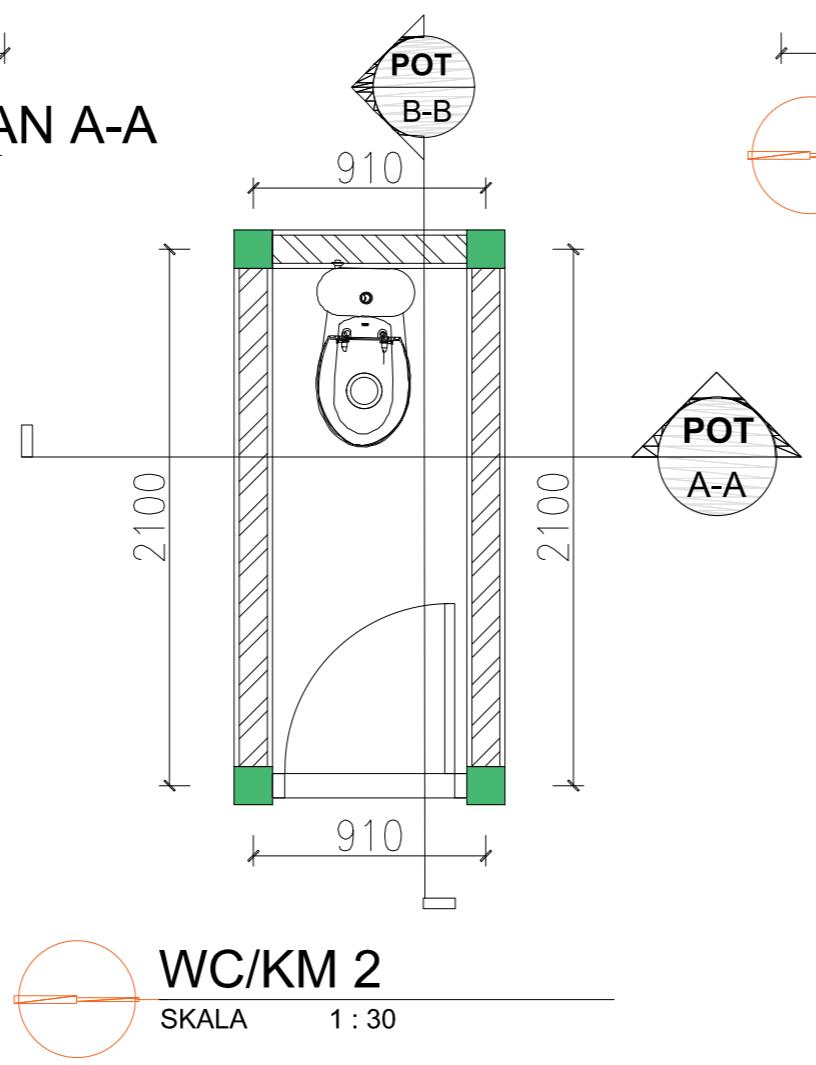

WC/KM 2
SKALA 1 : 30

PROJECT / PROYEK

Pembangunan Mushola
Darul Sholihin

OWNER / PEMILIK

Wl Hamba ALLAH KAS

CATATAN

KODE	MATERIAL LANTAI
L1	GRANITE TILE POLISHED 60X60 CM
L2	GRANITE TILE UN POLISHED 60X60 CM
KODE	MATERIAL DINDING
W1	PLASTER + EMULSION PAINT FINISH
W2	PLASTER + WEATHER SHIELD PAINT FINISH
W3	ROOSTER
KODE	MATERIAL PLAFOND
GP1	GYPSUMBOARD 9mm PAINTED FINISH. FIN. CAT WHITE SUPERMAT 108


* FINISHING TOILET CEK GAMBAR DETAILNYA

TIM PERENCANA


SHEET TITLE / JUDUL GAMBAR

DETAIL TOILET


DI GAMBAR	DI PERIKSA	DI SETUJUI
Andi Sukandi	Bpk. Aria Nurrahman, S.T	Bpk. Faris Djibrain, S.T
SKALA	KODE DATA	NO GAMBAR
1:30	ARS	1119

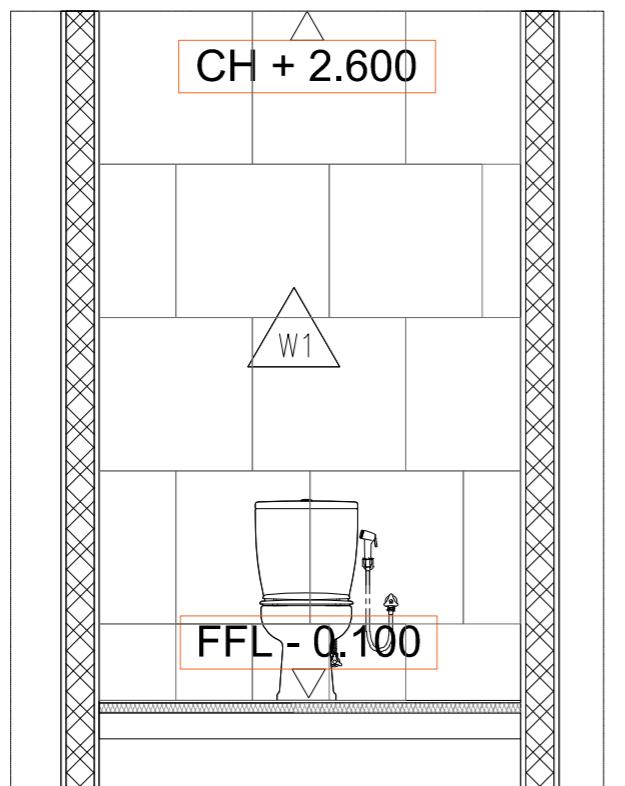

POTONGAN A-A
SKALA 1 : 30

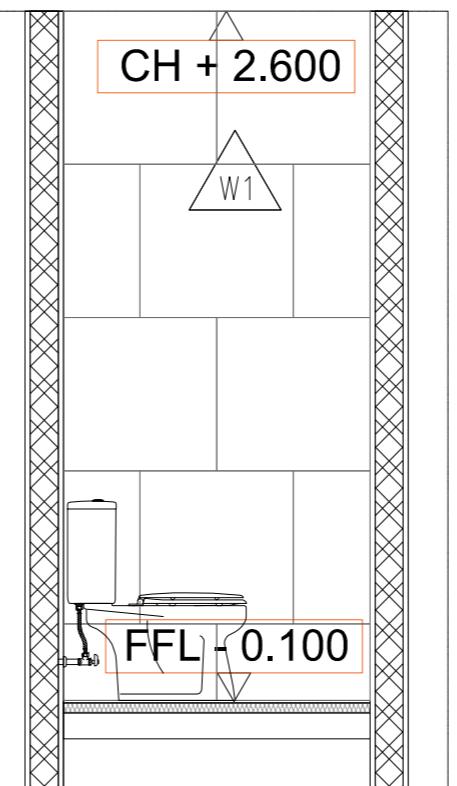

POTONGAN B-B
SKALA 1 : 30

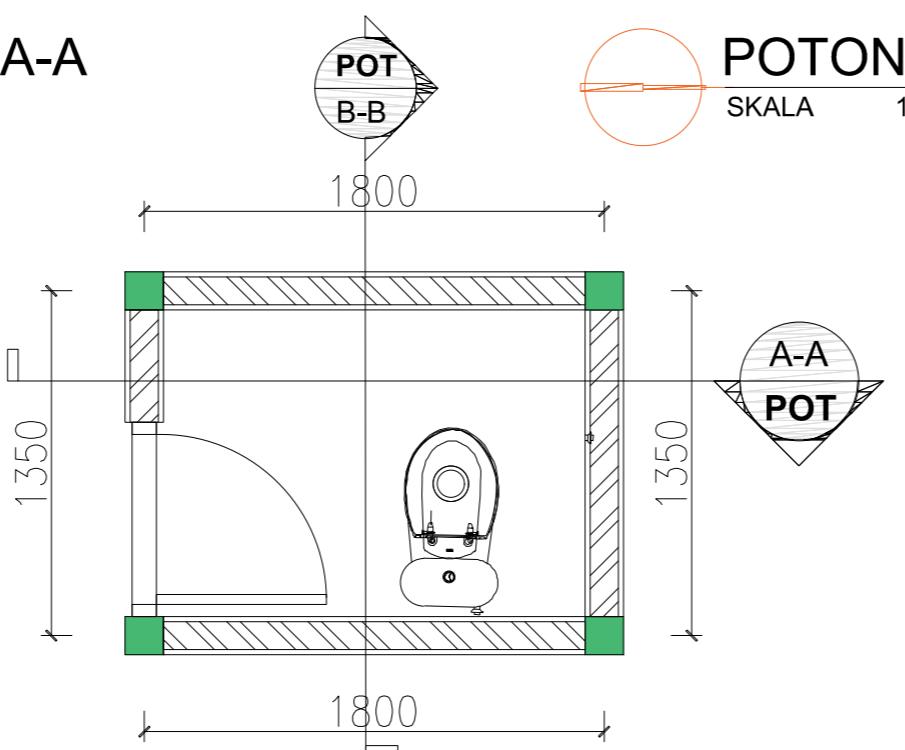

WC/KM 3
SKALA 1 : 30

PROJECT / PROYEK

Pembangunan Mushola
Darul Sholihin

OWNER / PEMILIK

Wl Hamba ALLAH KAS

CATATAN

KODE	MATERIAL LANTAI
L1	GRANITE TILE POLISHED 60X60 CM
L2	GRANITE TILE UN POLISHED 60X60 CM
KODE	MATERIAL DINDING
W1	PLASTER + EMULSION PAINT FINISH
W2	PLASTER + WEATHER SHIELD PAINT FINISH
W3	ROOSTER
KODE	MATERIAL PLAFOND
GP1	GYPSUMBOARD 9mm PAINTED FINISH. FIN. CAT WHITE SUPERMAT 108


* FINISHING TOILET CEK GAMBAR DETAILNYA

TIM PERENCANA


SHEET TITLE / JUDUL GAMBAR

DETAIL TOILET


DI GAMBAR	DI PERIKSA	DI SETUJUI
Andi Sukandi	Bpk. Aria Nurrahman, S.T	Bpk. Faris Djibrain, S.T
SKALA	KODE DATA	NO GAMBAR
1:30	ARS	1121

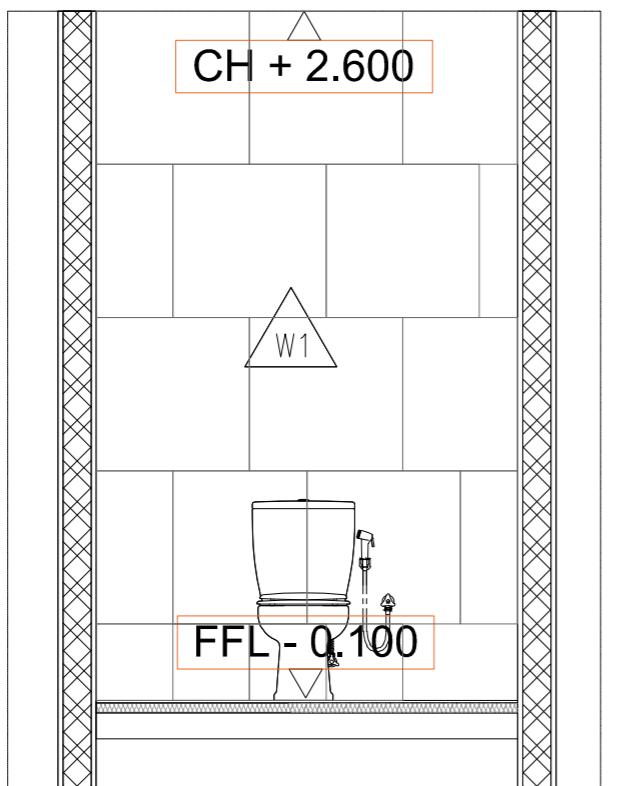

POTONGAN A-A
SKALA 1 : 30

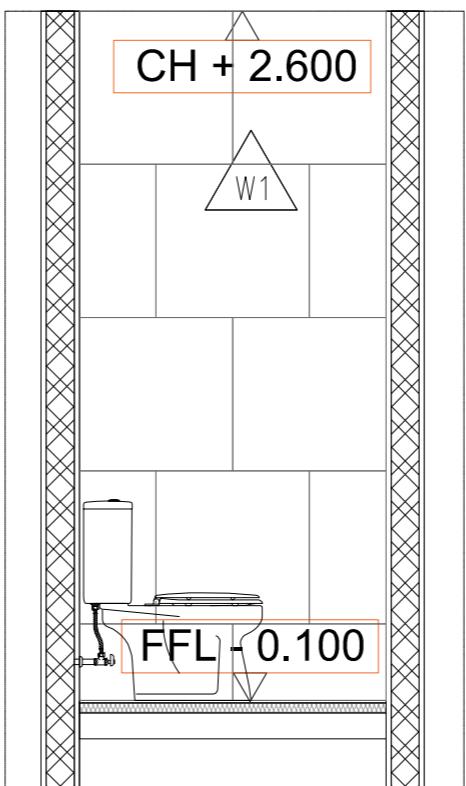

POTONGAN B-B
SKALA 1 : 30

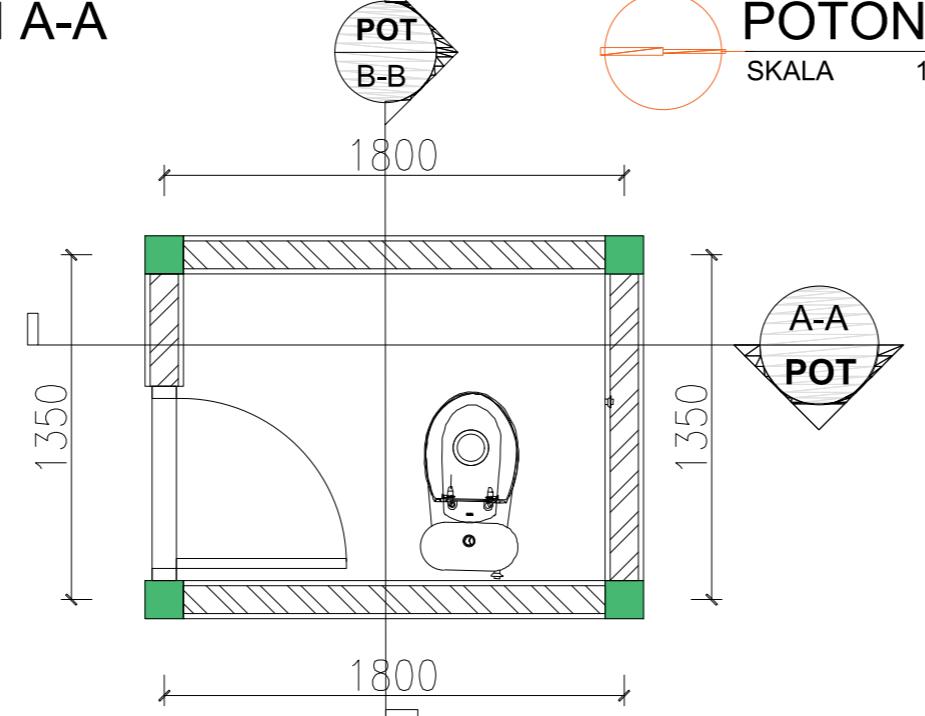

WC/KM 4
SKALA 1 : 30

PROJECT / PROYEK

Pembangunan Mushola
Darul Sholihin

OWNER / PEMILIK

Wl Hamba ALLAH KAS

CATATAN

KODE	MATERIAL LANTAI
L1	GRANITE TILE POLISHED 60X60 CM
L2	GRANITE TILE UN POLISHED 60X60 CM
KODE	MATERIAL DINDING
W1	PLASTER + EMULSION PAINT FINISH
W2	PLASTER + WEATHER SHIELD PAINT FINISH
W3	ROOSTER
KODE	MATERIAL PLAFOND
GP1	GYPSUMBOARD 9mm PAINTED FINISH. FIN. CAT WHITE SUPERMAT 108

* FINISHING TOILET CEK GAMBAR DETAILNYA

TIM PERENCANA

SHEET TITLE / JUDUL GAMBAR

DETAIL TOILET

DI GAMBAR	DI PERIKSA	DI SETUJUI
Andi Sukandi	Bpk. Aria Nurrahman, S.T	Bpk. Faris Djibrain, S.T
SKALA	KODE DATA	NO GAMBAR
1:30	ARS	1121


MEKANIKAL E. P
PERENCANAAN PEMBANGUNAN

*MUSHOLA
DARUL SHOLIHIN*

DAFTAR GAMBAR PERENCANAAN PEMBANGUNAN

DAFTAR ISI GAMBAR MEKANIKAL E. P


NO GAMBAR	JUDUL GAMBAR	HAL - GAMBAR
MEKANIKAL E. P		
01. DENAH INST. ELEKTRIKAL		
MEP	INSTALASI LISTRIK	2101
02. DENAH INST. AIR BERSIH		
MEP	INSTALASI AIR BERSIH	2102
03. DENAH AIR KOTOR		
MEP	INSTALASI AIR BEKAS	2103
MEP	INSTALASI AIR KOTOR	2104
03. DENAH PLUMBING		
MEP	DETAIL SEPTICTANK 1	2105
MEP	DETAIL SEPTICTANK 2	2106

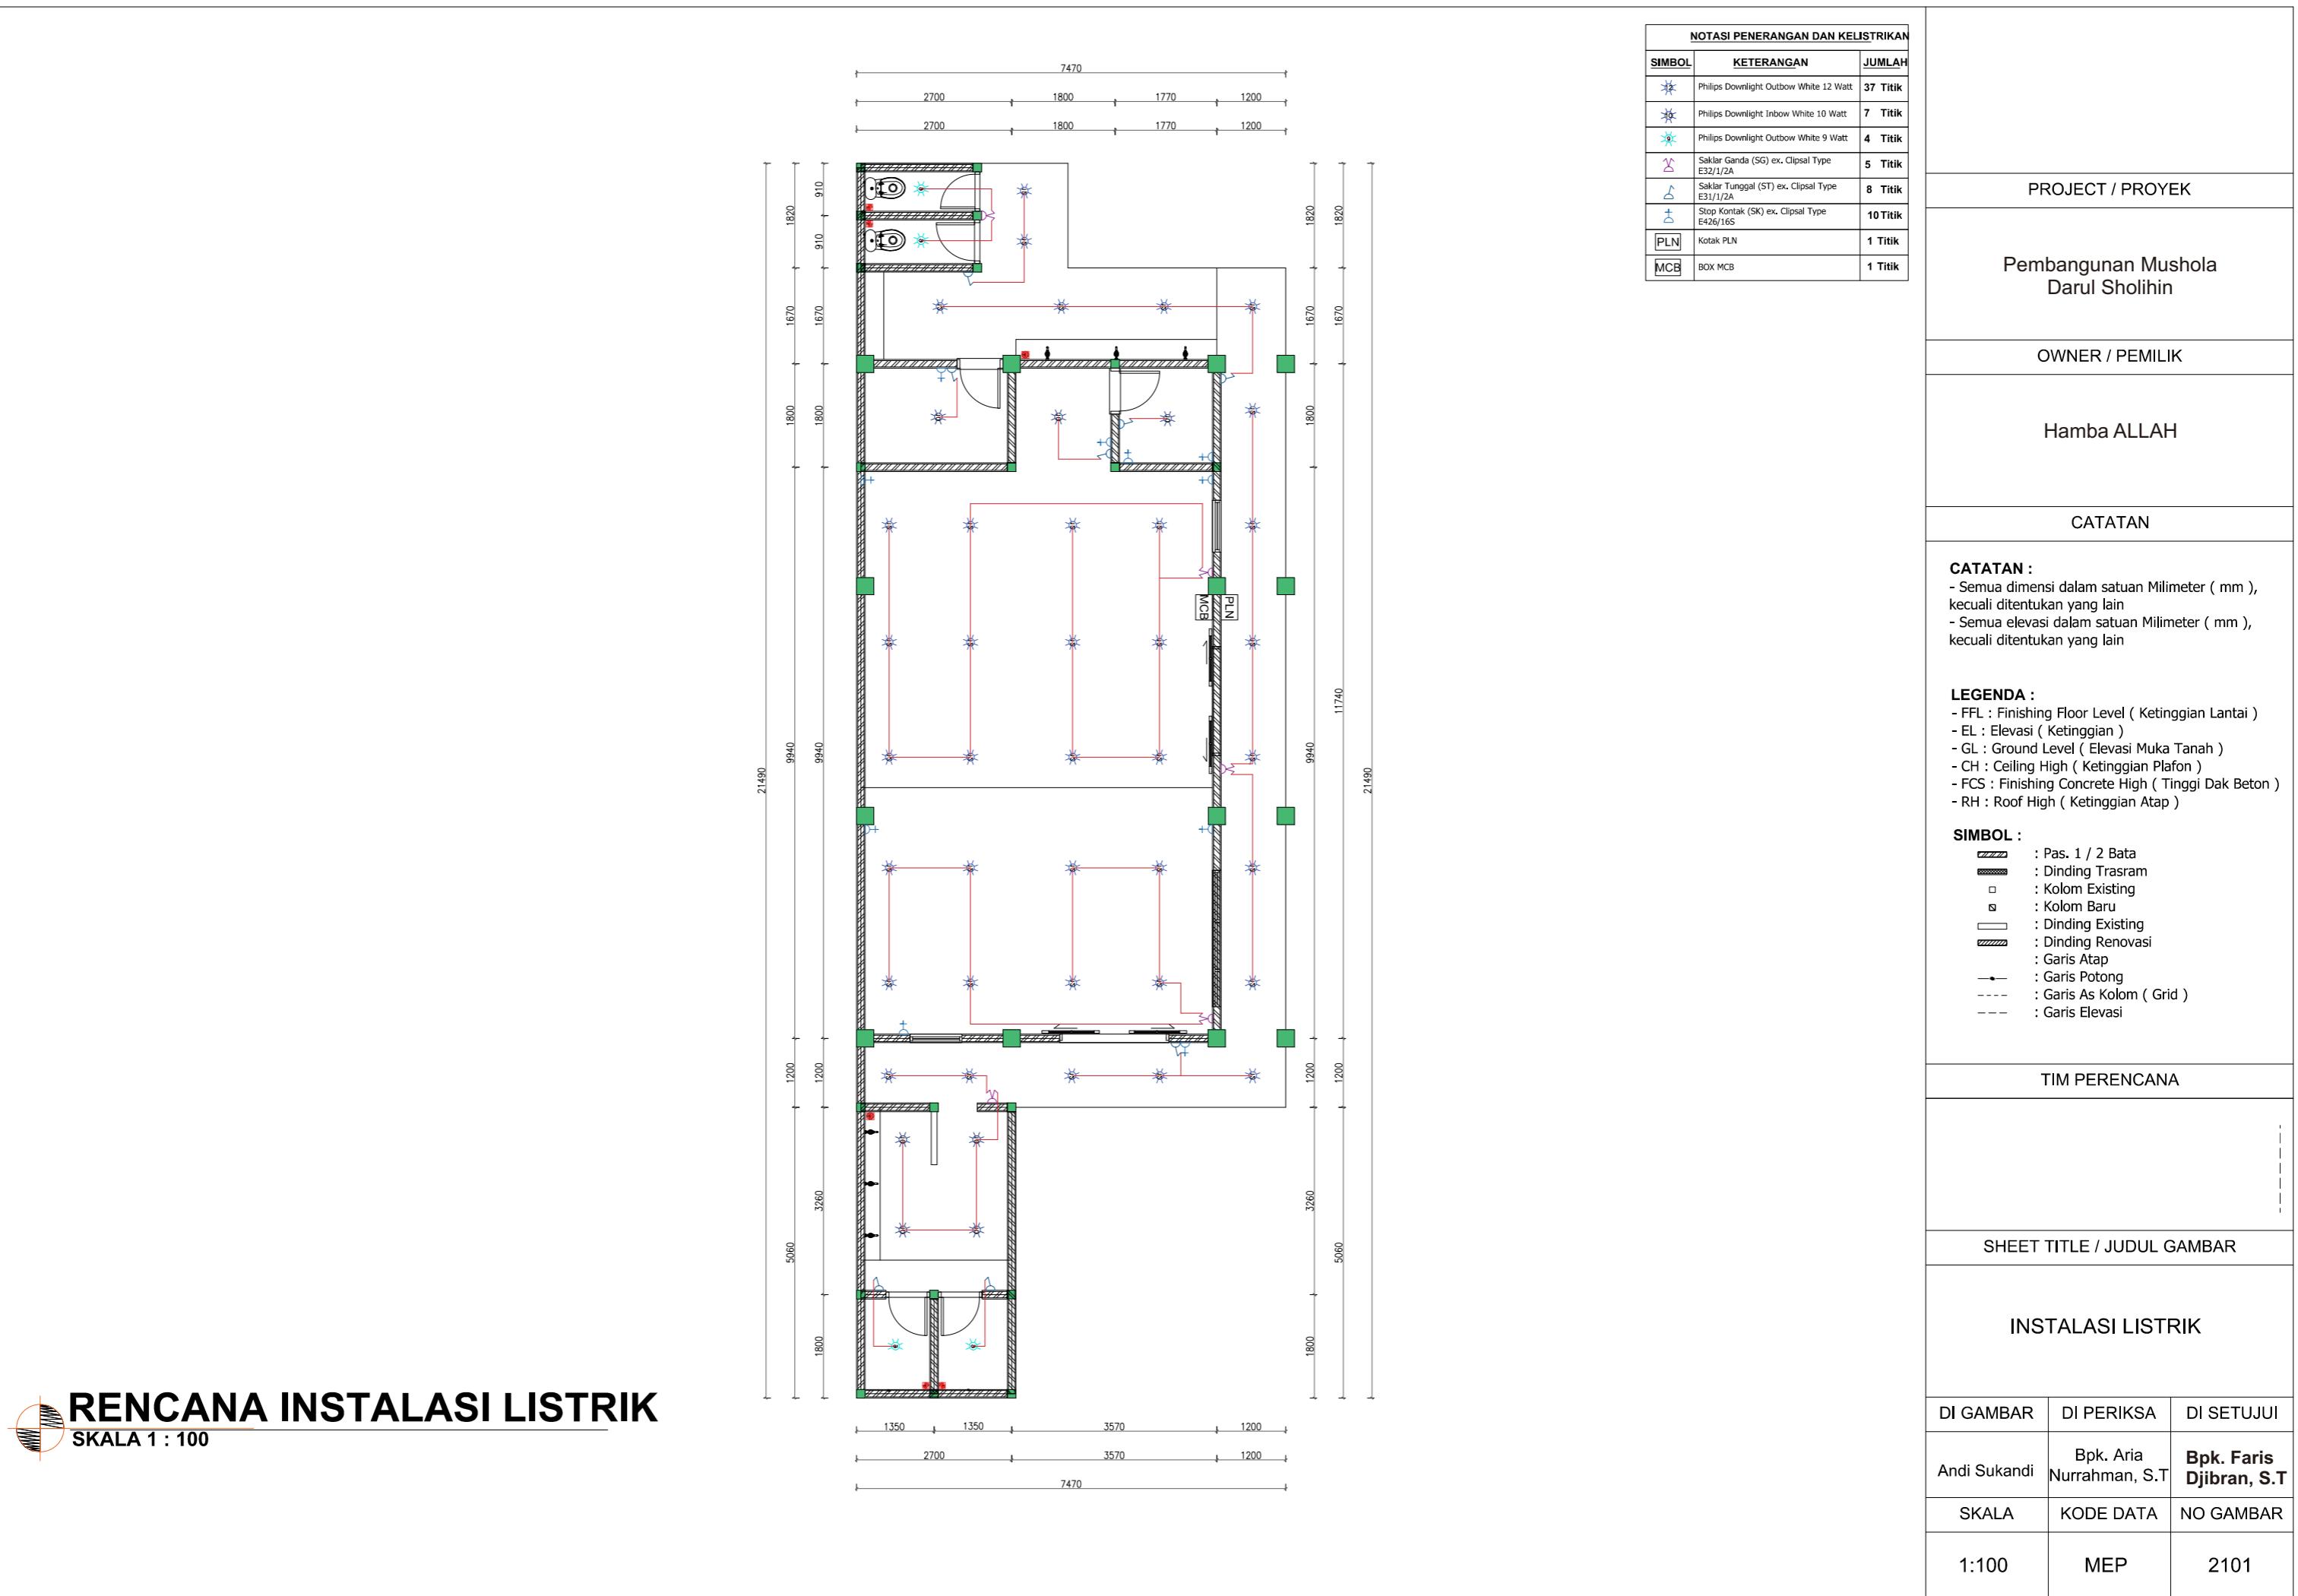



RENCANA AIR BERSIH

SKALA 1 : 100

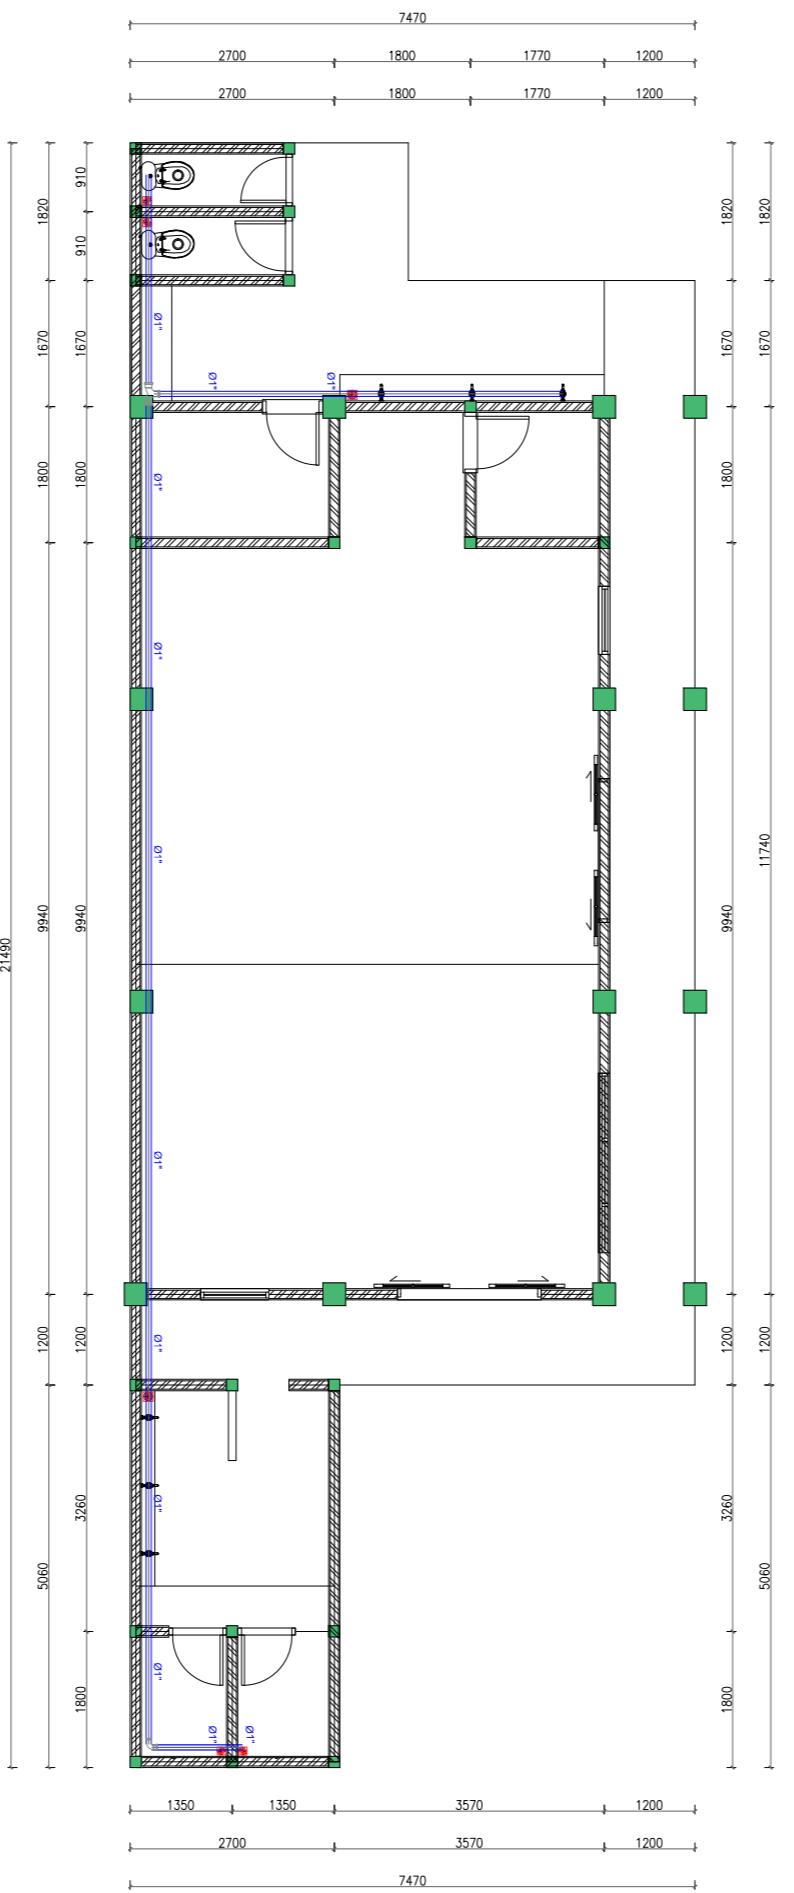


PROJECT / PROYEK		
Pembangunan Mushola Darul Sholihin		
OWNER / PEMILIK		
Hamba ALLAH		
CATATAN		
CATATAN :		
<ul style="list-style-type: none"> - Semua dimensi dalam satuan Milimeter (mm), kecuali ditentukan yang lain - Semua elevasi dalam satuan Milimeter (mm), kecuali ditentukan yang lain 		
LEGENDA :		
<ul style="list-style-type: none"> - FFL : Finishing Floor Level (Ketinggian Lantai) - EL : Elevasi (Ketinggian) - GL : Ground Level (Elevasi Muka Tanah) - CH : Ceiling High (Ketinggian Plafon) - FCS : Finishing Concrete High (Tinggi Dak Beton) - RH : Roof High (Ketinggian Atap) 		
SIMBOL :		
        	<ul style="list-style-type: none"> : Pas. 1 / 2 Bata : Dinding Trasram : Kolom Existing : Kolom Baru : Dinding Existing : Dinding Renovasi : Garis Atap : Garis Potong : Garis As Kolom (Grid) : Garis Elevasi 	
TIM PERENCANA		
SHEET TITLE / JUDUL GAMBAR		
INSTALASI AIR BERSIH		
DI GAMBAR	DI PERIKSA	DI SETUJUI
Andi Sukandi	Bpk. Aria Nurrahman, S.T	Bpk. Faris Djibrain, S.T
SKALA	KODE DATA	NO GAMBAR
1:100	MEP	2102




RENCANA INSTALASI AIR BEKAS

SKALA 1 : 100

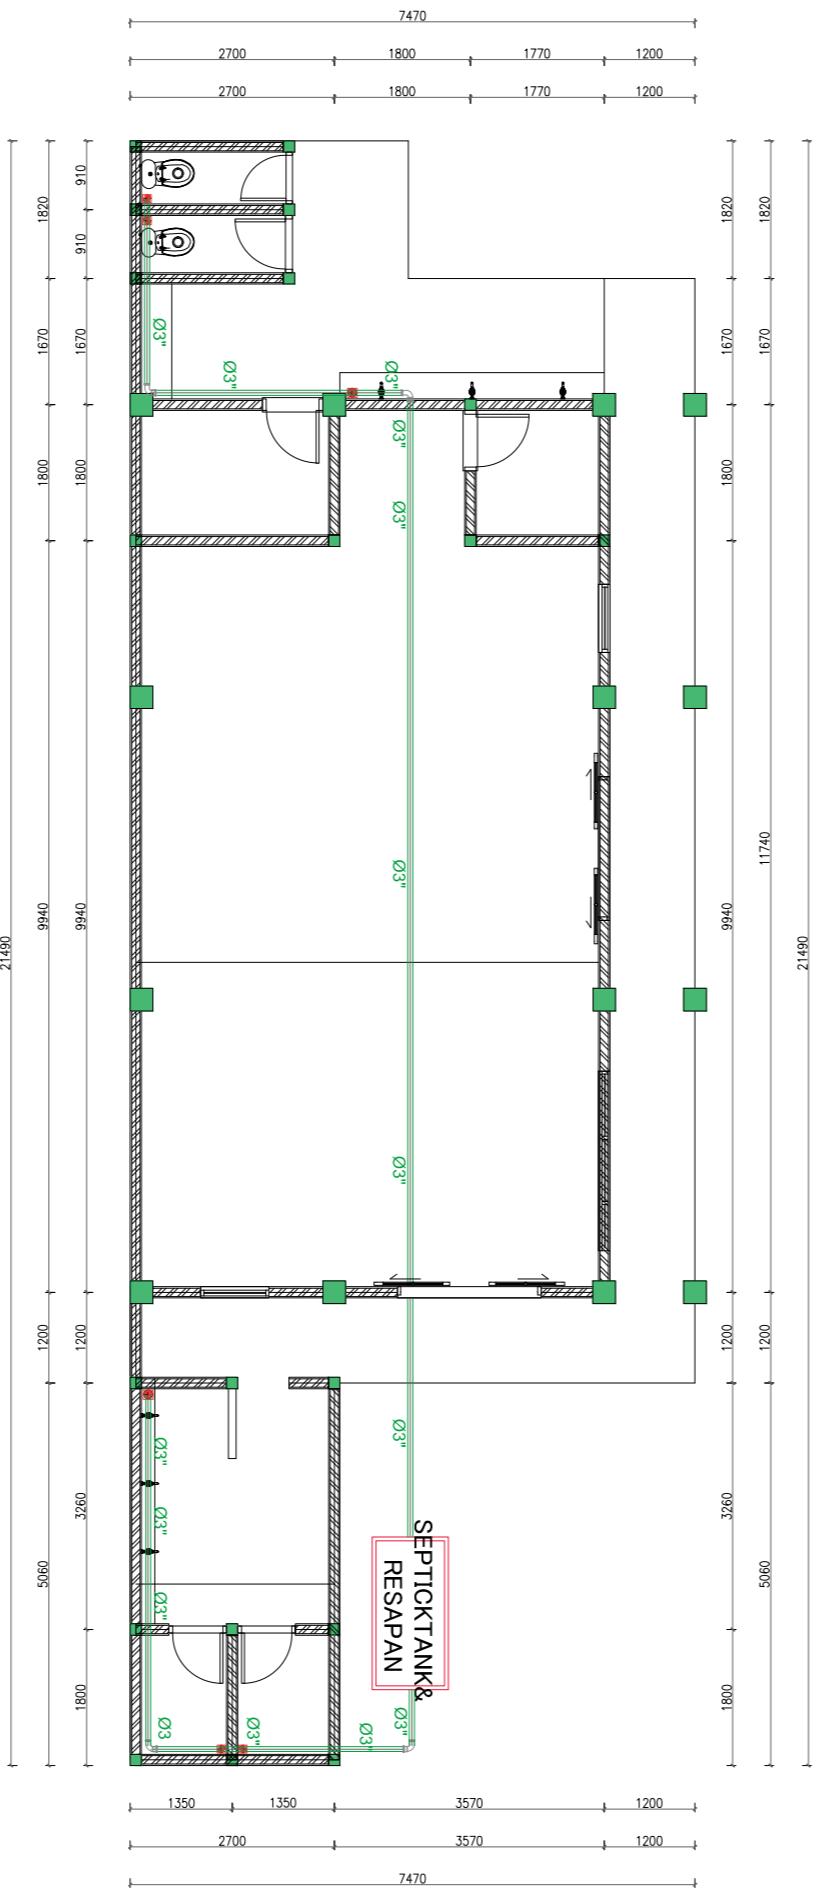

PROJECT / PROYEK		
Pembangunan Mushola Darul Sholihin		
OWNER / PEMILIK		
Hamba ALLAH		
CATATAN		
CATATAN : - Semua dimensi dalam satuan Milimeter (mm), kecuali ditentukan yang lain - Semua elevasi dalam satuan Milimeter (mm), kecuali ditentukan yang lain		
LEGENDA : - FFL : Finishing Floor Level (Ketinggian Lantai) - EL : Elevasi (Ketinggian) - GL : Ground Level (Elevasi Muka Tanah) - CH : Ceiling High (Ketinggian Plafon) - FCS : Finishing Concrete High (Tinggi Dak Beton) - RH : Roof High (Ketinggian Atap)		
SIMBOL :  : Pas. 1 / 2 Bata  : Dinding Trasram  : Kolom Existing  : Kolom Baru  : Dinding Existing  : Dinding Renovasi  : Garis Atap  : Garis Potong  : Garis As Kolom (Grid)  : Garis Elevasi		
TIM PERENCANA		
SHEET TITLE / JUDUL GAMBAR		
INSTALASI AIR BEKAS		
DI GAMBAR	DI PERIKSA	DI SETUJUI
Andi Sukandi	Bpk. Aria Nurrahman, S.T	Bpk. Faris Djibrain, S.T
SKALA	KODE DATA	NO GAMBAR
1:100	MEP	2103

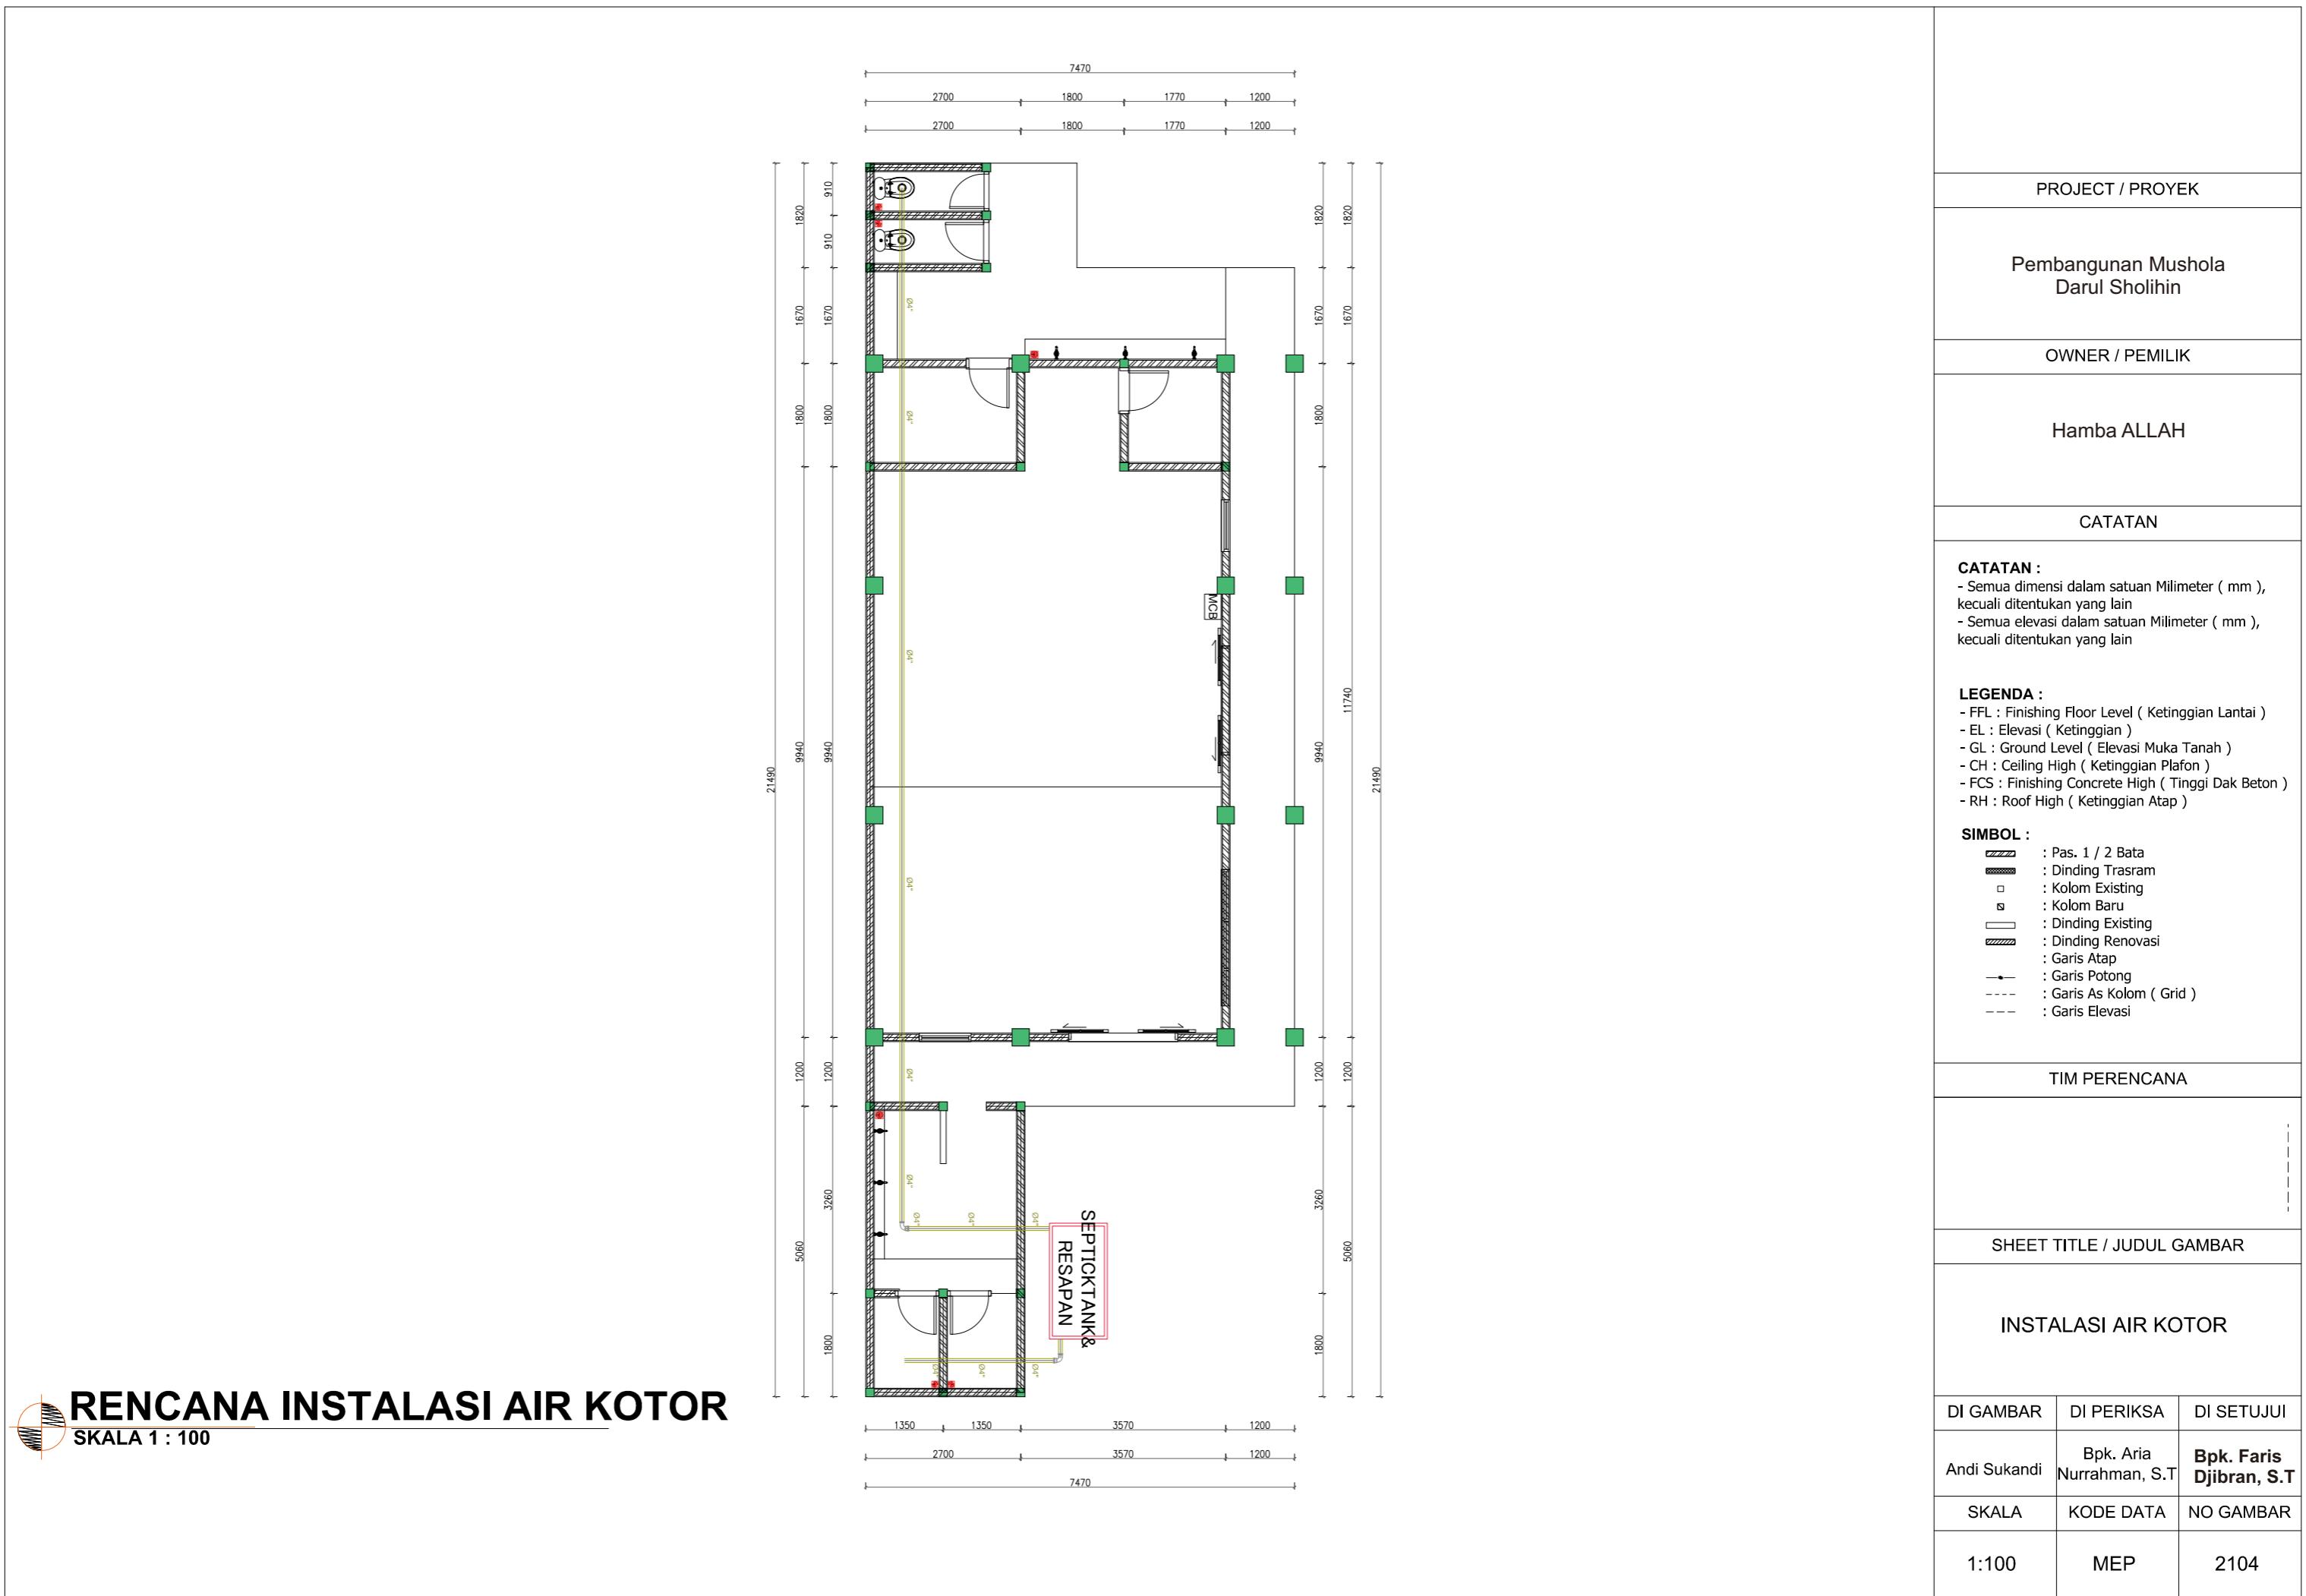

PROJECT / PROYEK

Pembangunan Mushola
Darul Sholihin

OWNER / PEMILIK

Hamba ALLAH


CATATAN

TIM PERENCANA

SHEET TITLE / JUDUL GAMBAR


DETAIL SEPTICTANK #1

DI GAMBAR	DI PERIKSA	DI SETUJUI
Andi Sukandi	Bpk. Aria Nurrahman, S.T	Bpk. Faris Djibrain, S.T
SKALA	KODE DATA	NO GAMBAR
1:25	MEP	2105

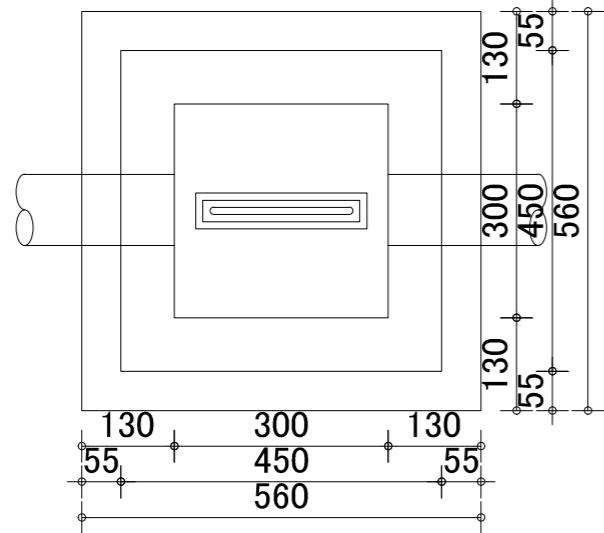


DENAH BAK KONTROL

Skala 1:10

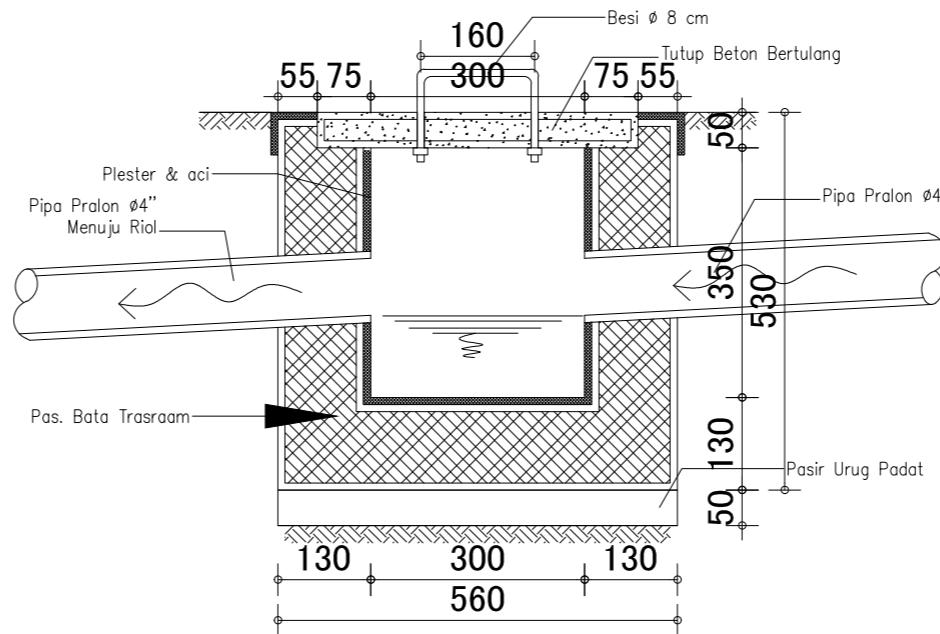


DETAIL BAK KONTROL

Skala 1:10

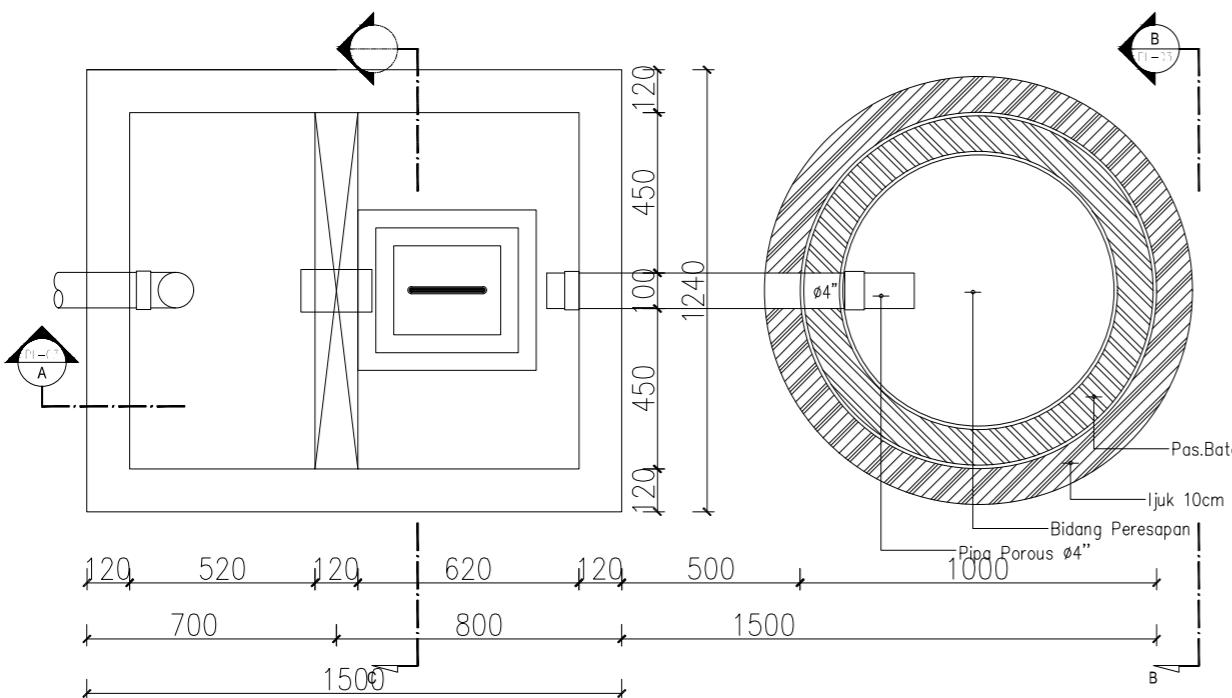


TAMPAK SEPTICTANK

Skala 1:20

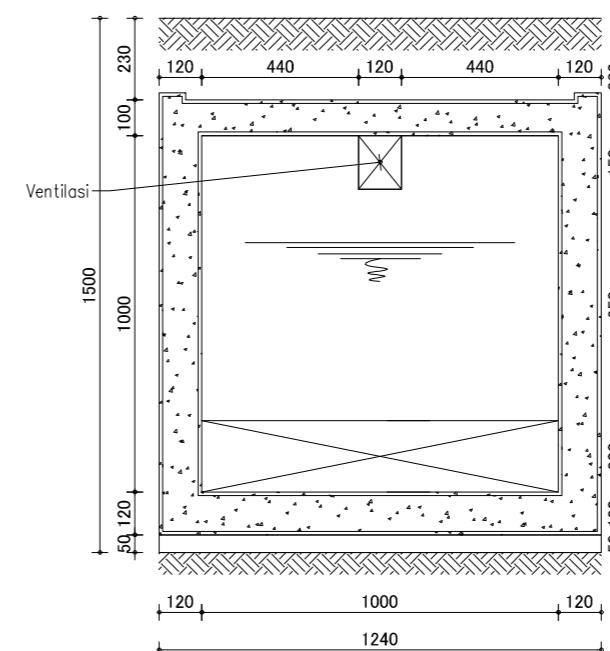


PROJECT / PROYEK		
Pembangunan Mushola Darul Sholihin		
OWNER / PEMILIK		
Hamba ALLAH		
CATATAN		
TIM PERENCANA		
SHEET TITLE / JUDUL GAMBAR		
DETAIL SEPTICTANK #2		
DI GAMBAR	DI PERIKSA	DI SETUJUI
Andi Sukandi	Bpk. Aria Nurrahman, S.T	Bpk. Faris Djibrani, S.T
SKALA	KODE DATA	NO GAMBAR
1:25	MEP	2106

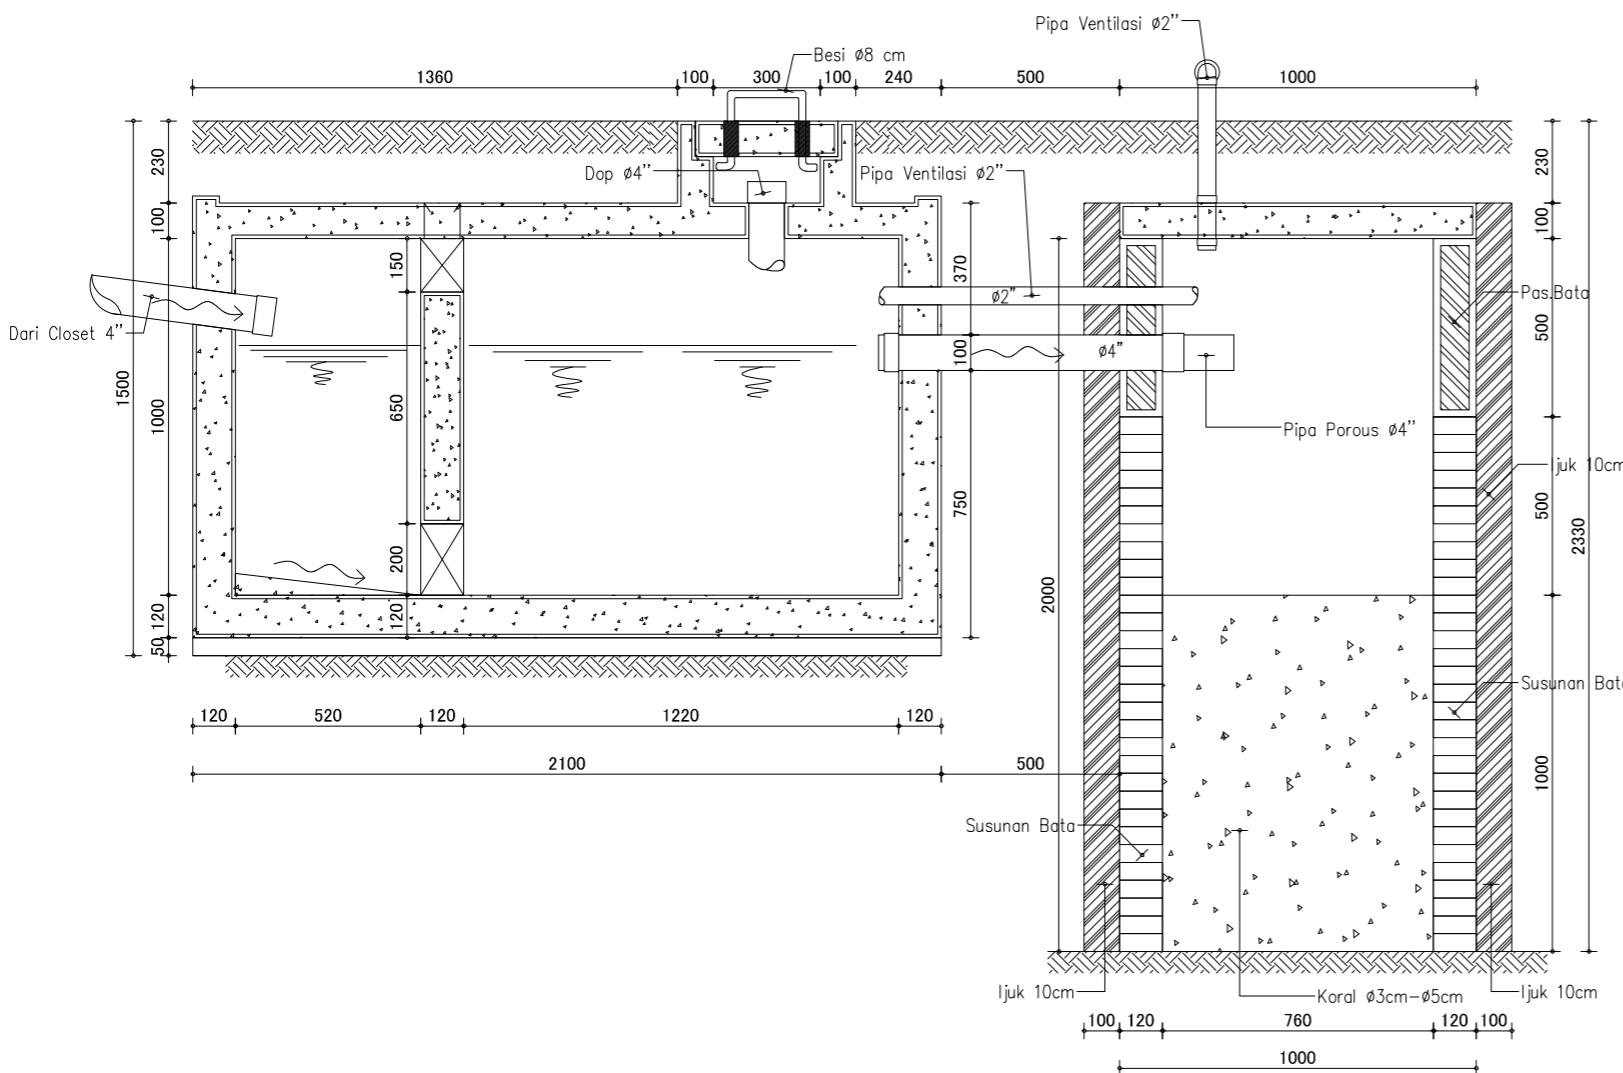

DETAIL SEPTICKTANK
POT-A-A

Skala 1:20

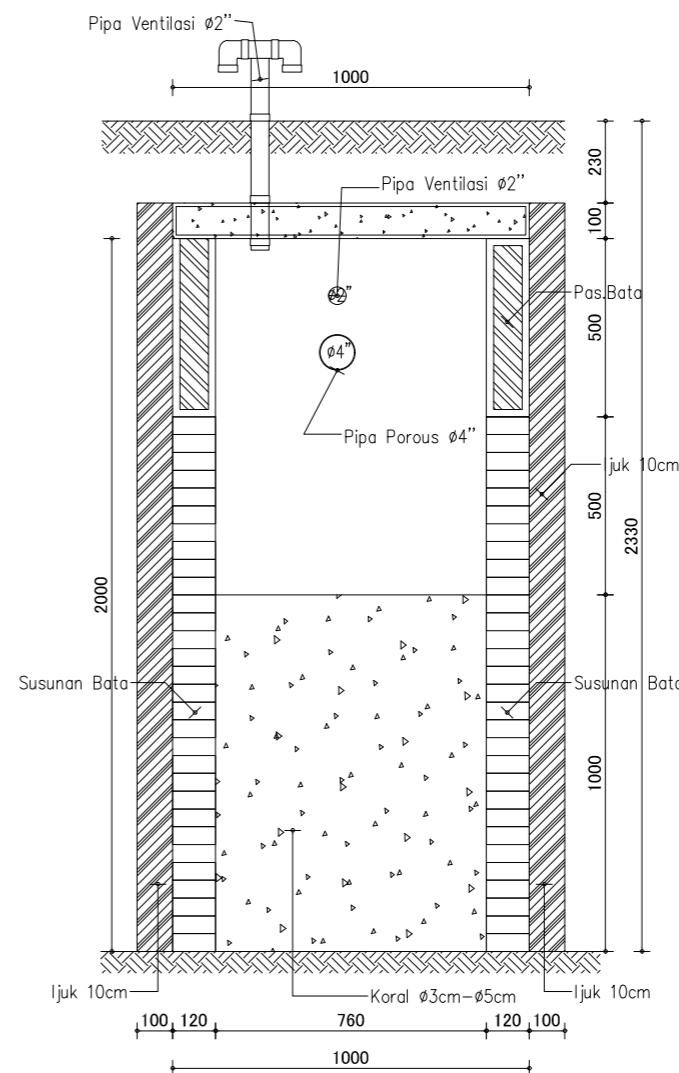

DETAIL RESAPAN

Skala 1:20

DETAIL SEPTICTANK #2

DI GAMBAR	DI PERIKSA	DI SETUJUI
Andi Sukandi	Bpk. Aria Nurrahman, S.T	Bpk. Faris Djibrain, S.T
SKALA	KODE DATA	NO GAMBAR
1:25	MEP	2106

STRUKTUR
PERENCANAAN PEMBANGUNAN

MUSHOLA
DARUL SHOLIHIN

DAFTAR GAMBAR PERENCANAAN PEMBANGUNAN


DAFTAR ISI GAMBAR STRUKTUR

NO GAMBAR	JUDUL GAMBAR	HAL - GAMBAR
STRUKTUR		
01. RENCANA PONDASI & SLOOF		
STR	DENAH RENCANA SLOOF	3101
STR	DENAH RENCANA FOOTPLATE	3102
STR	DENAH RENCANA PONDASI BATU KALI	3103
02. RENCANA KOLOM		
STR	DENAH KOLOM	3104
03. RENCANA BALOK		
STR	DENAH PEMBALOKAN	3105
04. RENCANA PLAT LANTAI		
STR	DETAIL PONDASI	3106
STR	DETAIL PENULANGAN SLOOF,KOLOM,BALOK	3107
STR	DETAIL PLAT LANTAI	3108





RENCANA DENAH SLOOF


SKALA 1 : 100

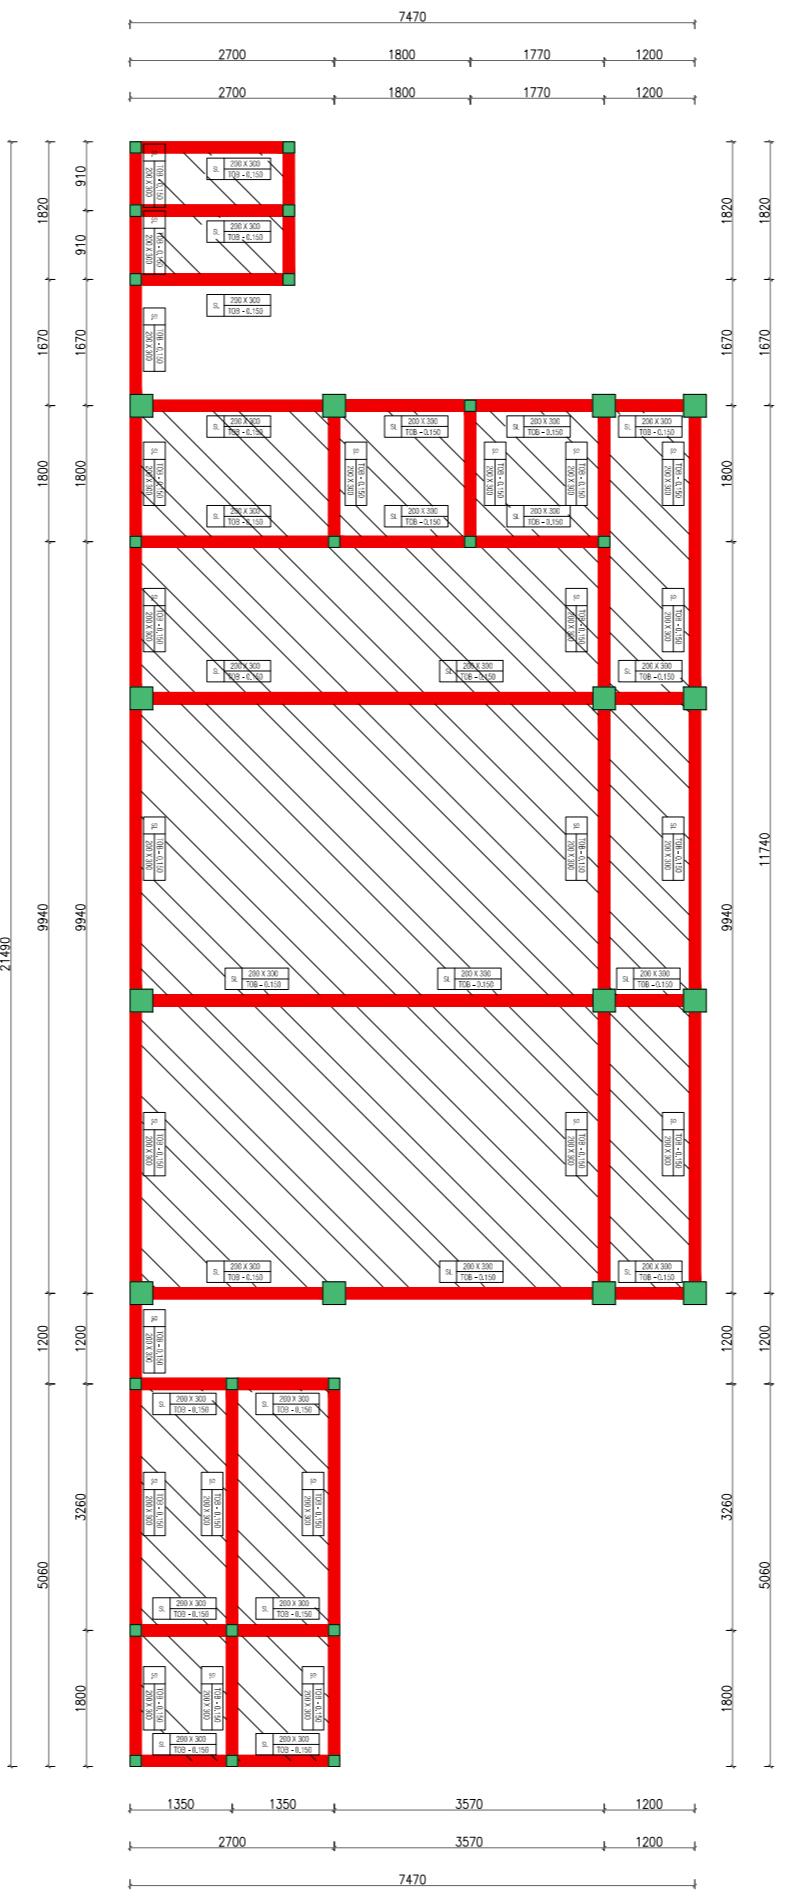

PROJECT / PROYEK																						
Pembangunan Mushola Darul Sholihin																						
OWNER / PEMILIK																						
Hamba ALLAH																						
CATATAN																						
CATATAN : <ul style="list-style-type: none">- Semua dimensi dalam satuan Milimeter (mm), kecuali ditentukan yang lain- Semua elevasi dalam satuan Milimeter (mm), kecuali ditentukan yang lain																						
LEGENDA : <ul style="list-style-type: none">- FFL : Finishing Floor Level (Ketinggian Lantai)- EL : Elevasi (Ketinggian)- GL : Ground Level (Elevasi Muka Tanah)- CH : Ceiling High (Ketinggian Plafon)- FCS : Finishing Concrete High (Tinggi Dak Beton)- RH : Roof High (Ketinggian Atap)																						
SIMBOL : <table border="0"><tr><td></td><td>: Pas. 1 / 2 Bata</td></tr><tr><td></td><td>: Dinding Trasram</td></tr><tr><td></td><td>: Kolom Existing</td></tr><tr><td></td><td>: Kolom Baru</td></tr><tr><td></td><td>: Dinding Existing</td></tr><tr><td></td><td>: Dinding Renovasi</td></tr><tr><td></td><td>: Garis Atap</td></tr><tr><td></td><td>: Garis Potong</td></tr><tr><td></td><td>: Garis As Kolom (Grid)</td></tr><tr><td></td><td>: Garis Elevasi</td></tr></table>				: Pas. 1 / 2 Bata		: Dinding Trasram		: Kolom Existing		: Kolom Baru		: Dinding Existing		: Dinding Renovasi		: Garis Atap		: Garis Potong		: Garis As Kolom (Grid)		: Garis Elevasi
	: Pas. 1 / 2 Bata																					
	: Dinding Trasram																					
	: Kolom Existing																					
	: Kolom Baru																					
	: Dinding Existing																					
	: Dinding Renovasi																					
	: Garis Atap																					
	: Garis Potong																					
	: Garis As Kolom (Grid)																					
	: Garis Elevasi																					
TIM PERENCANA																						
SHEET TITLE / JUDUL GAMBAR																						
RENCANA DENAH SLOOF																						
DI GAMBAR	DI PERIKSA	DI SETUJUI																				
Andi Sukandi	Bpk. Aria Nurrahman, S.T	Bpk. Faris Djibrain, S.T																				
SKALA	KODE DATA	NO GAMBAR																				
1:100	STR	3101																				

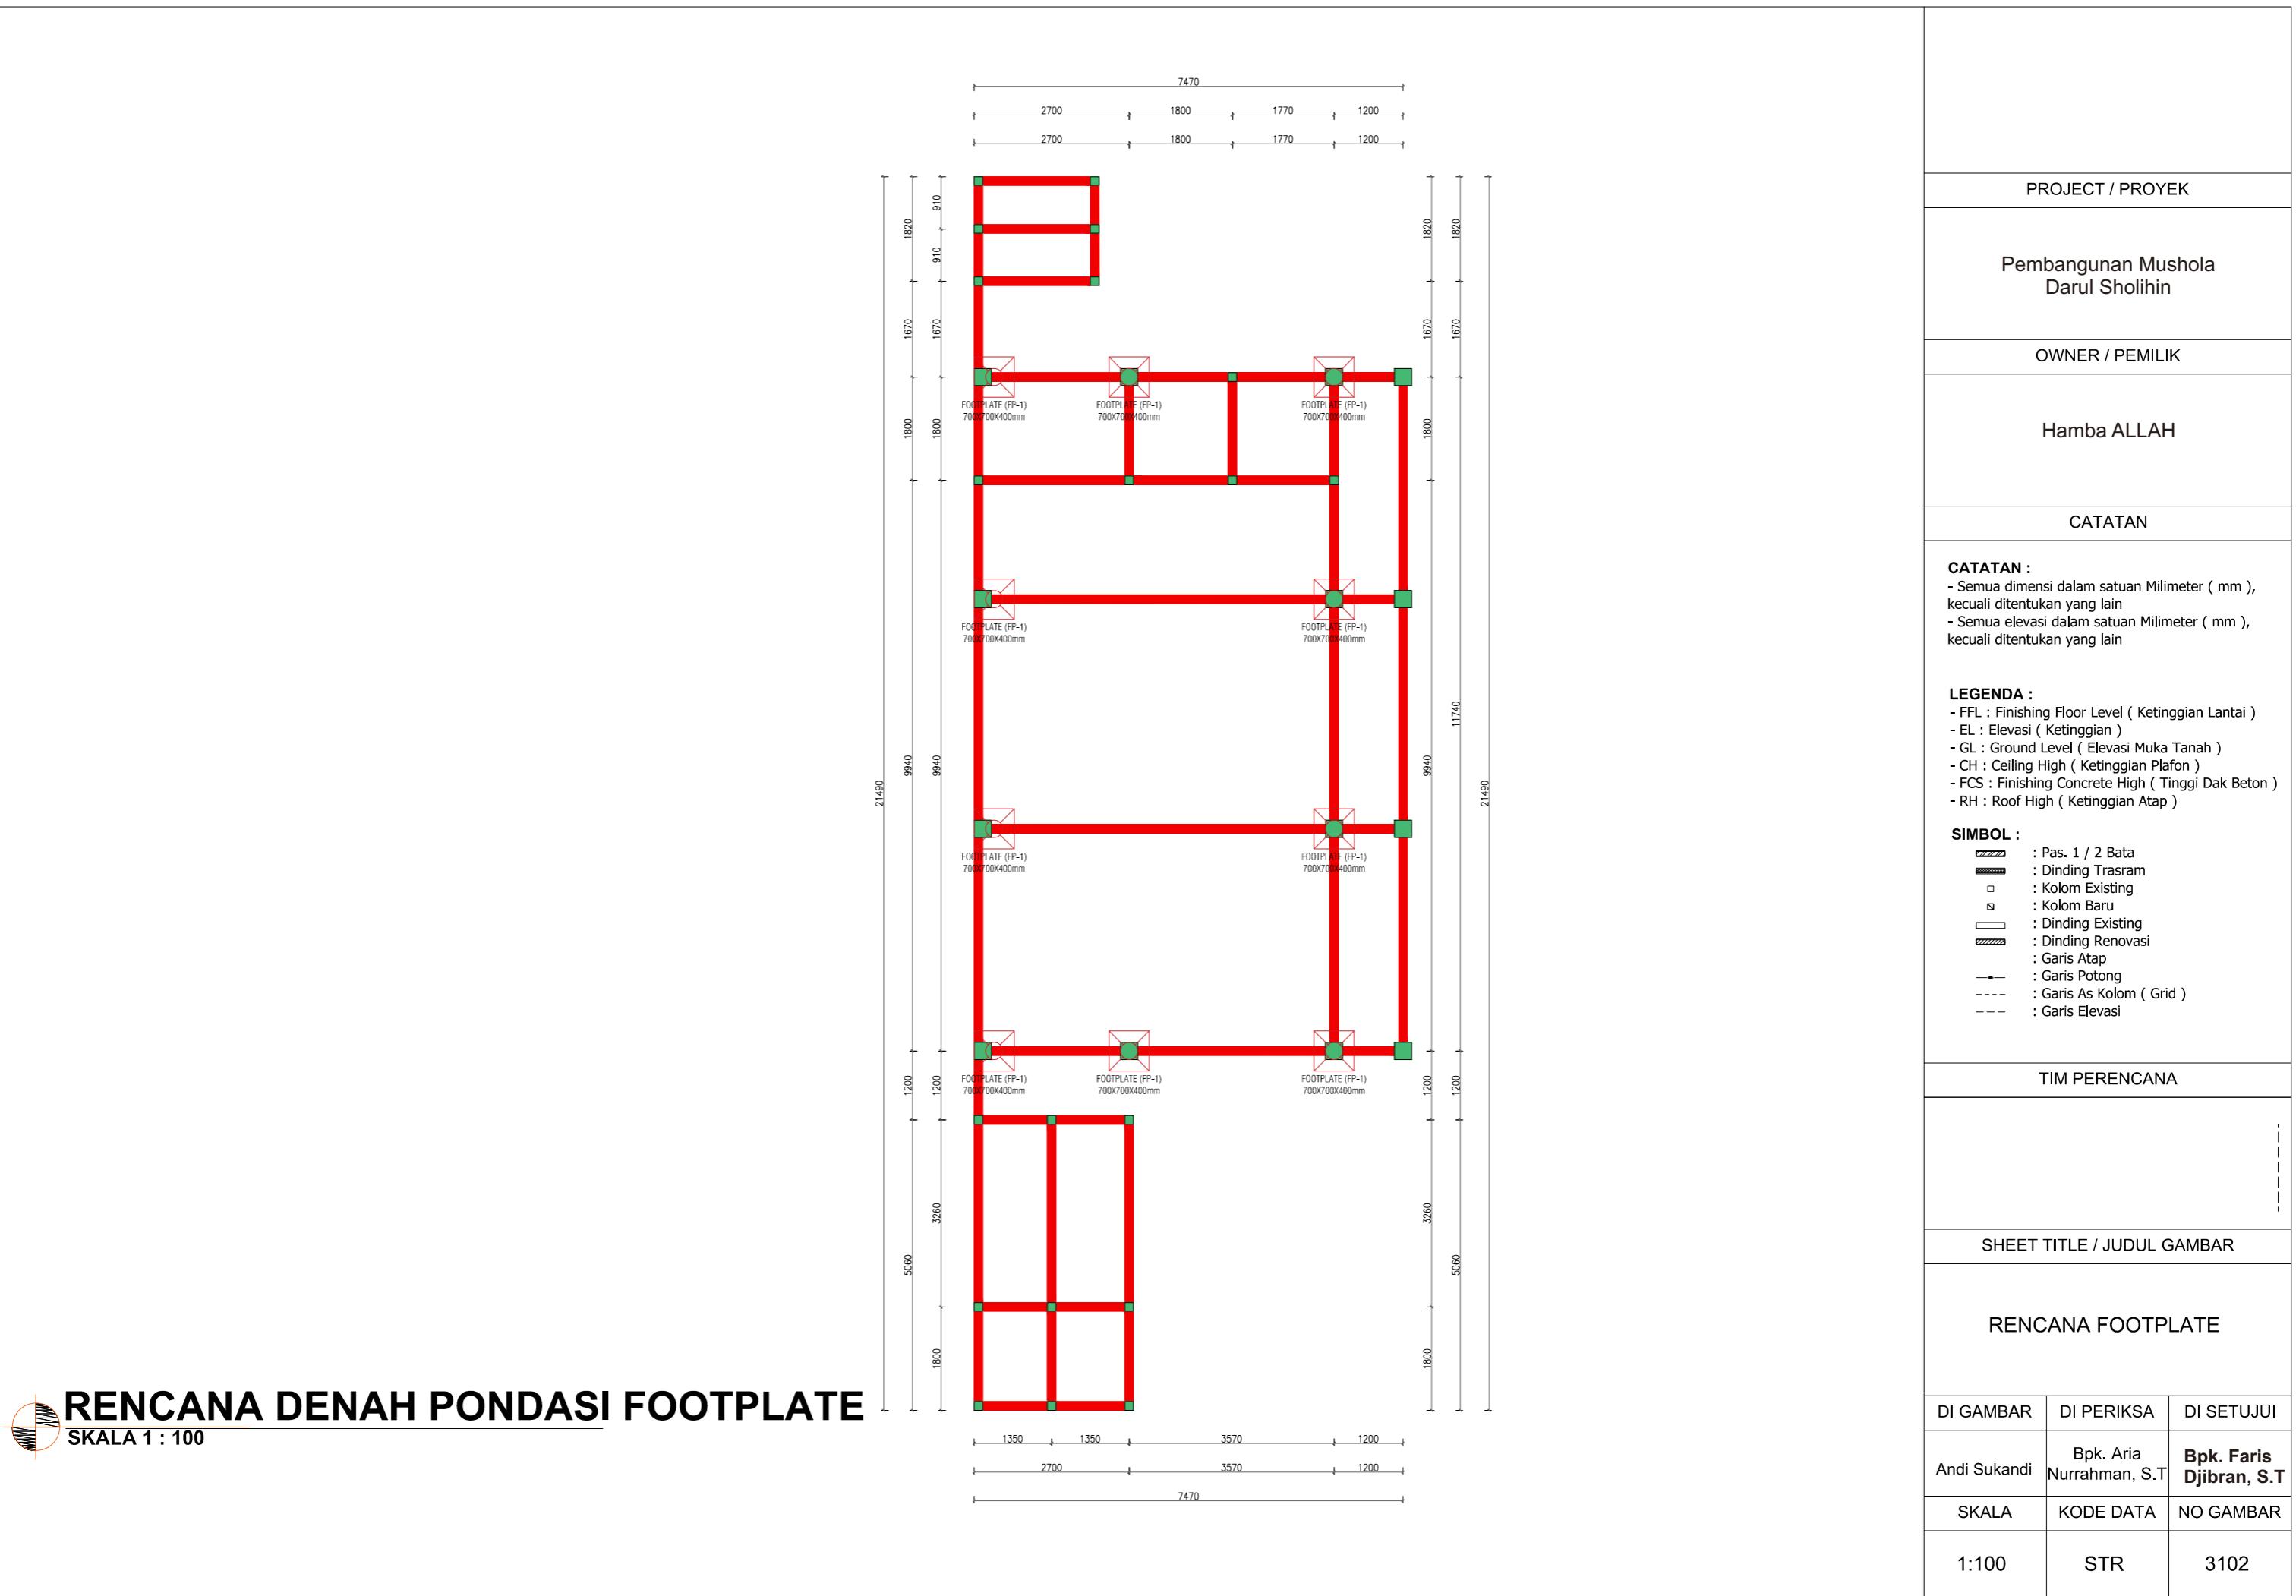


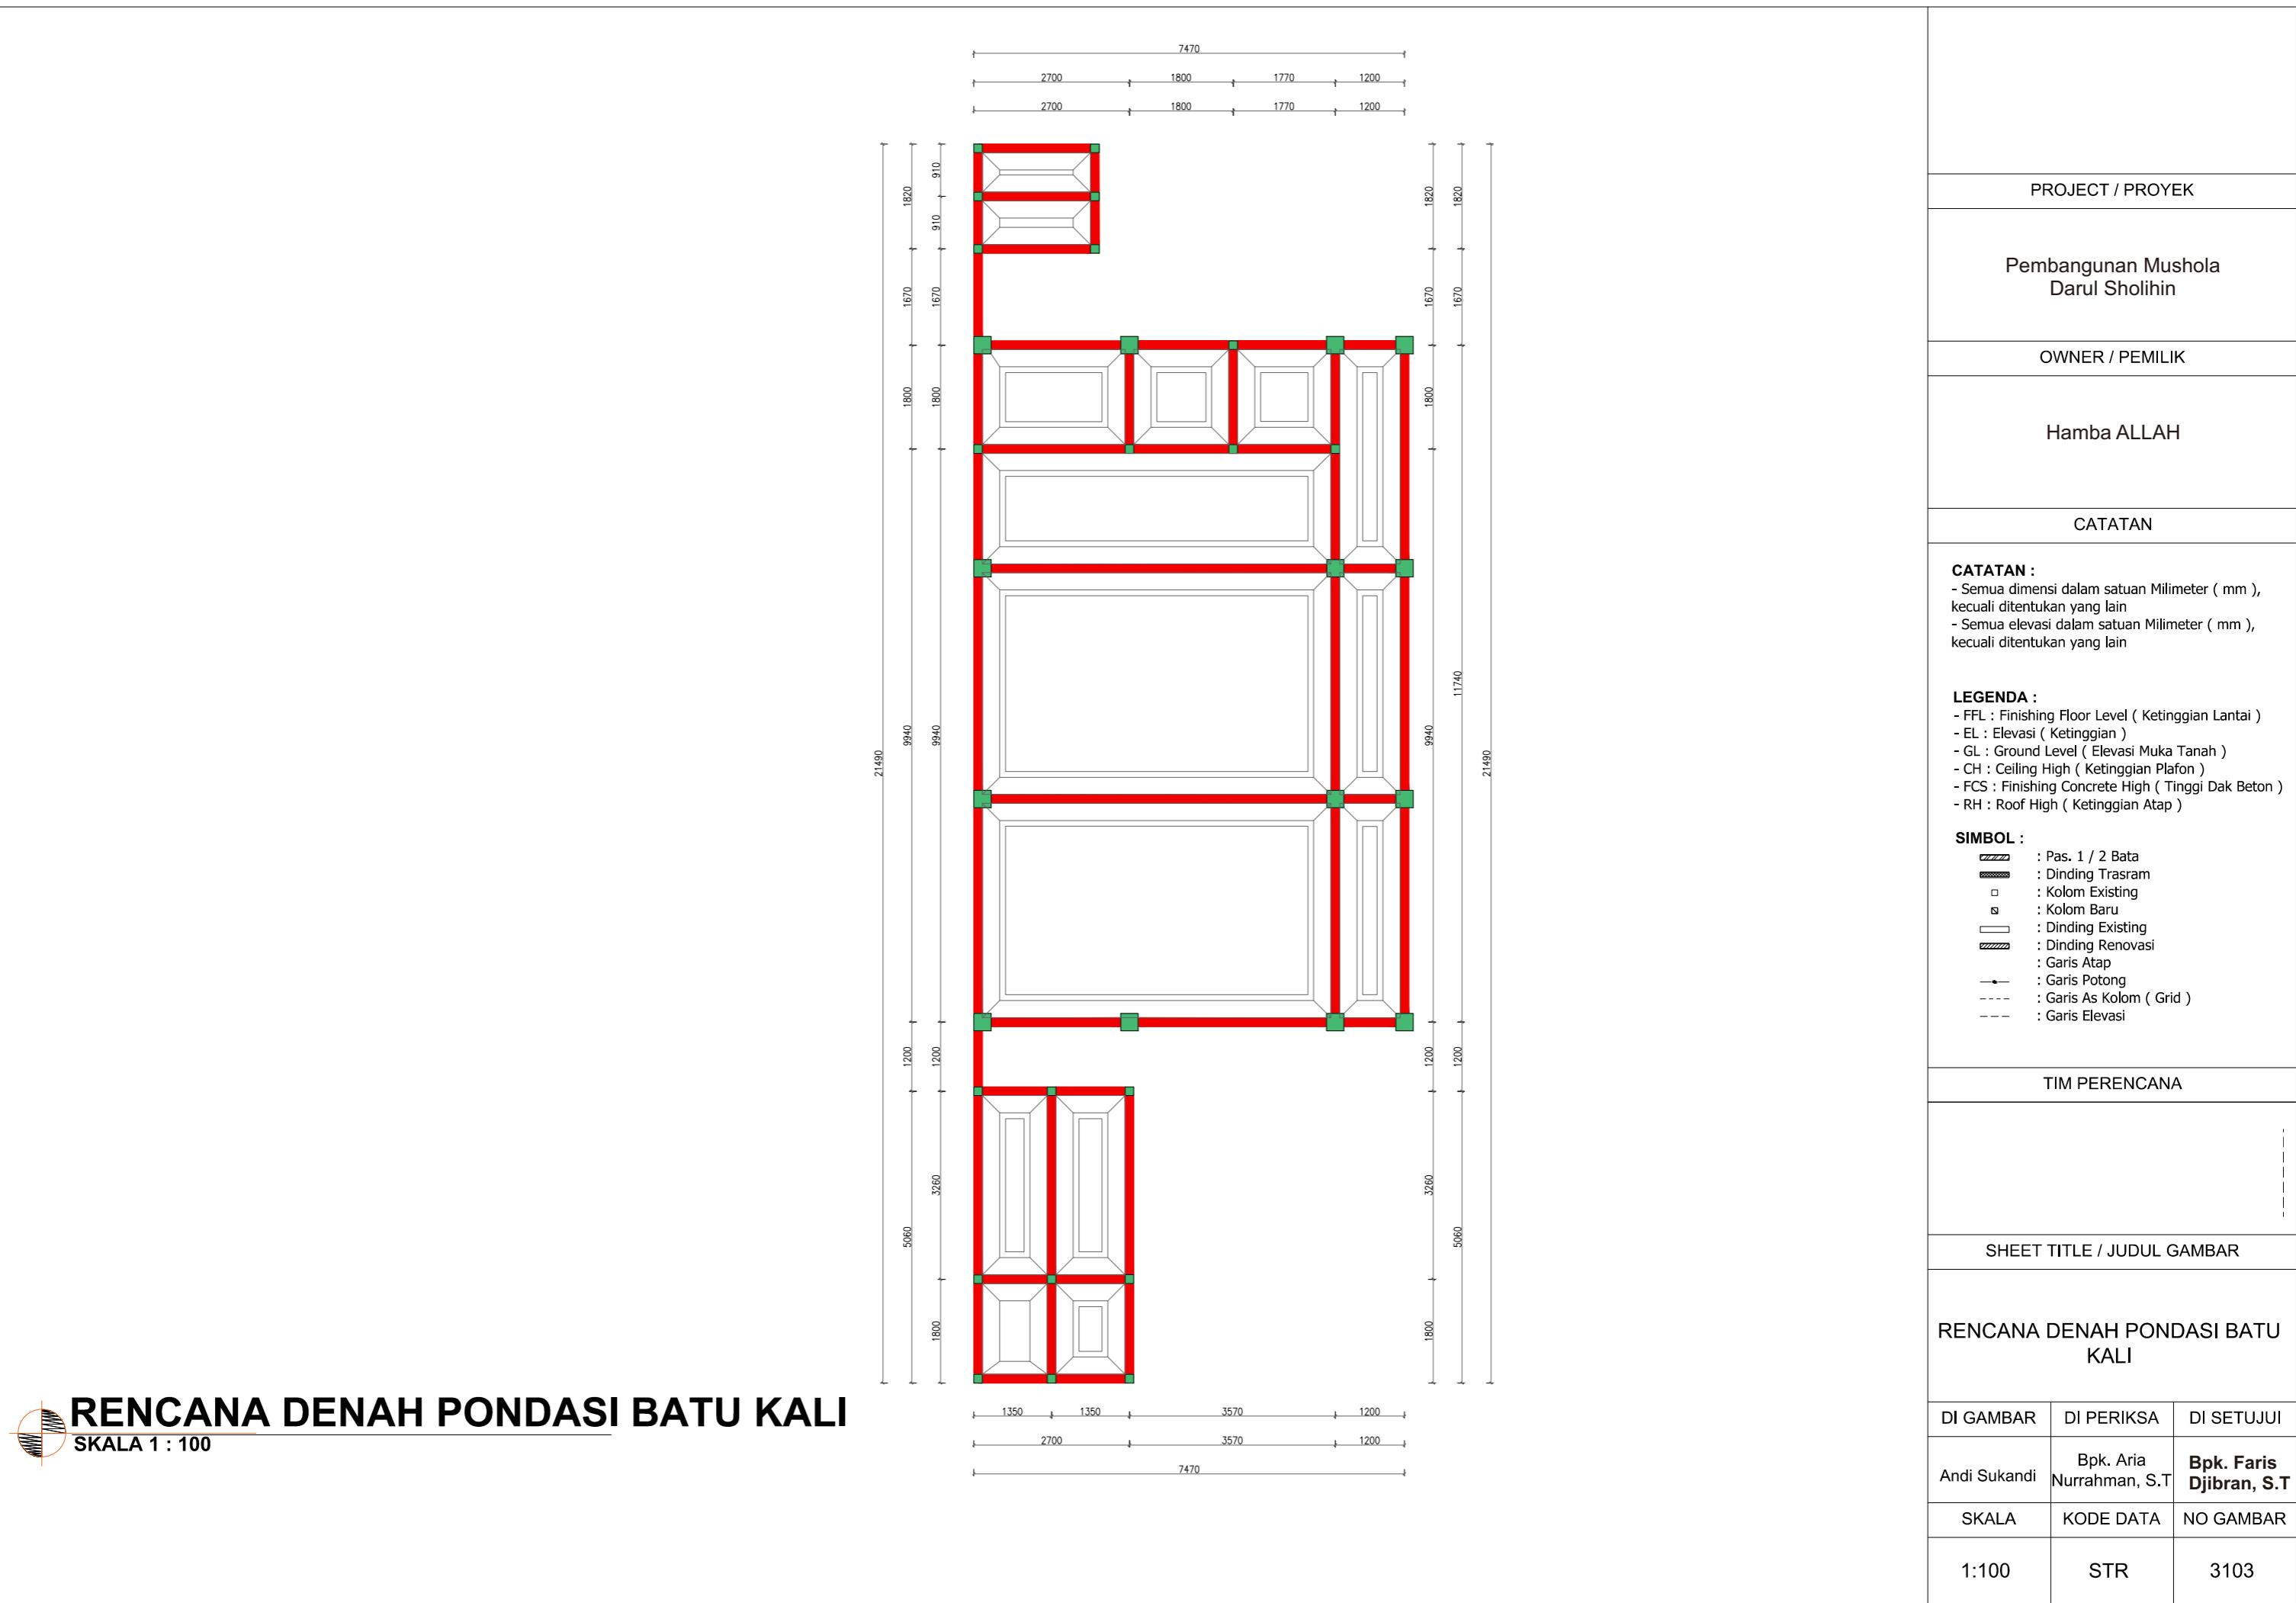

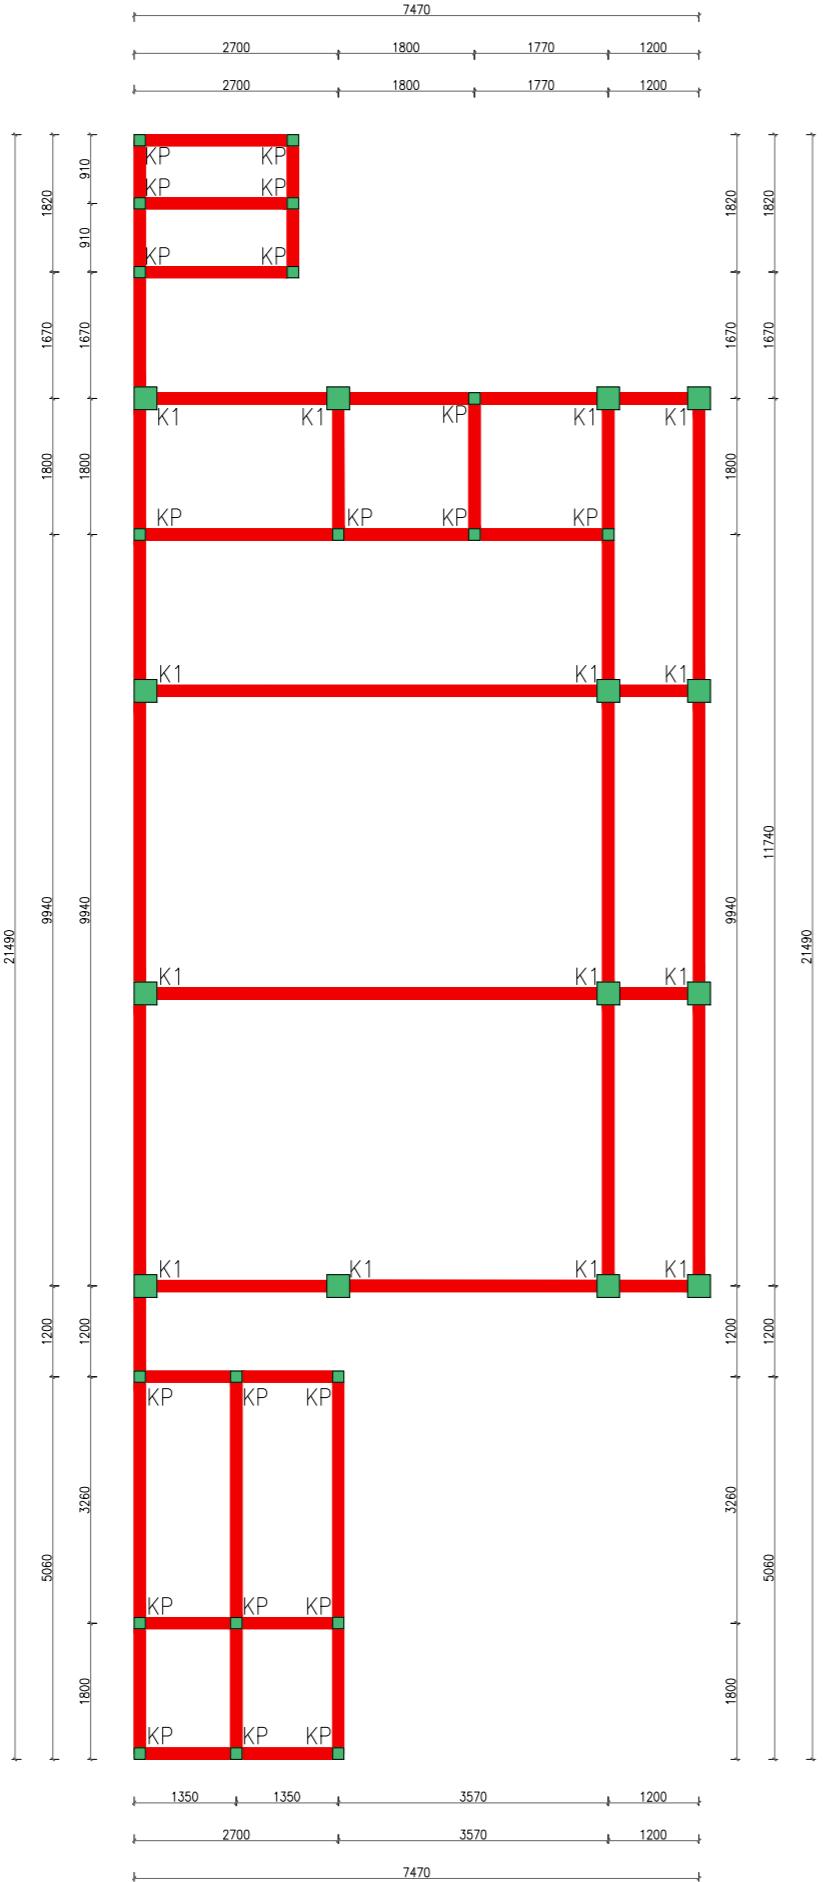

 SKALA 1 : 100

RENCANA DENAH KOLOM Elv + 5.900

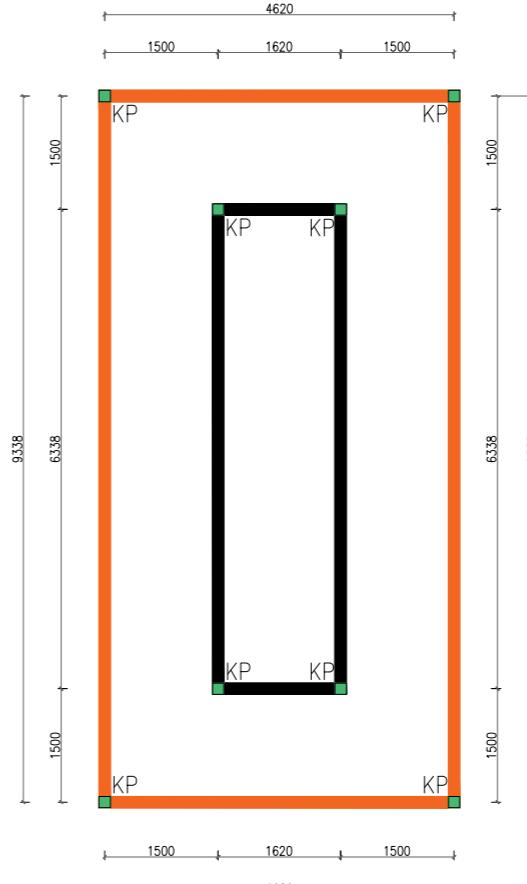

PROJECT / PROYEK

Pembangunan Mushola
Darul Sholihin

OWNER / PEMILIK

Hamba ALLAH

CATATAN

CATATAN :
 - Semua dimensi dalam satuan Milimeter (mm),
 kecuali ditentukan yang lain
 - Semua elevasi dalam satuan Milimeter (mm),
 kecuali ditentukan yang lain

LEGENDA :
 - FFL : Finishing Floor Level (Ketinggian Lantai)
 - EL : Elevasi (Ketinggian)
 - GL : Ground Level (Elevasi Muka Tanah)
 - CH : Ceiling High (Ketinggian Plafon)
 - FCS : Finishing Concrete High (Tinggi Dak Beton)
 - RH : Roof High (Ketinggian Atap)

SIMBOL :

	: Pas. 1 / 2 Bata
	: Dinding Trasram
	: Kolom Existing
	: Kolom Baru
	: Dinding Existing
	: Dinding Renovasi
	: Garis Atap
	: Garis Potong
	: Garis As Kolom (Grid)
	: Garis Elevasi

TIM PERENCANA

SHEET TITLE / JUDUL GAMBAR


RENCANA DENAH KOLOM

DI GAMBAR DI PERIKSA DI SETUJUI

Andi Sukandi Bpk. Aria Nurrahman, S.T. **Bpk. Faris Djibrain, S.T**

SKALA KODE DATA NO GAMBAR

1:100 STR 3104

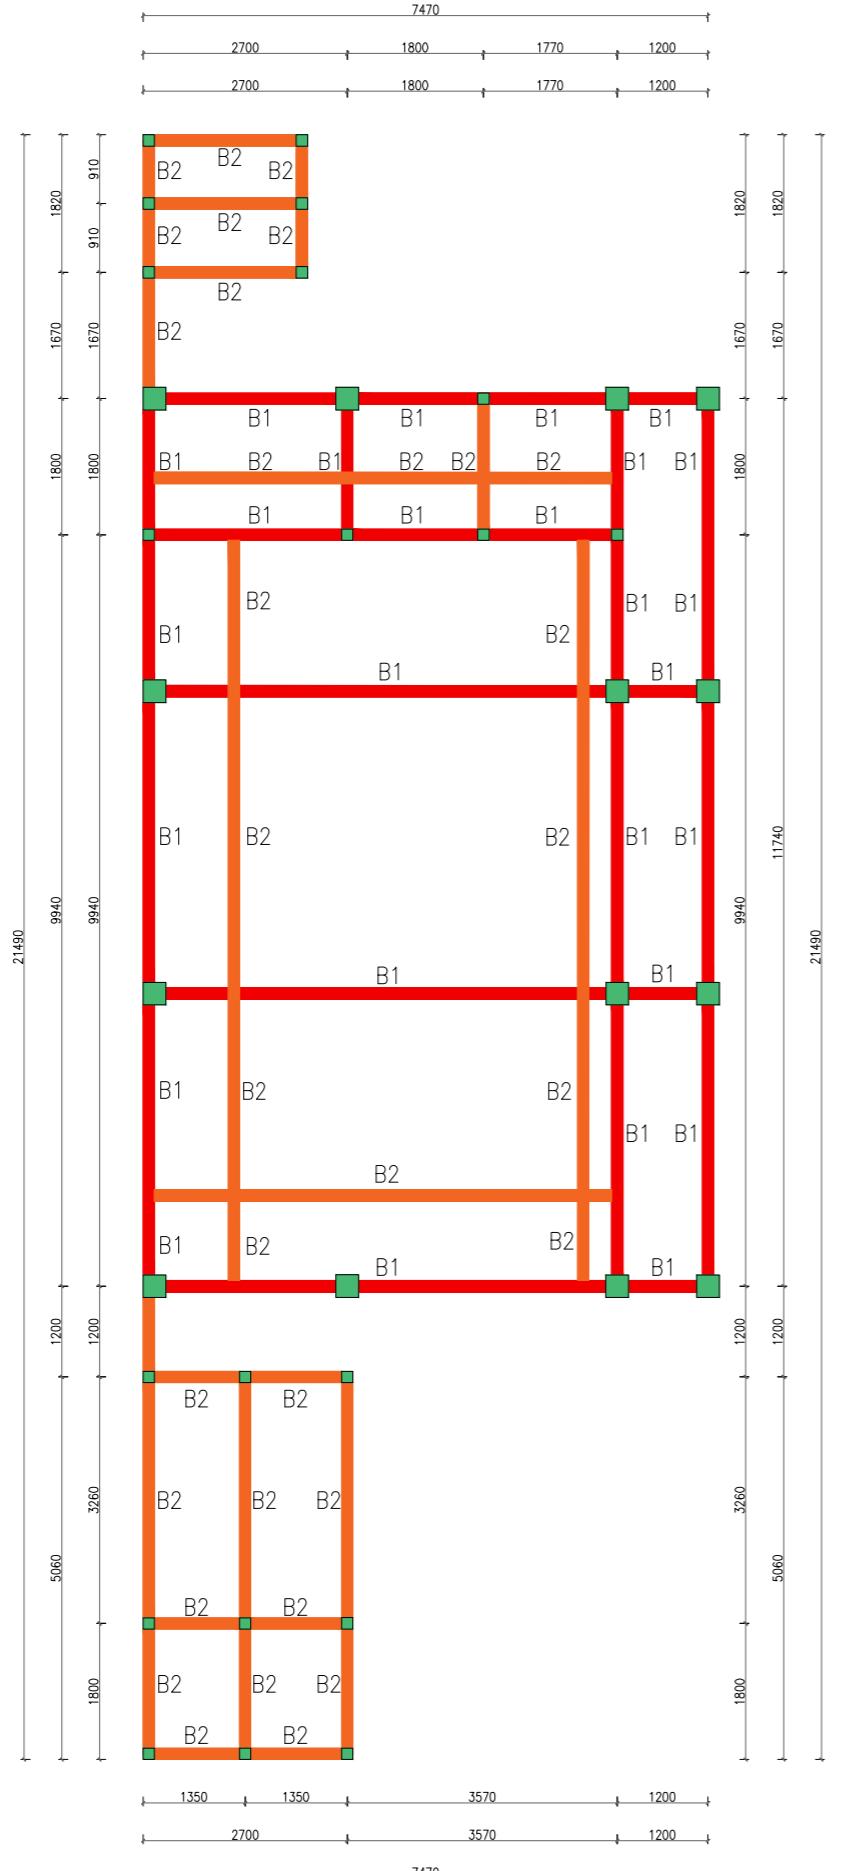

 RENCANA DENAH BALOK Elv + 5.900
SKALA 1 : 100

SKALA 1 : 100




RENCAN
SKALA 1 : 100

RENCANA DENAH BALOK


SKALA 1 : 100

PROJECT / PROYEK		
Pembangunan Mushola Darul Sholihin		
OWNER / PEMILIK		
Hamba ALLAH		
CATATAN		
CATATAN :		
<ul style="list-style-type: none"> - Semua dimensi dalam satuan Milimeter (mm), kecuali ditentukan yang lain - Semua elevasi dalam satuan Milimeter (mm), kecuali ditentukan yang lain 		
LEGENDA :		
<ul style="list-style-type: none"> - FFL : Finishing Floor Level (Ketinggian Lantai) - EL : Elevasi (Ketinggian) - GL : Ground Level (Elevasi Muka Tanah) - CH : Ceiling High (Ketinggian Plafon) - FCS : Finishing Concrete High (Tinggi Dak Beton) - RH : Roof High (Ketinggian Atap) 		
SIMBOL :		
	:	Pas. 1 / 2 Bata
	:	Dinding Trasram
	:	Kolom Existing
	:	Kolom Baru
	:	Dinding Existing
	:	Dinding Renovasi
	:	Garis Atap
	:	Garis Potong
	:	Garis As Kolom (Grid)
	:	Garis Elevasi
TIM PERENCANA		
SHEET TITLE / JUDUL GAMBAR		
RENCANA DENAH BALOK		
DI GAMBAR	DI PERIKSA	DI SETUJUI
Andi Sukandi	Bpk. Aria Nurrahman, S.T	Bpk. Faris Djibran, S.T
SKALA	KODE DATA	NO GAMBAR
1:100	STR	3105

RENCANA INSTALASI AIR KOTOR
SKALA 1 : 100

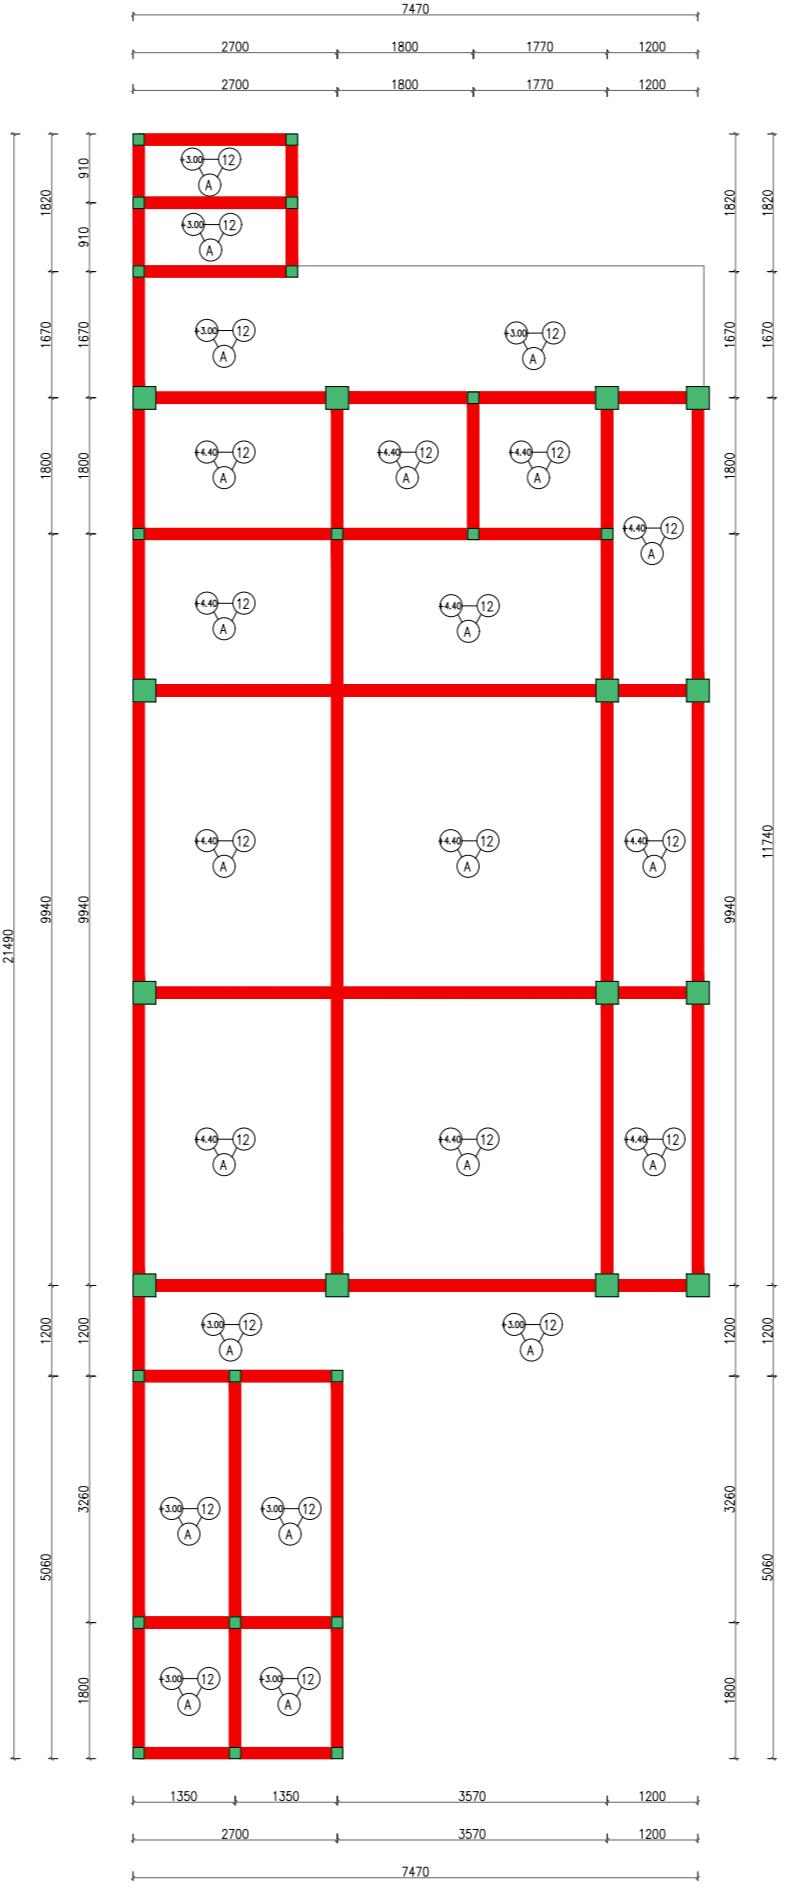


PROJECT / PROYEK																						
Pembangunan Mushola Darul Sholihin																						
OWNER / PEMILIK																						
Hamba ALLAH																						
CATATAN																						
CATATAN : <ul style="list-style-type: none"> - Semua dimensi dalam satuan Milimeter (mm), kecuali ditentukan yang lain - Semua elevasi dalam satuan Milimeter (mm), kecuali ditentukan yang lain 																						
LEGENDA : <ul style="list-style-type: none"> - FFL : Finishing Floor Level (Ketinggian Lantai) - EL : Elevasi (Ketinggian) - GL : Ground Level (Elevasi Muka Tanah) - CH : Ceiling High (Ketinggian Plafon) - FCS : Finishing Concrete High (Tinggi Dak Beton) - RH : Roof High (Ketinggian Atap) 																						
SIMBOL : <table border="0"> <tr> <td></td> <td>: Pas. 1 / 2 Bata</td> </tr> <tr> <td></td> <td>: Dinding Trasram</td> </tr> <tr> <td></td> <td>: Kolom Existing</td> </tr> <tr> <td></td> <td>: Kolom Baru</td> </tr> <tr> <td></td> <td>: Dinding Existing</td> </tr> <tr> <td></td> <td>: Dinding Renovasi</td> </tr> <tr> <td></td> <td>: Garis Atap</td> </tr> <tr> <td></td> <td>: Garis Potong</td> </tr> <tr> <td></td> <td>: Garis As Kolom (Grid)</td> </tr> <tr> <td></td> <td>: Garis Elevasi</td> </tr> </table>				: Pas. 1 / 2 Bata		: Dinding Trasram		: Kolom Existing		: Kolom Baru		: Dinding Existing		: Dinding Renovasi		: Garis Atap		: Garis Potong		: Garis As Kolom (Grid)		: Garis Elevasi
	: Pas. 1 / 2 Bata																					
	: Dinding Trasram																					
	: Kolom Existing																					
	: Kolom Baru																					
	: Dinding Existing																					
	: Dinding Renovasi																					
	: Garis Atap																					
	: Garis Potong																					
	: Garis As Kolom (Grid)																					
	: Garis Elevasi																					
TIM PERENCANA																						
SHEET TITLE / JUDUL GAMBAR																						
RENCANA DENAH PLAT LANTAI																						
DI GAMBAR	DI PERIKSA	DI SETUJUI																				
Andi Sukandi	Bpk. Aria Nurrahman, S.T	Bpk. Faris Djibrain, S.T																				
SKALA	KODE DATA	NO GAMBAR																				
1:100	STR	3106																				

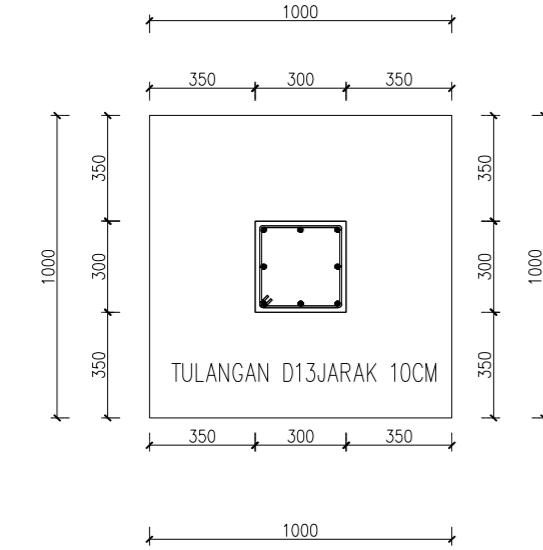

DENAH PONDASI (P1)


SKALA 1 : 40

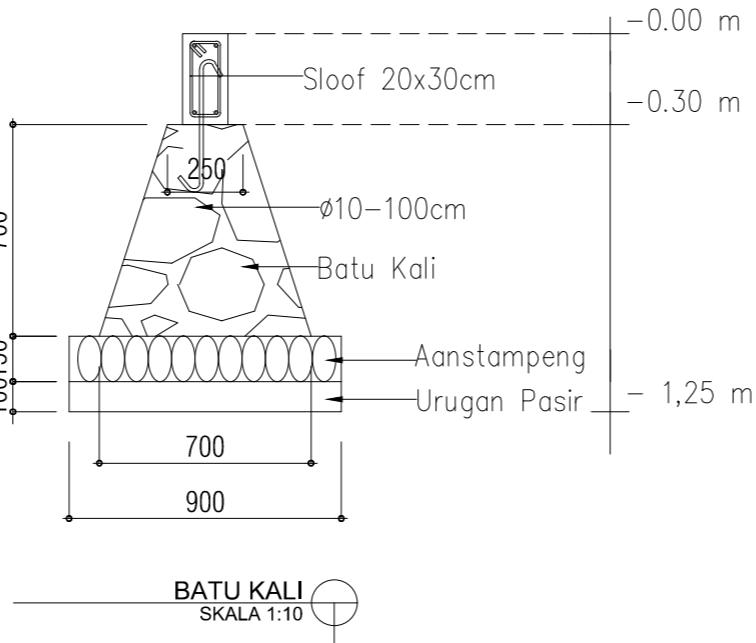

BATU KALI
SKALA 1:10


DENAH PONDASI (P2)

SKALA 1 : 40

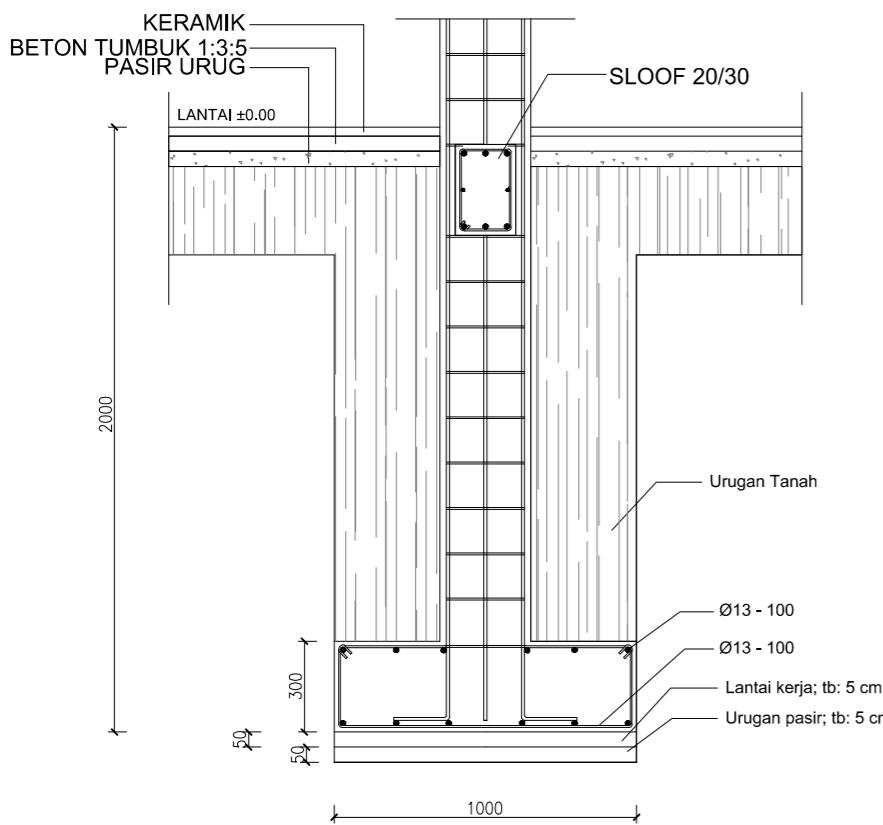

POTONGAN PONDASI (P1)

SKALA 1 : 40

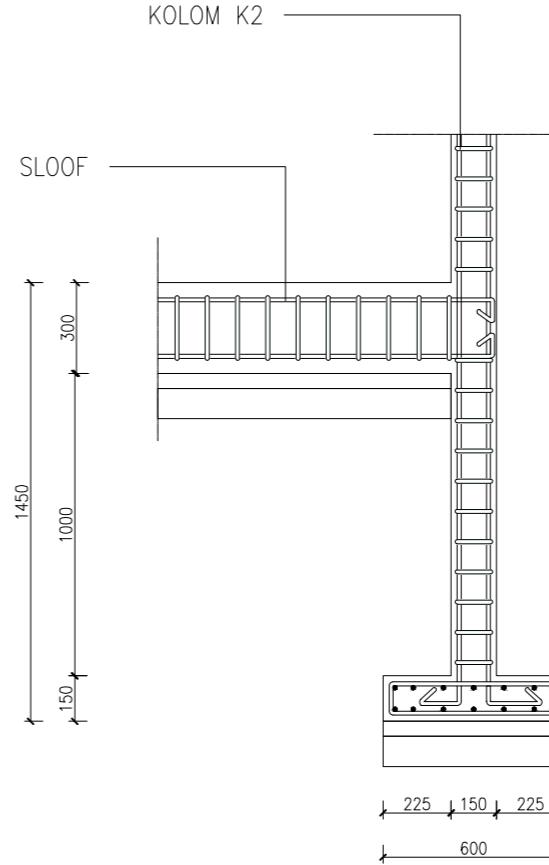

POTONGAN PONDASI (P2)

SKALA 1 : 40

PROJECT / PROYEK

Pembangunan Mushola
Darul Sholihin

OWNER / PEMILIK

Hamba ALLAH

CATATAN

TIM PERENCANA

SHEET TITLE / JUDUL GAMBAR

DETAIL PONDASI #1

DI GAMBAR	DI PERIKSA	DI SETUJUI
Andi Sukandi	Bpk. Aria Nurrahman, S.T	Bpk. Faris Djibrain, S.T
SKALA	KODE DATA	NO GAMBAR
1:25	STR	3107

TYPE BALOK	B1		B2		B3	
	TUMPUAN	LAPANGAN	TUMPUAN	LAPANGAN	TUMPUAN	LAPANGAN
DETAIL						
DIMENSI	20X40CM	20X40CM	15X30CM	15X30CM	10X20CM	10X20CM
TULANGAN ATAS	3D13	2D13	2D13	2D13	2D10	2D13
TULANGAN TENGAH	2D13	2D13	2D13	2D13	-	-
TULANGAN BAWAH	2D13	3D13	2D13	2D13	2D10	2D10
SENGKANG	Ø8-200	Ø8-200	Ø8-200	Ø8-200	Ø8-150	Ø8-150
SELIMUT BETON	2,5 CM	2,5 CM	2,5 CM	2,5 CM	2,5 CM	2,5 CM

DETAIL PENULANGAN BALOK

SKALA 1 : 25

TYPE KOLOM	KP			
	TUMPUAN	LAPANGAN	TUMPUAN	LAPANGAN
DETAIL				
DIMENSI	15X15CM	15X15CM	30X30CM	30X30CM
TULANGAN UTAMA	4D10	4D10	8 D13	8 D13
SENGKANG	Ø8-150	Ø8-150	Ø8-150	Ø8-150
SELIMUT BETON	2 CM	2 CM	2,5 CM	2,5 CM

DETAIL PENULANGAN KOLOM

SKALA 1 : 25

TYPE SLOOF	SL1	
	TUMPUAN	LAPANGAN
DETAIL		
DIMENSI	20X30CM	20X30CM
TULANGAN ATAS	3D13	3D13
TULANGAN TENGAH	-	-
TULANGAN BAWAH	3D13	3D13
SENGKANG	Ø8-200	Ø8-200
SELIMUT BETON	2,5 CM	2,5 CM

DETAIL PENULANGAN SLOOF

SKALA 1 : 25

PROJECT / PROYEK

Pembangunan Mushola
Darul Sholihin

OWNER / PEMILIK

Hamba ALLAH

CATATAN

TIM PERENCANA

SHEET TITLE / JUDUL GAMBAR

DETAIL PONDASI #2

DI GAMBAR DI PERIKSA DI SETUJUI

Andi Sukandi Bpk. Aria Nurrahman, S.T. **Bpk. Faris Djibrain, S.T**

SKALA KODE DATA NO GAMBAR

1:25 STR 3108

PROJECT / PROYEK

Pembangunan Mushola
Darul Sholihin

OWNER / PEMILIK

Hamba ALLAH


CATATAN

TIM PERENCANA


SHEET TITLE / JUDUL GAMBAR

DETAIL PLAT LANTAI


DI GAMBAR	DI PERIKSA	DI SETUJUI
Andi Sukandi	Bpk. Aria Nurrahman, S.T	Bpk. Faris Djibrain, S.T
SKALA	KODE DATA	NO GAMBAR
1:40	STR	3109

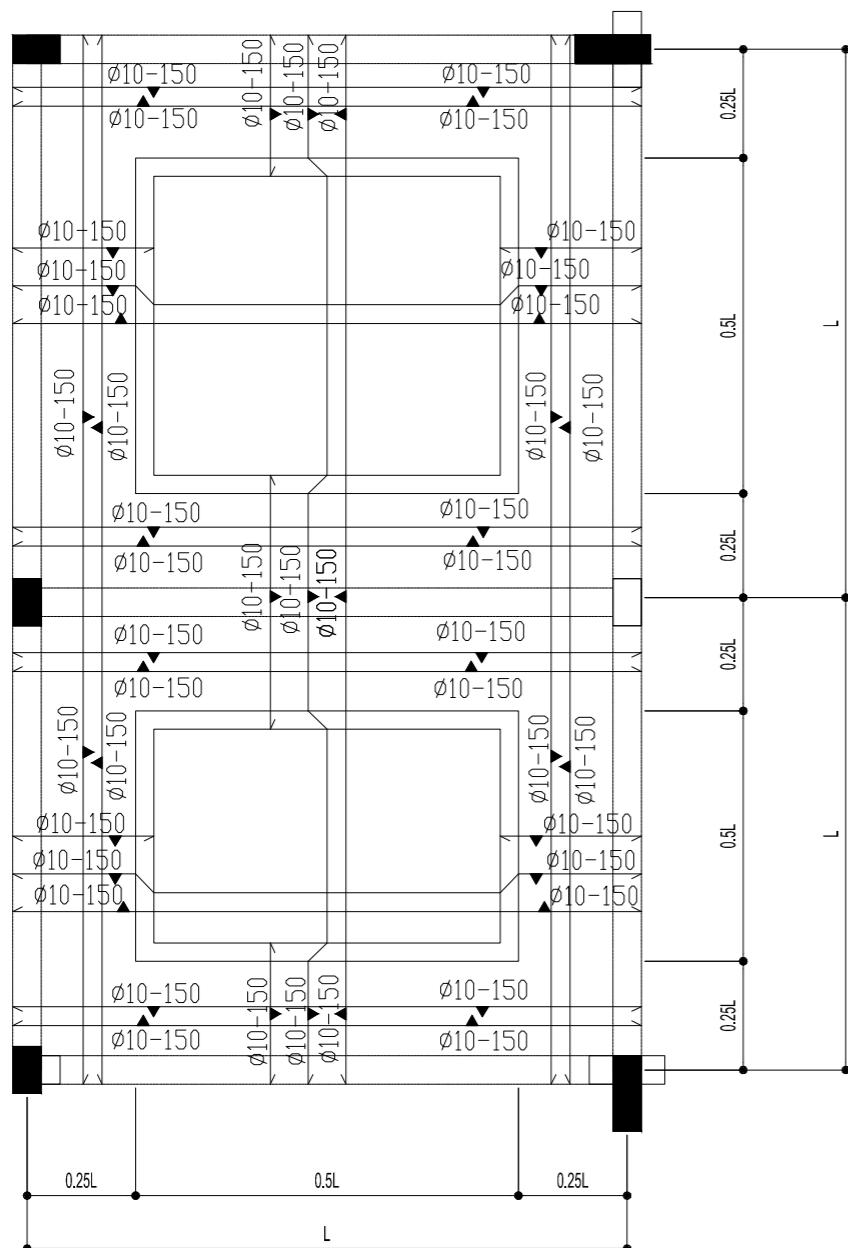

DETAIL PELAT A
SKALA 1:35

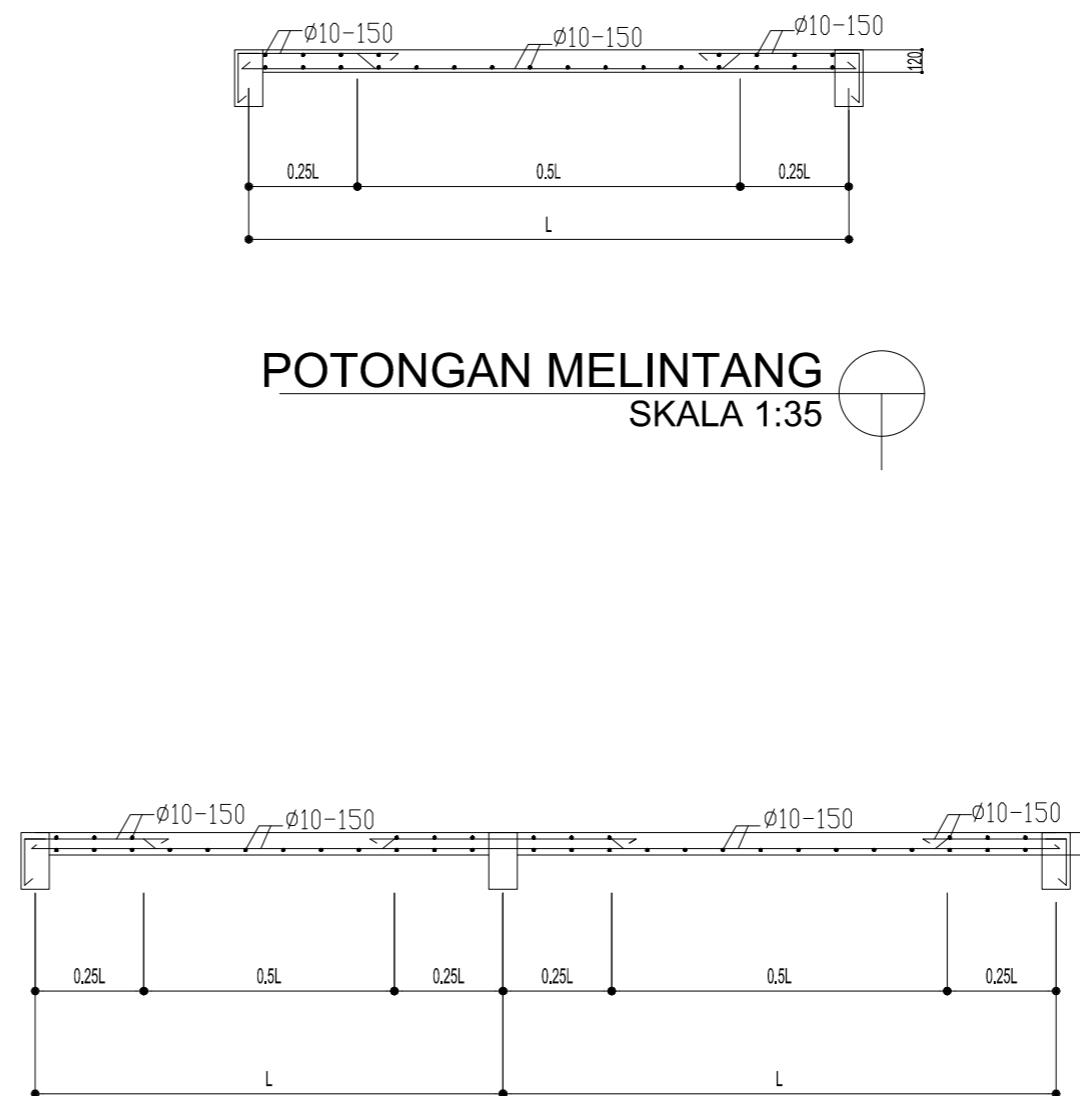

POTONGAN MELINTANG
SKALA 1:35

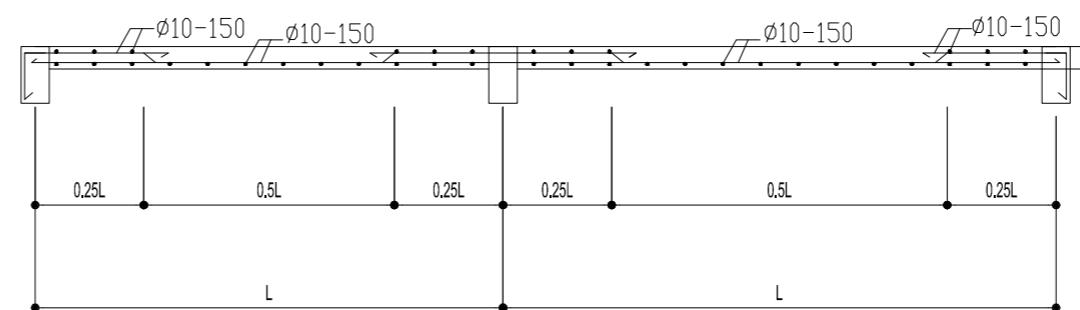

POTONGAN MEMANJANG
SKALA 1:35